


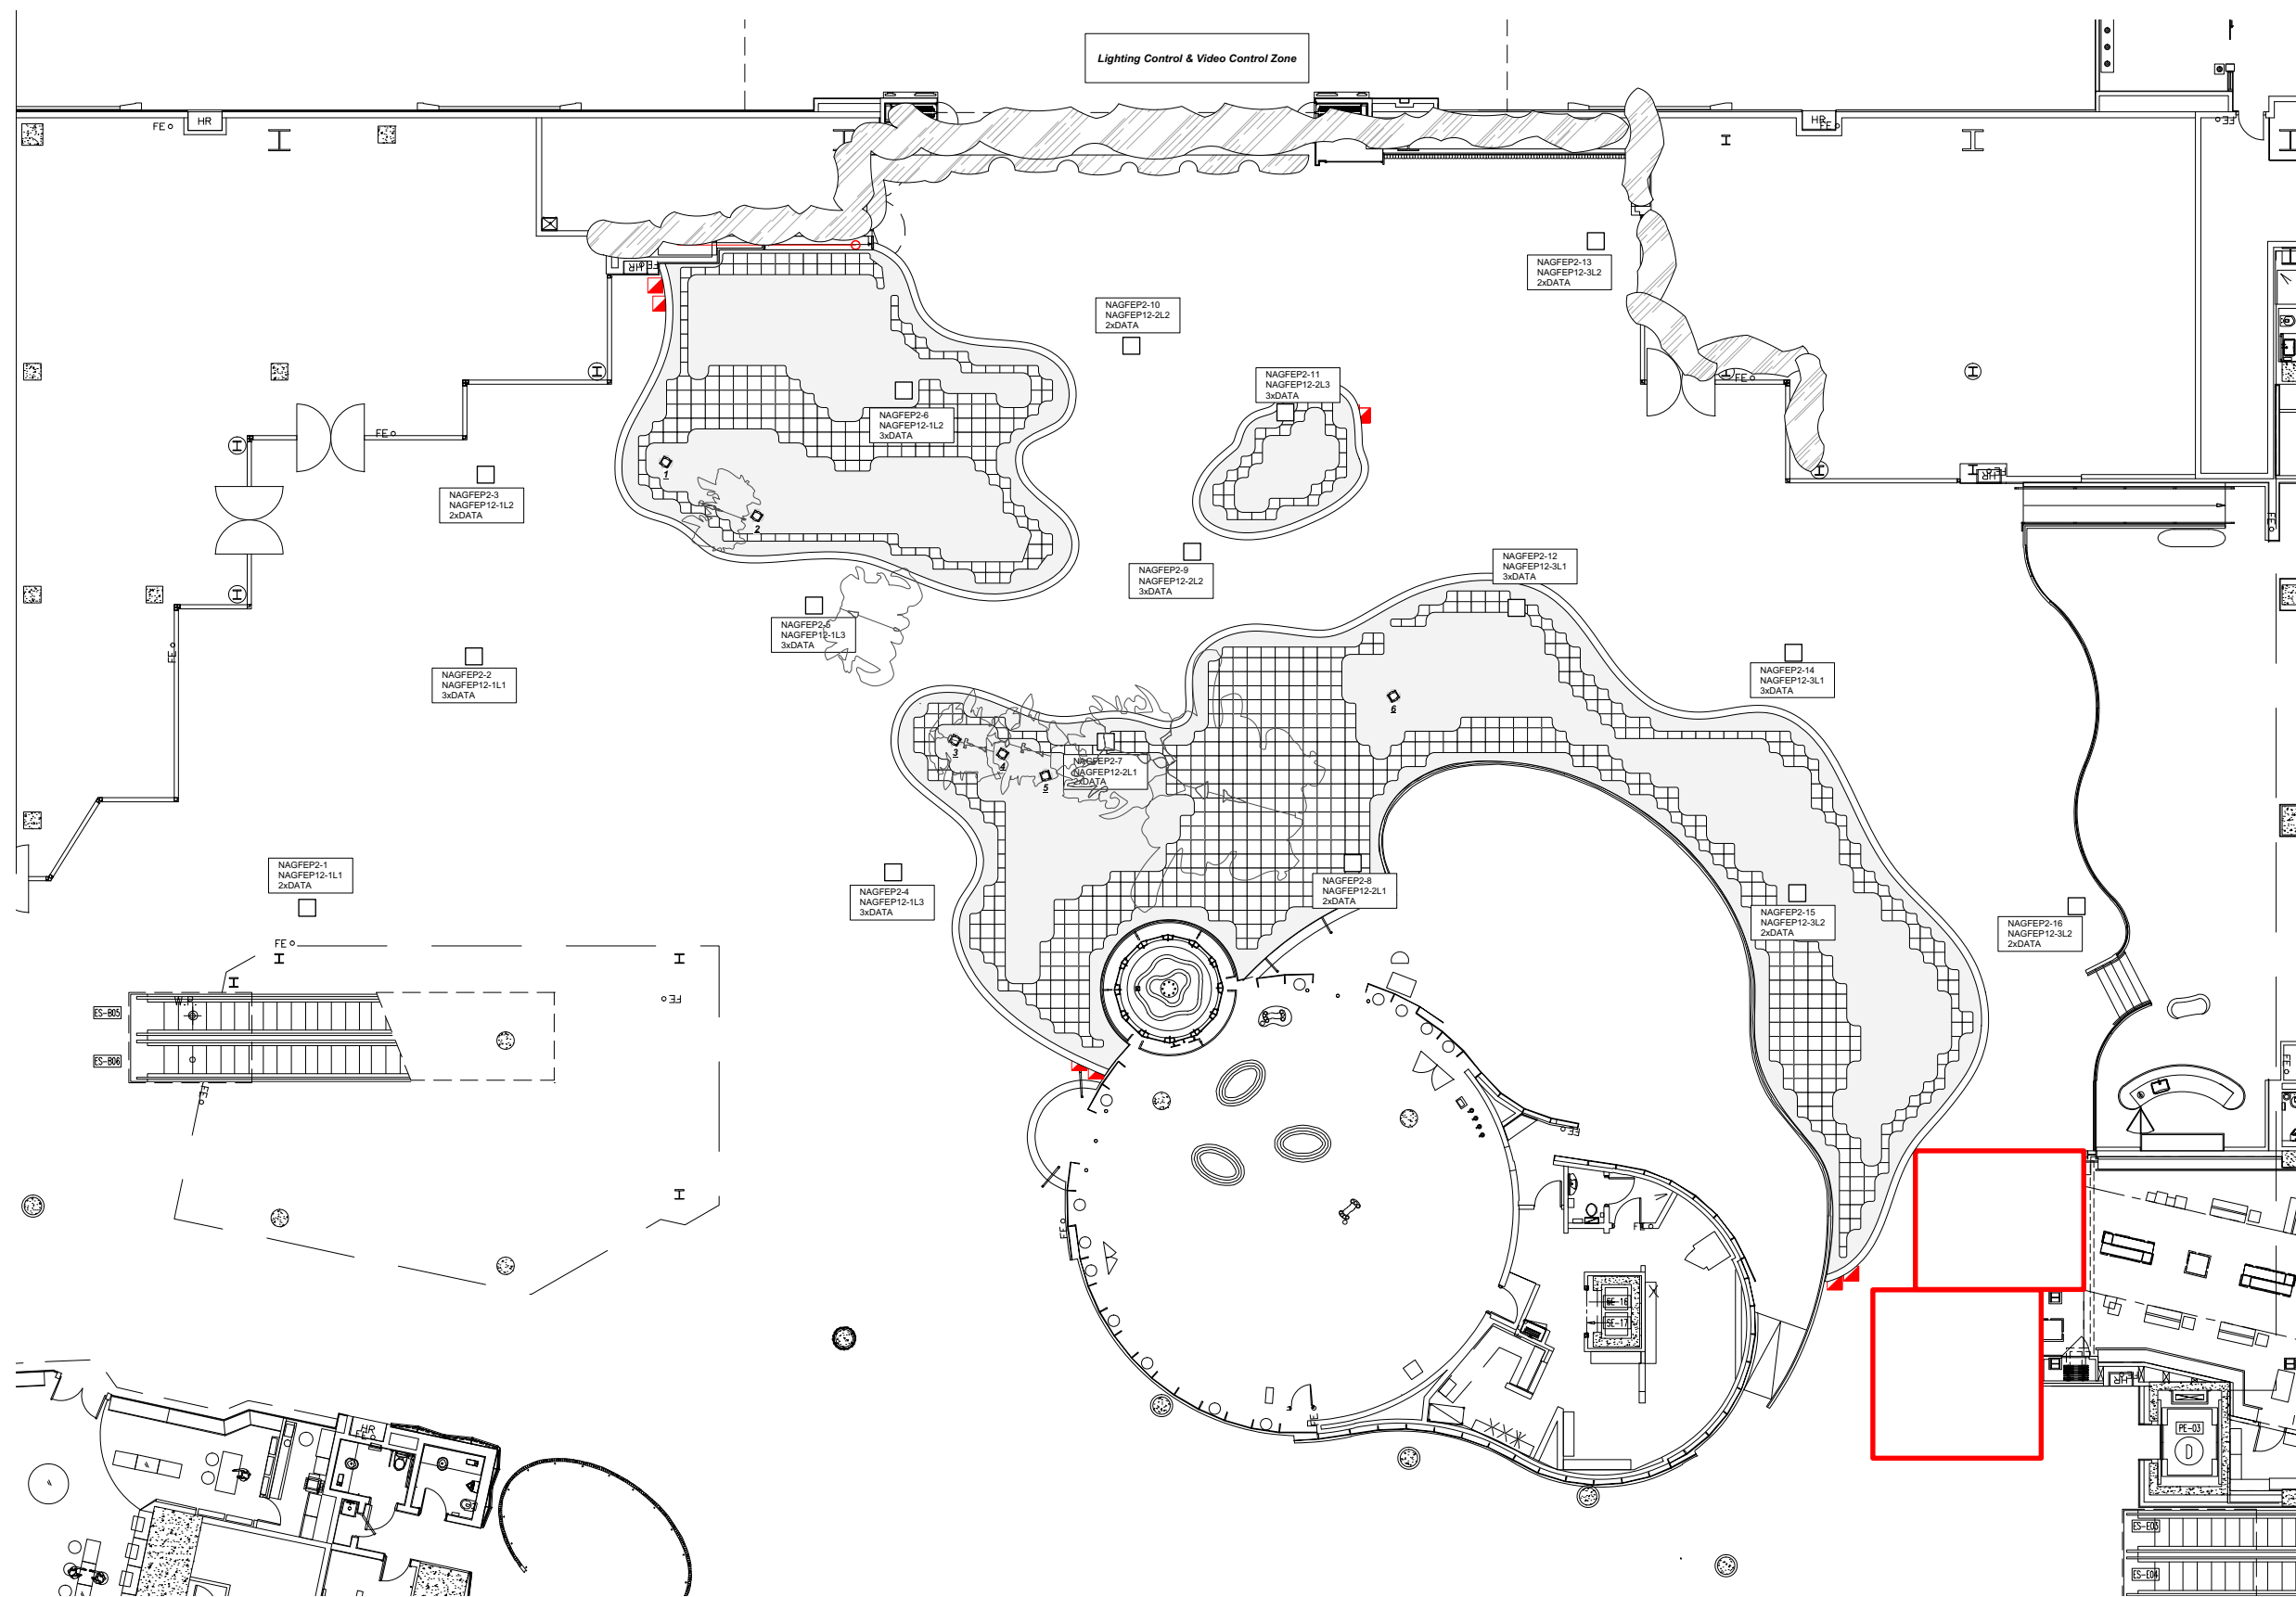

KEY:

- LED彩砖 (500*500mm)
LED Panel (500*500mm)
- 电脑摇头切割灯
Moving Light Profile Fine 600L

Cable legend

- 3*1.5mm² Power Cable
Plug must match the moving light
- 3*1mm² Power Cable
Use 13A power plug
- 5*0.5mm² DMX Cable
Plug must match the moving light
- Wireless DMX signal
From Transmitter to Receiver

Lighting Equipments Layout

Scale 1:250 / A3


蛻變:無窮盡

A Metamorphosis: No End to End

展示設計: 馬文
燈光設計: 蕭麗河
制圖: 喬仕敏



2019-5-26 v8

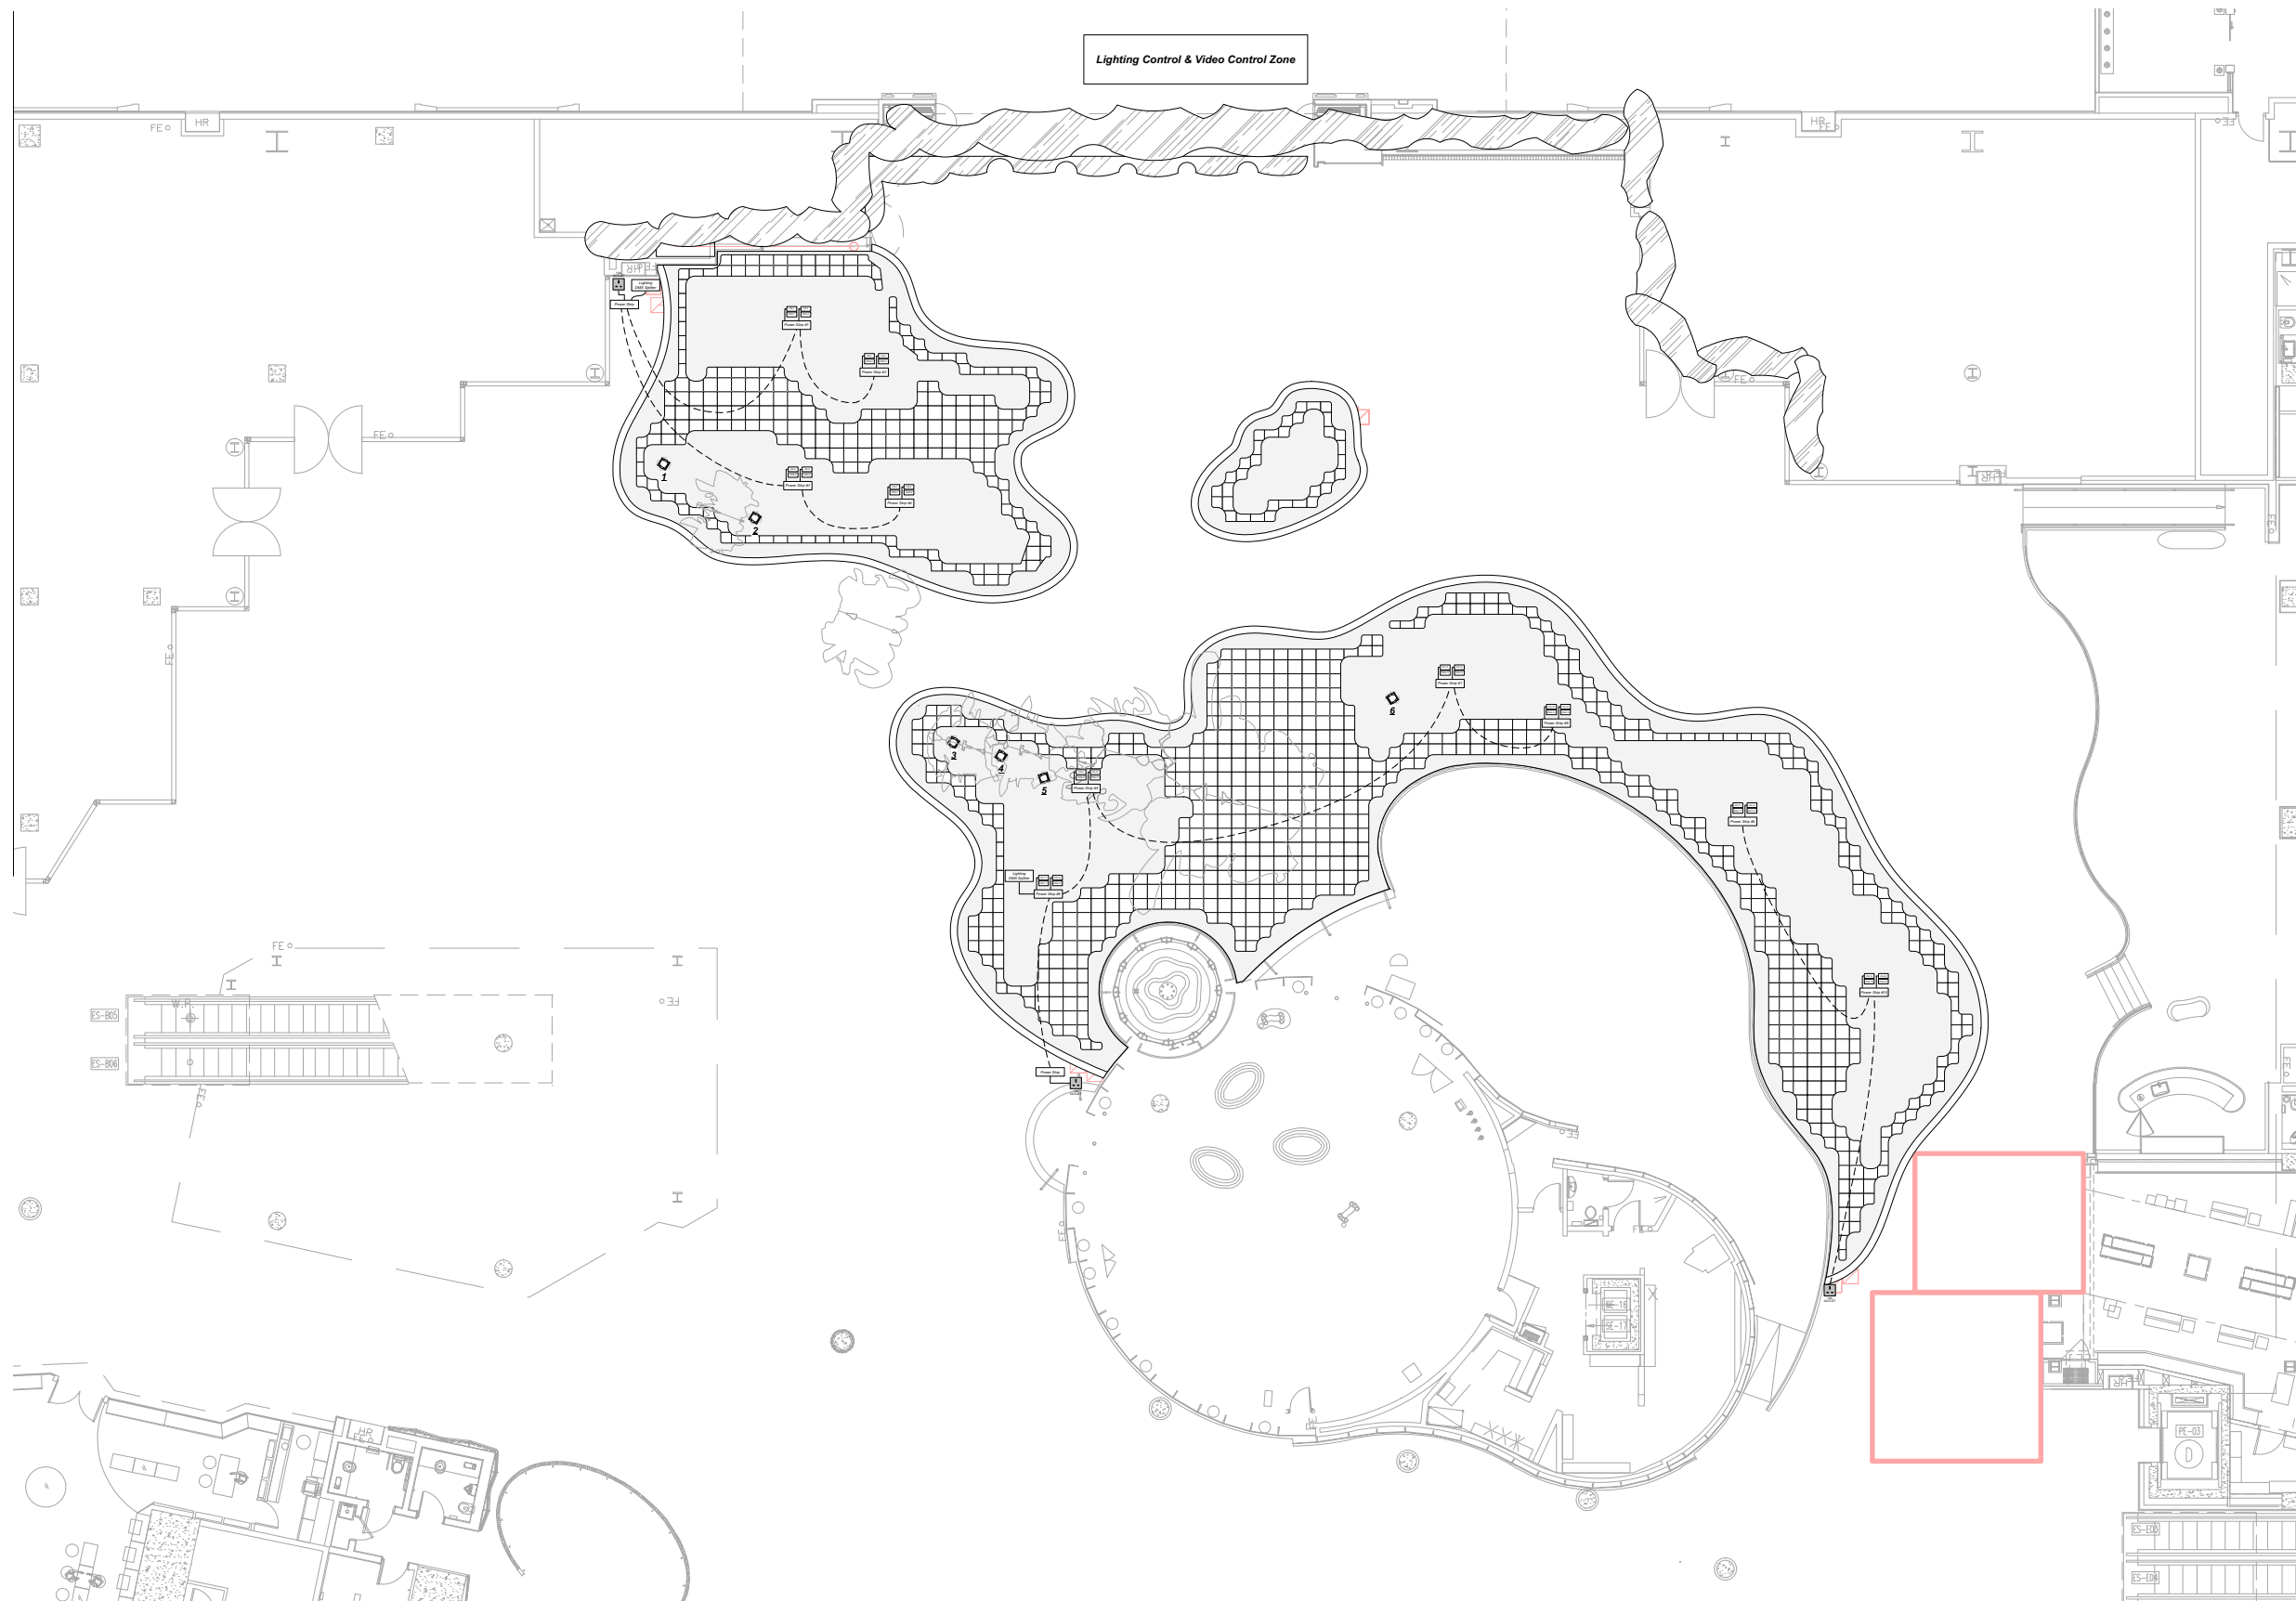

KEY:

- LED彩砖 (500*500mm)
LED Panel (500*500mm)
- 电脑摇头切割灯
Moving Light - Fine 600L

Cable legend

- 3*1.5mm² Power Cable
Plug must match the moving light
- 3*1mm² Power Cable
Use 13A power plug
- 5*0.5mm² DMX Cable
Plug must match the moving light
- Wireless DMX signal
From Transmitter to Receiver

- | | |
|-------------|---------------------------------------|
| PS | Power Supply
For star light |
| PDS | Power Data Supply
For star light |
| Power Strip | Power Strip
For power distribution |

Power Cabling Plan for Star Light

Scale 1:250 / A3

蛻變:無窮盡

A Metamorphosis: No End to End

展示設計: 馬文
燈光設計: 蕭麗河
制圖: 喬仕敏



2019-5-26 v8



KEY:

- LED彩砖 (500*500mm)
LED Panel (500*500mm)
- 电脑摇头切割灯
Moving Light - Fine 600L

Cable legend

- 3*1.5mm² Power Cable
Plug must match the moving light
- 3*1mm² Power Cable
Use 13A power plug
- 5*0.5mm² DMX Cable
Plug must match the moving light
- Wireless DMX signal
From Transmitter to Receiver

- PS Power Supply
For star light
- PDS Power Data Supply
For star light
- Power Strip Power Strip
For power distribution

DMX Cabling Plan for Star Light & Moving Light

Scale 1:250 / A3


蛻變:無窮盡

A Metamorphosis: No End to End

展示設計: 馬文
燈光設計: 蕭麗河
制圖: 喬仕敏



2019-5-26 v8

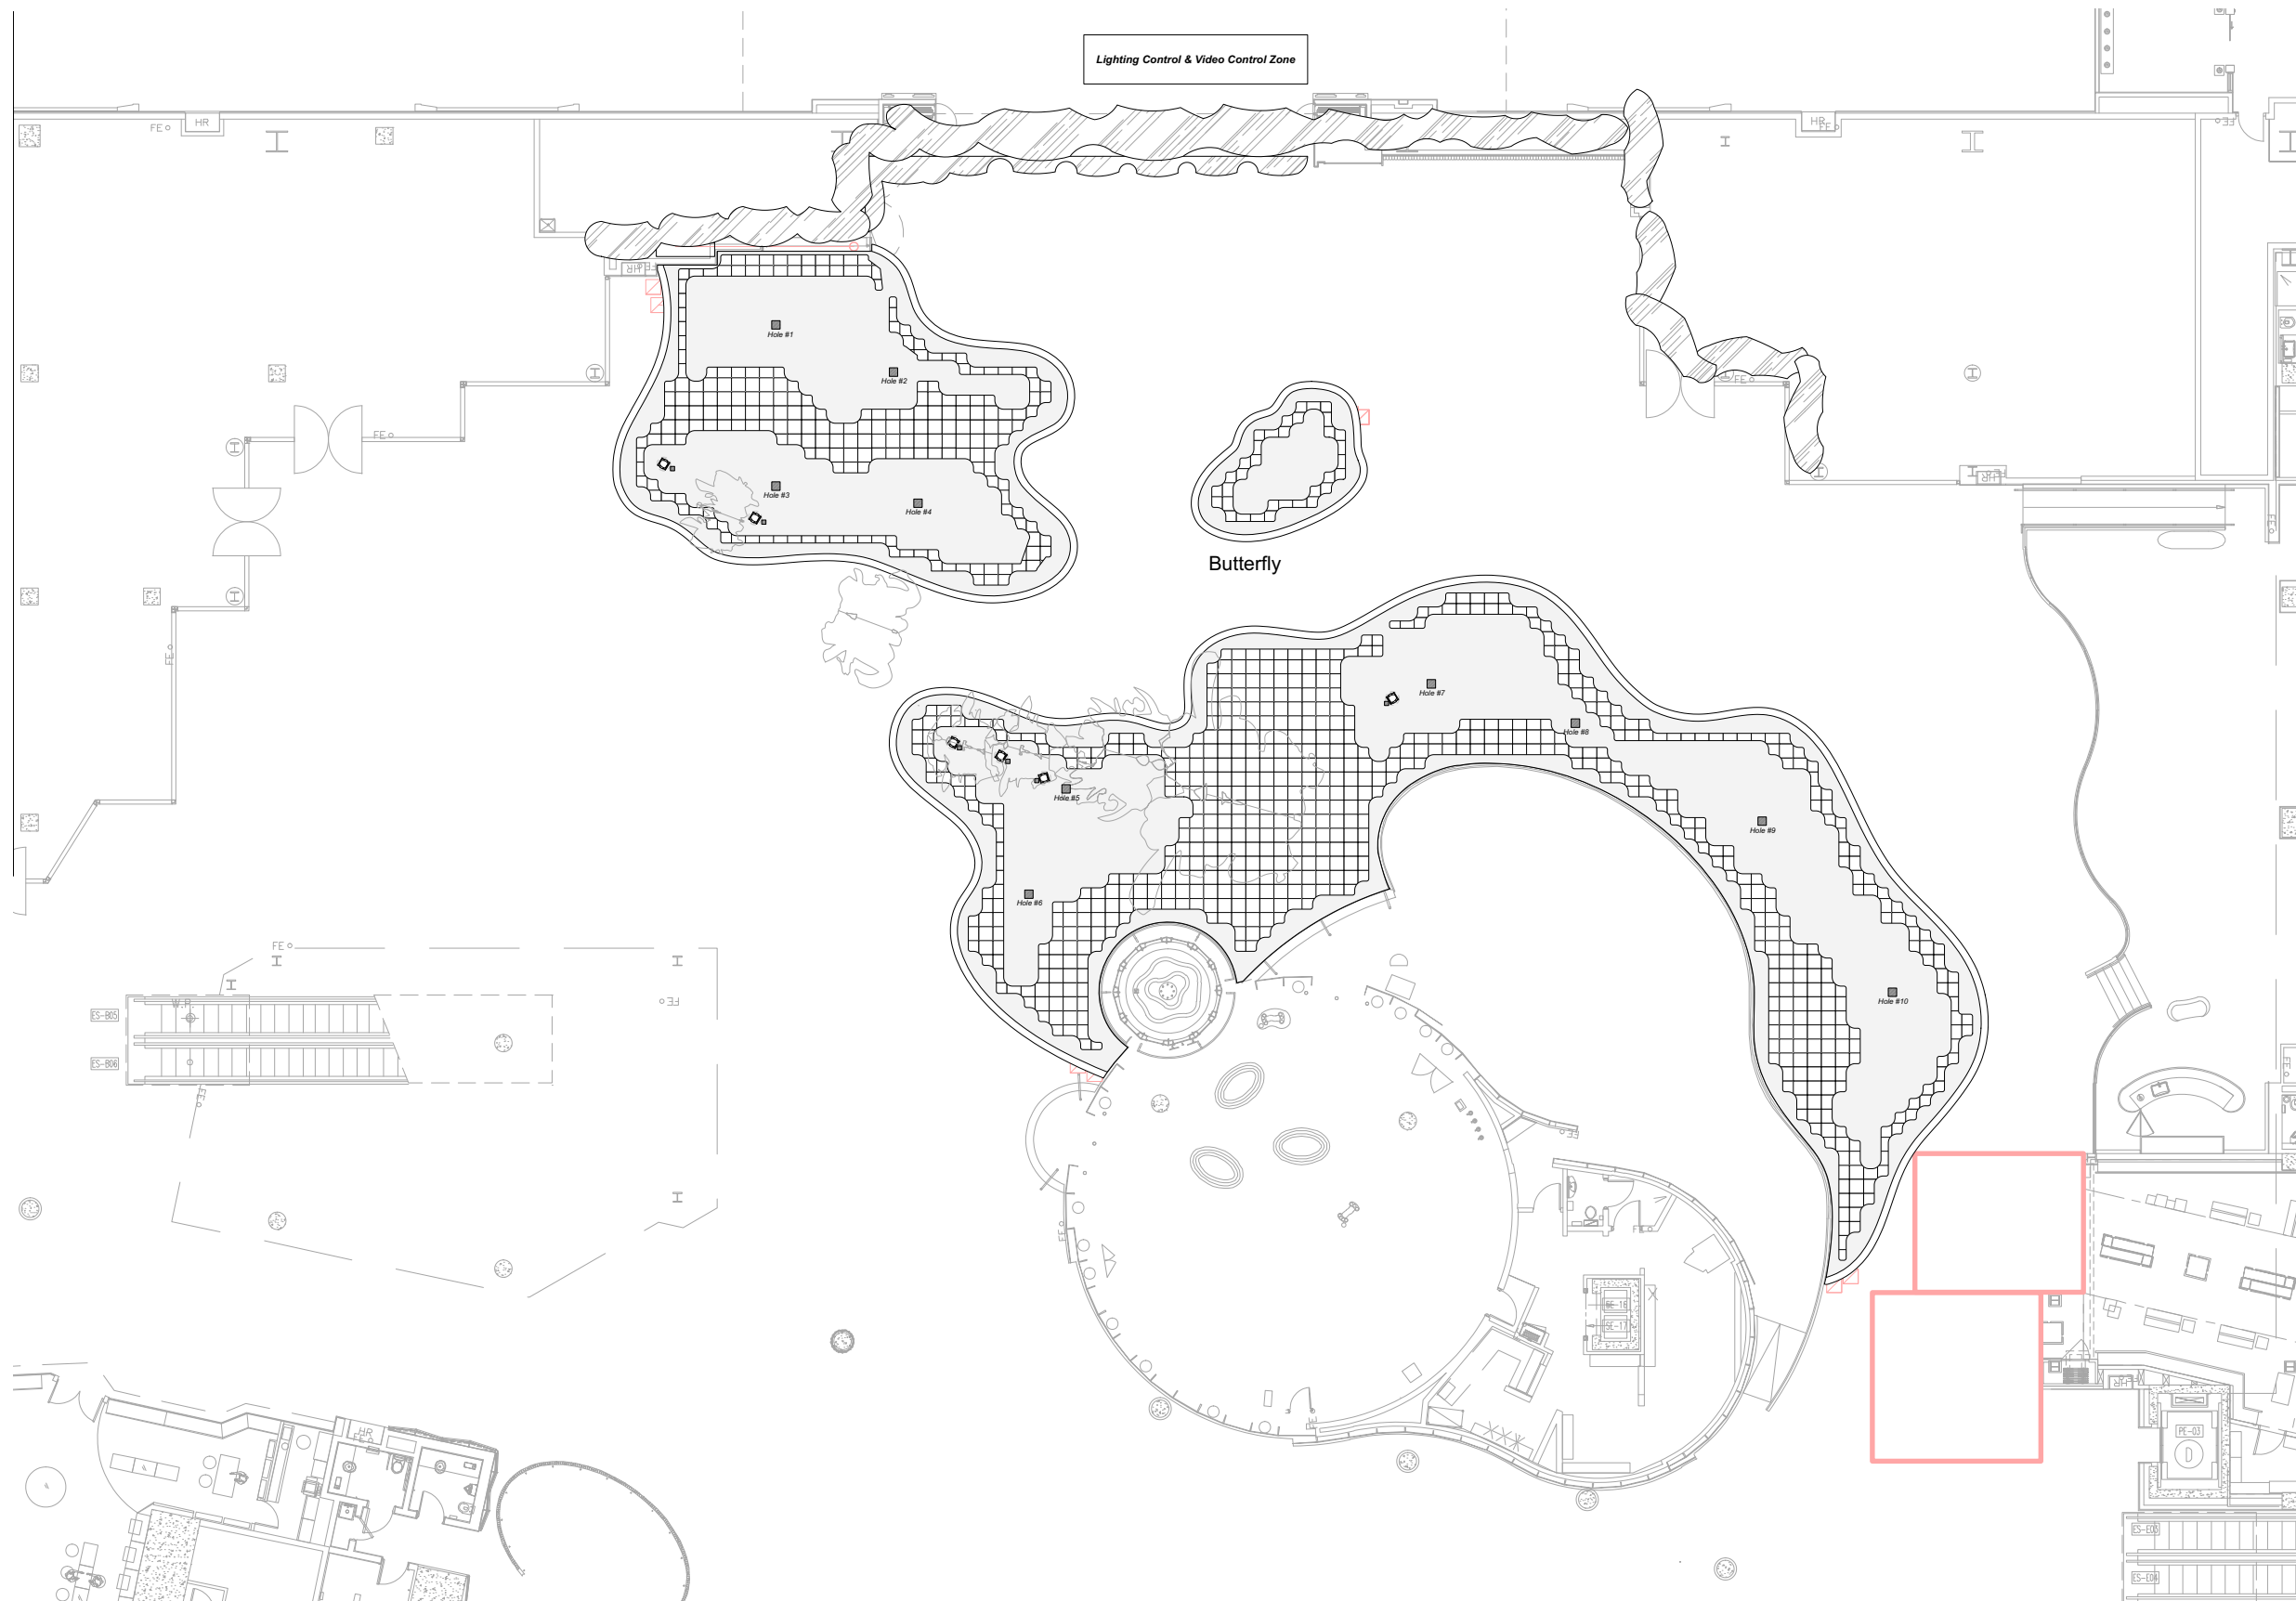

KEY:

- LED彩砖 (500*500mm)
LED Panel (500*500mm)
- 电脑摇头切割灯
Moving Light - Fine 600L

Cable legend

- 3*1.5mm² Power Cable
Plug must match the moving light
- 3*1mm² Power Cable
Use 13A power plug
- 5*0.5mm² DMX Cable
Plug must match the moving light
- Wireless DMX signal
From Transmitter to Receiver

- 150*150 mm
Access Hole for moving light
- 300*300 mm
Access Hole for star light

Access Hole layout

Scale 1:250 / A3


蛻變:無窮盡

A Metamorphosis: No End to End


展示設計: 馬文
燈光設計: 蕭麗河
制圖: 喬仕敏




2019-5-26 v8

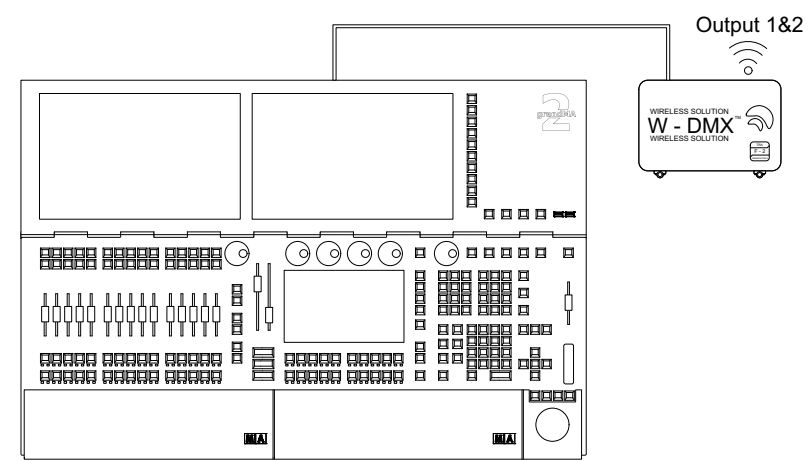

**GrandMA2 Light
Lighting Console**

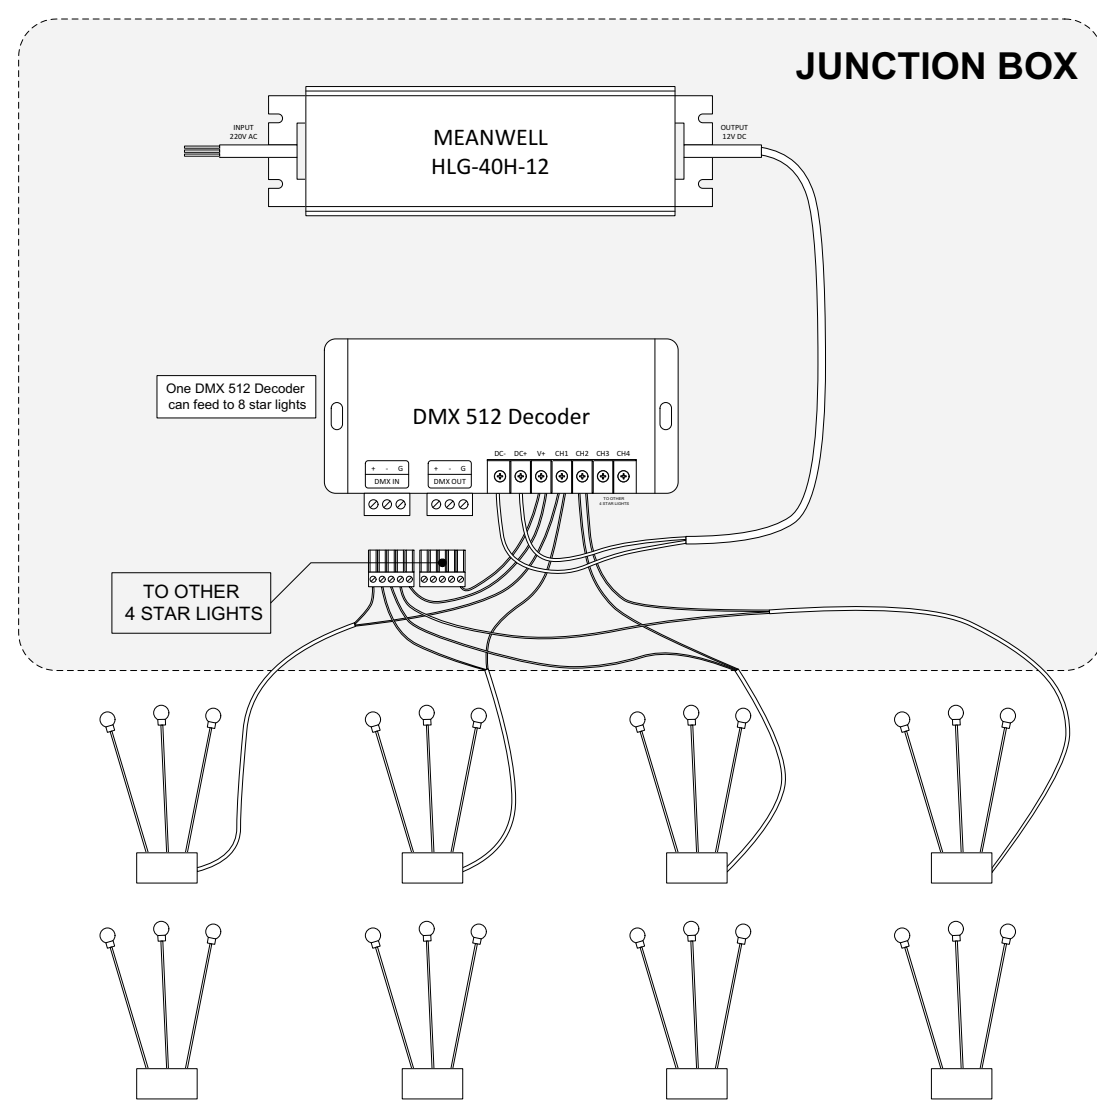

General Diagram for Star Light

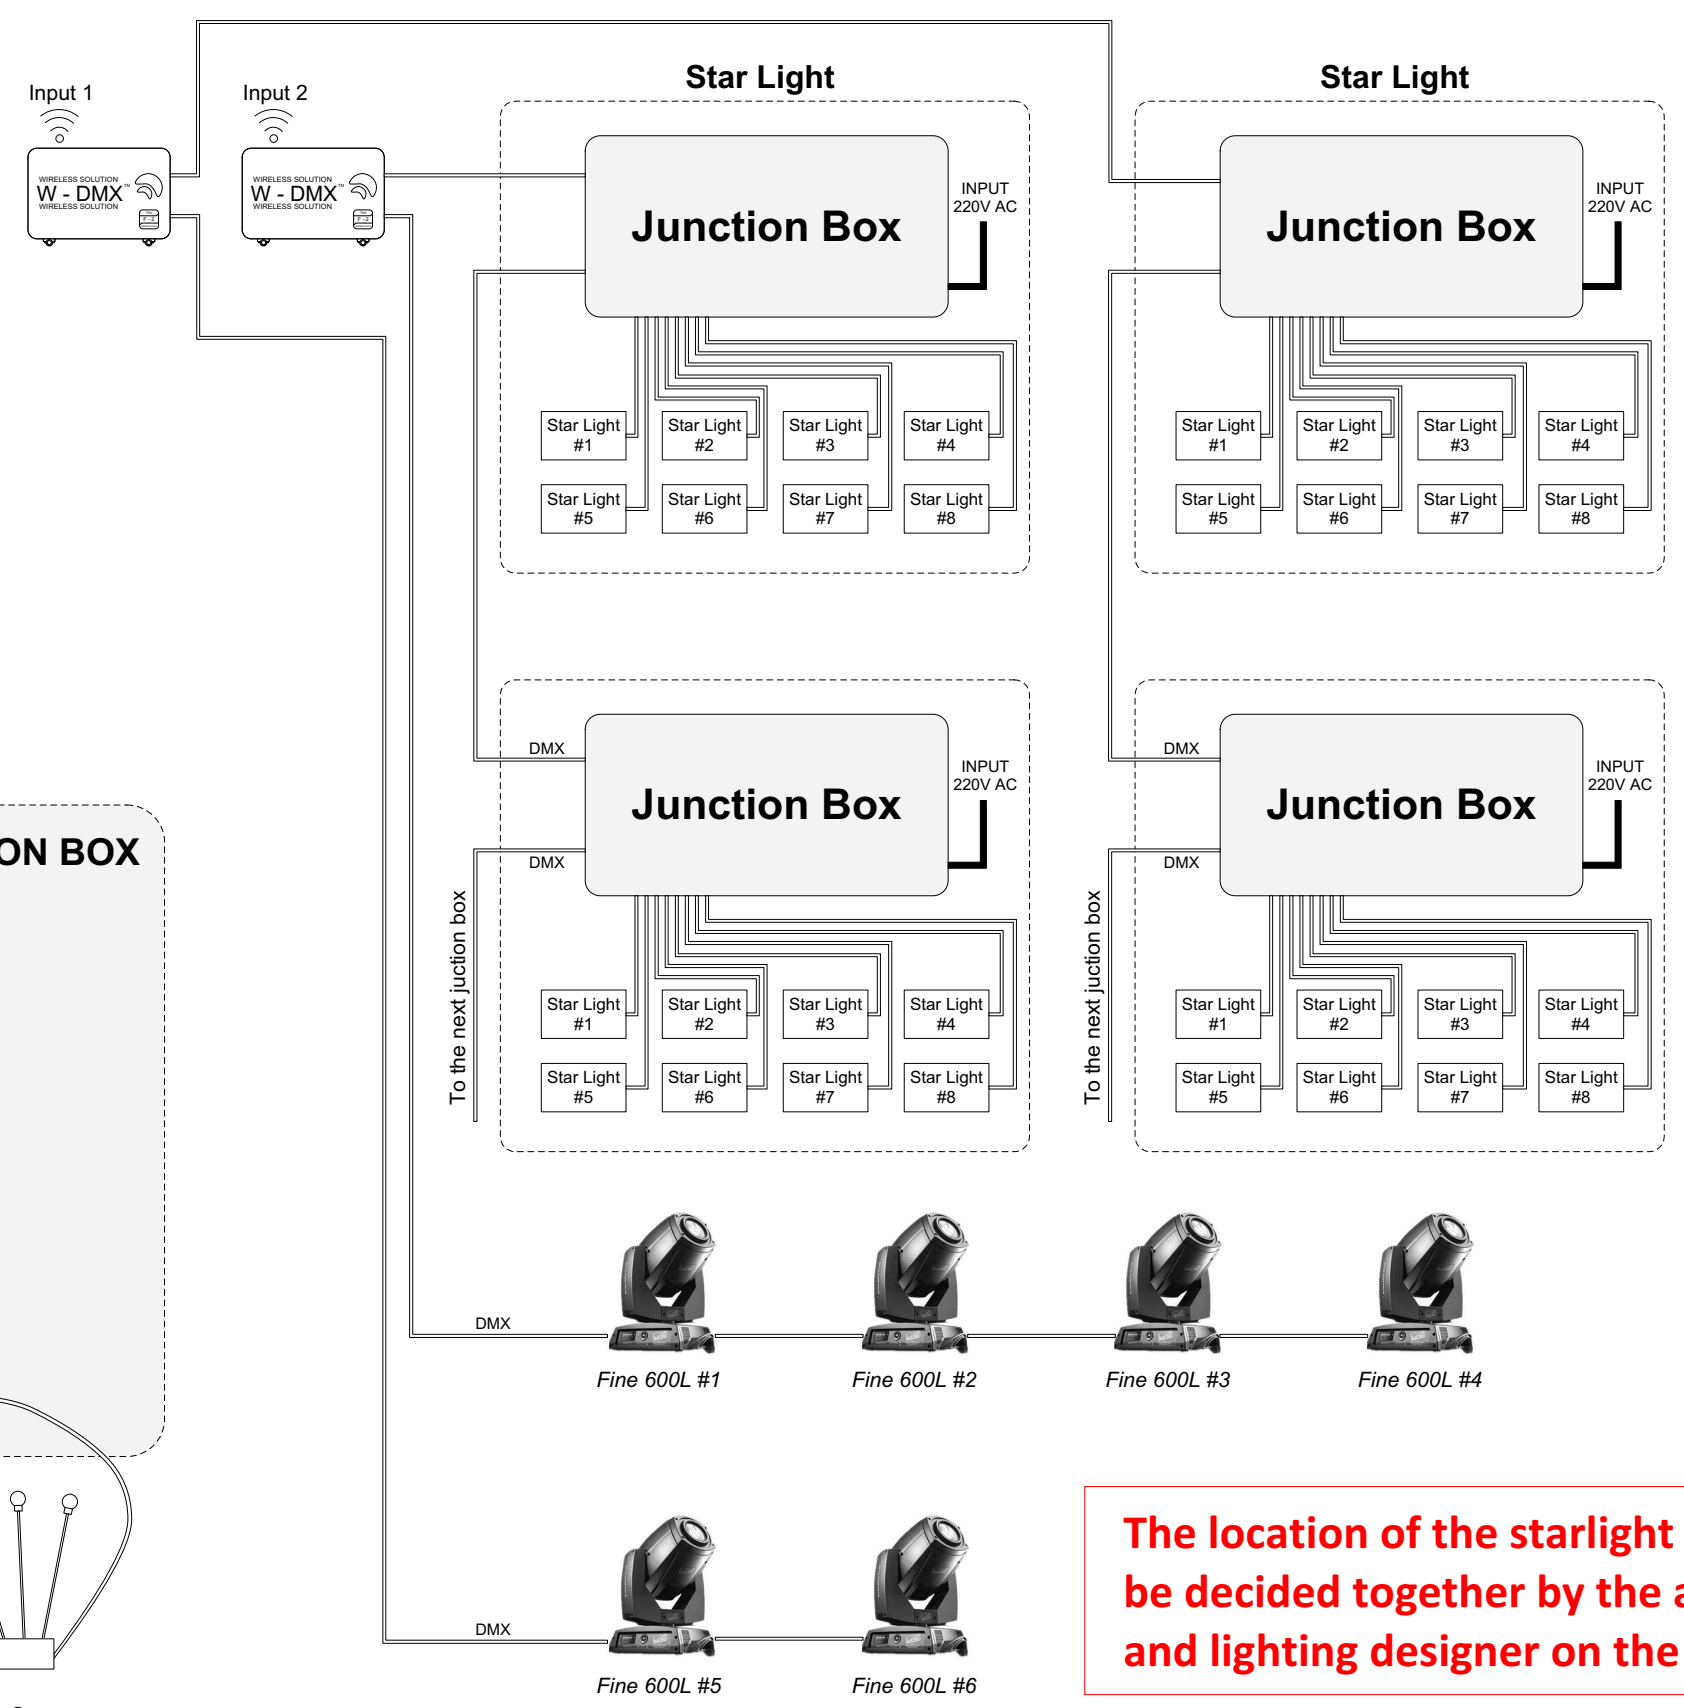

**The location of the starlight will
be decided together by the artist
and lighting designer on the site**

Lighting General Diagram

A Metamorphosis: No End to End