


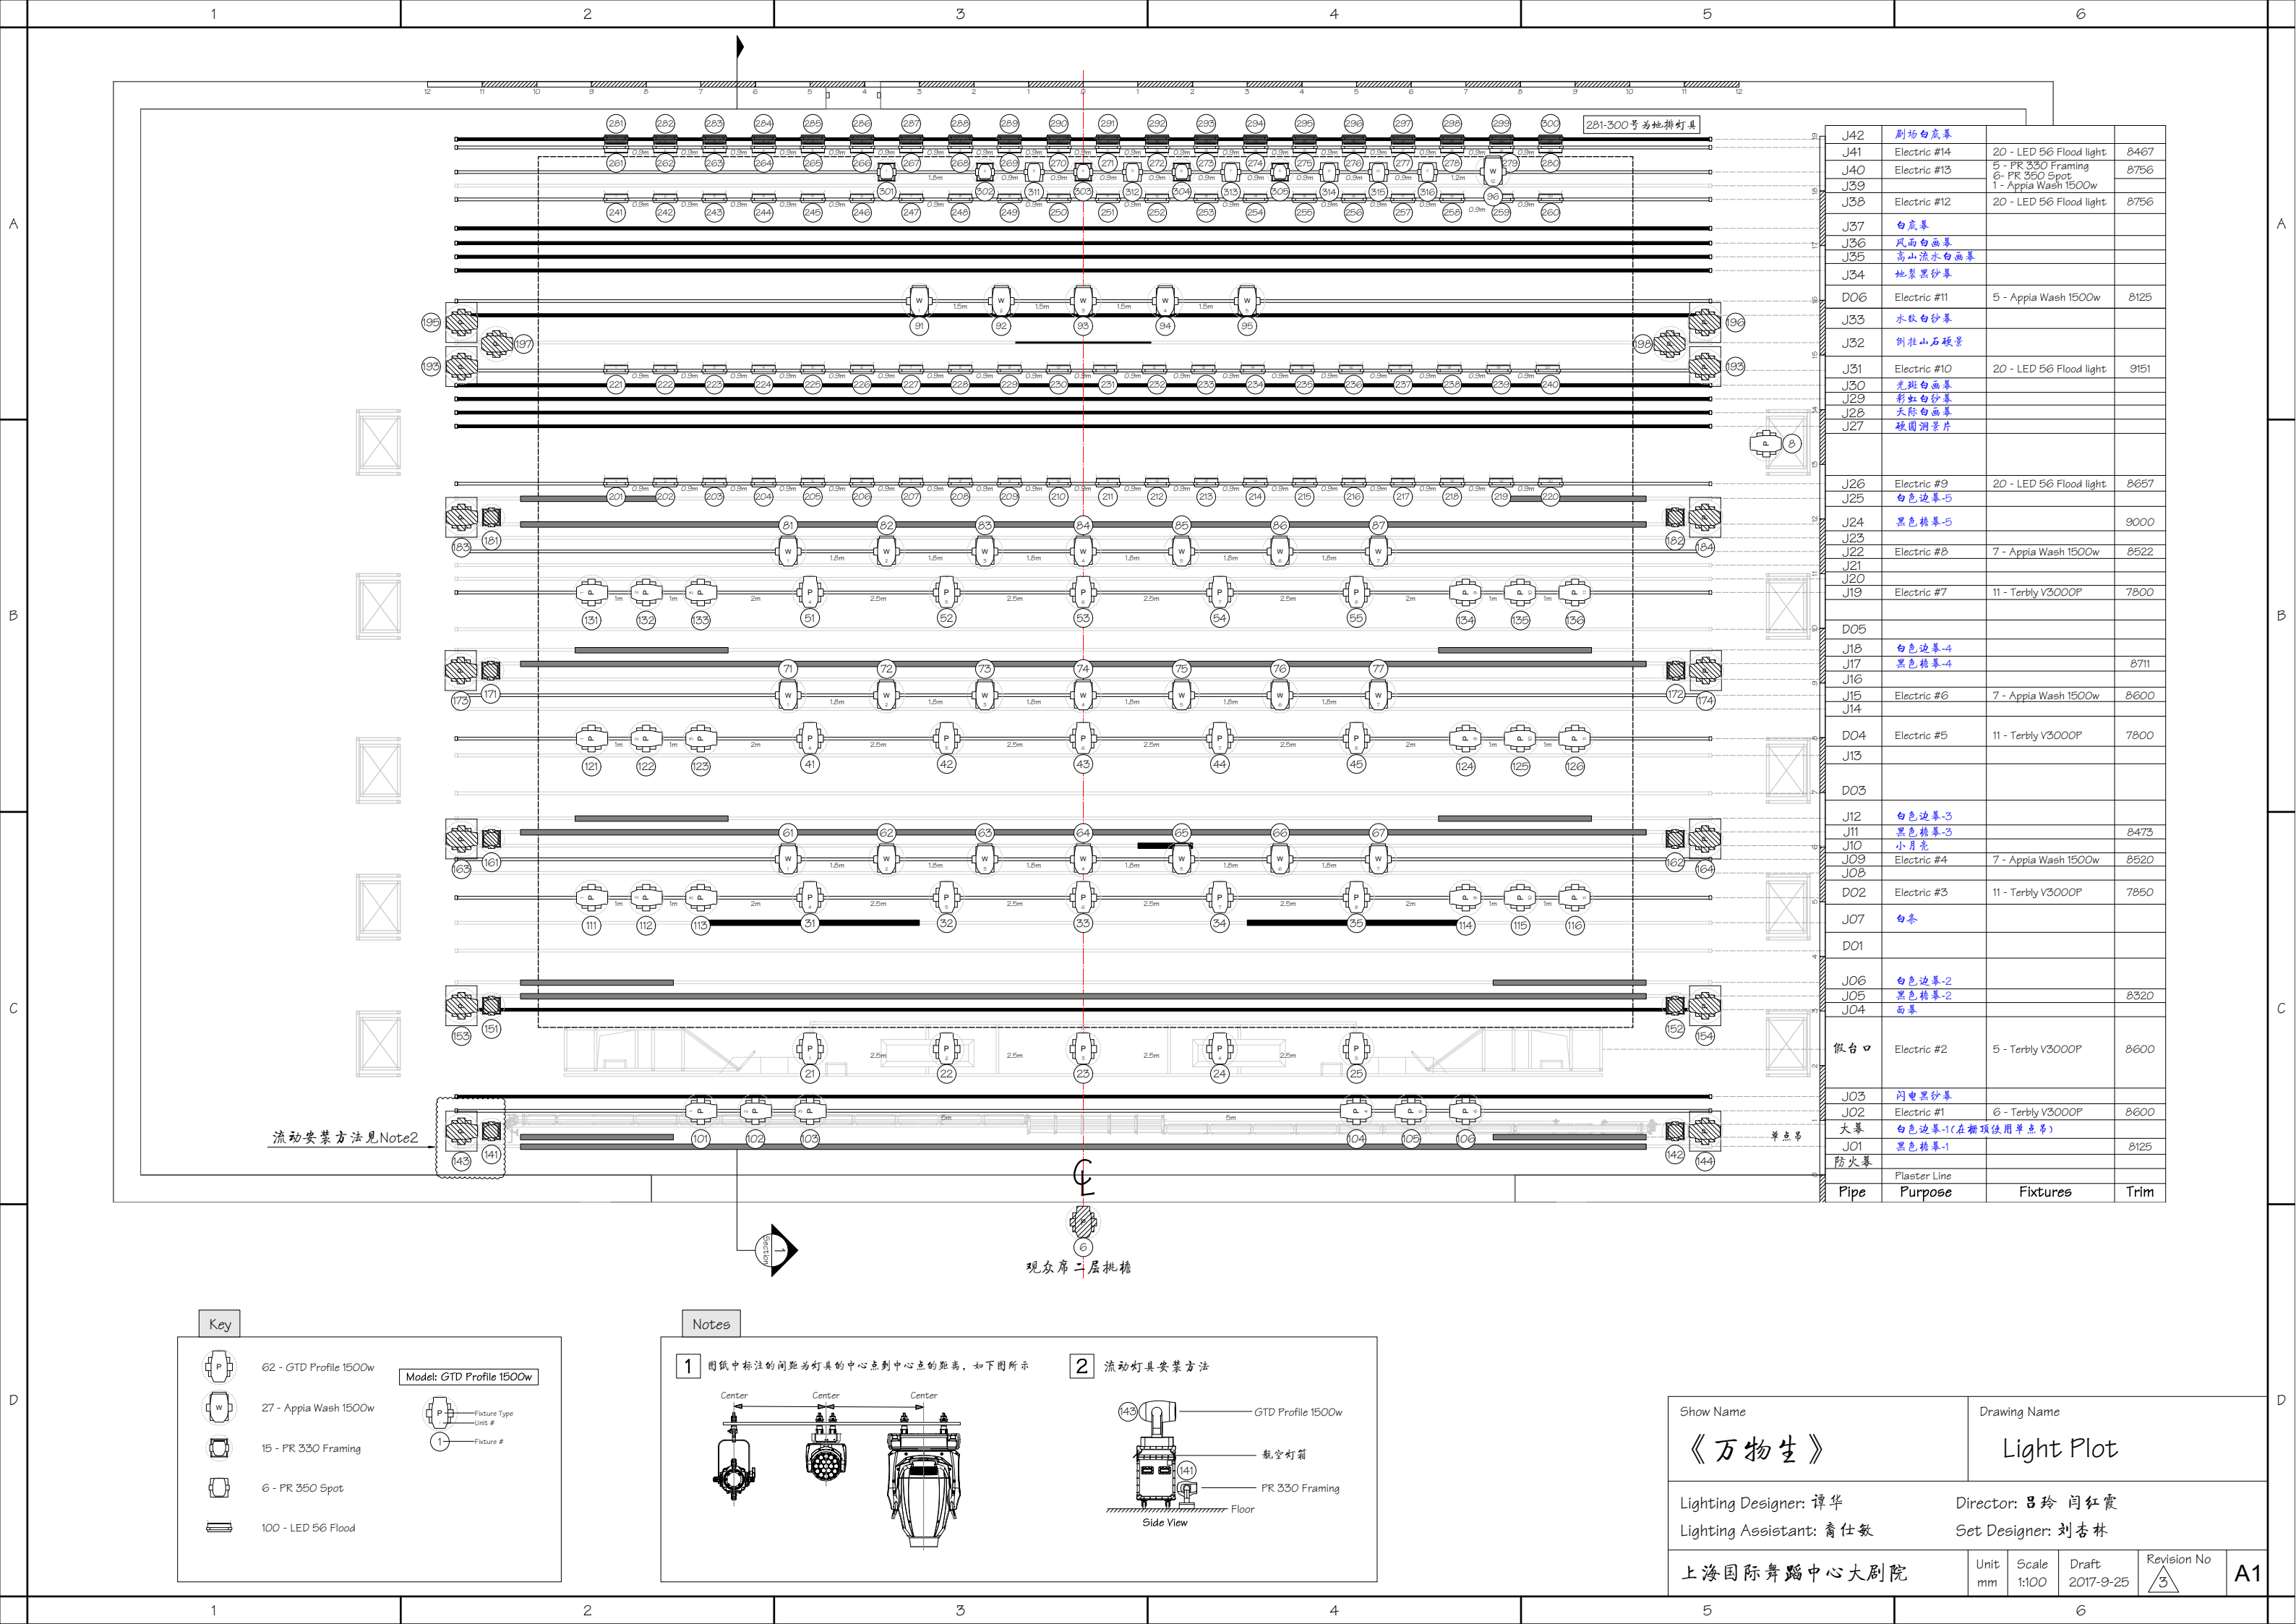


J42	剧场白底幕		
J41	Electric #14	20 - LED 56 Flood light	8467
J40	Electric #13	5 - PR 330 Framing	8756
J39		6 - PR 350 Spot	
J38	Electric #12	1 - Appia Wash 1500w	
J37	白底幕	20 - LED 56 Flood light	8756
J36	风雨白画幕		
J35	高山流水白画幕		
J34	地景黑纱幕		
D06	Electric #11	5 - Appia Wash 1500w	8125
J33	水纹白纱幕		
J32	侧挂山石硬景		
J31	Electric #10	20 - LED 56 Flood light	9151
J30	光斑白画幕		
J29	彩虹白纱幕		
J28	天际白画幕		
J27	硬圆洞景片		
J26	Electric #9	20 - LED 56 Flood light	8657
J25	白色边幕-5		
J24	黑色糖幕-5		9000
J23			
J22	Electric #8	7 - Appia Wash 1500w	8522
J21			
J20			
J19	Electric #7	11 - Terby V3000P	7800
D05			
J18	白色边幕-4		
J17	黑色糖幕-4		8711
J16			
J15	Electric #6	7 - Appia Wash 1500w	8600
J14			
D04	Electric #5	11 - Terby V3000P	7800
J13			
D03			
J12	白色边幕-3		
J11	黑色糖幕-3		8473
J10	小月亮		
J09	Electric #4	7 - Appia Wash 1500w	8520
J08			
D02	Electric #3	11 - Terby V3000P	7850
J07	白条		
D01			
J06	白色边幕-2		
J05	黑色糖幕-2		8320
J04	面幕		
假台口	Electric #2	5 - Terby V3000P	8600
J03	闪电黑纱幕		
J02	Electric #1	6 - Terby V3000P	8600
大幕	白色边幕-1(在棚顶使用单点吊)		
J01	黑色糖幕-1		8125
防火幕			
Pipe	Plaster Line		
	Purpose	Fixtures	Trim

Key	
	62 - GTD Profile 1500w
	27 - Appia Wash 1500w
	15 - PR 330 Framing
	6 - PR 350 Spot
	100 - LED 56 Flood
Model: GTD Profile 1500w	
	Fixture Type
	Unit #
	Fixture #


Notes	
1	图纸中标注的间距为灯具的中心点到中心点的距离, 如下图所示
2	流动灯具安装方法

Show Name		Drawing Name	
《万物生》		Light Plot	
Lighting Designer: 谭华		Director: 吕玲 闫红霞	
Lighting Assistant: 裔仕数		Set Designer: 刘杏林	
上海国际舞蹈中心大剧院		Unit mm	Scale 1:100
		Draft 2017-9-25	Revision No 3
		A1	

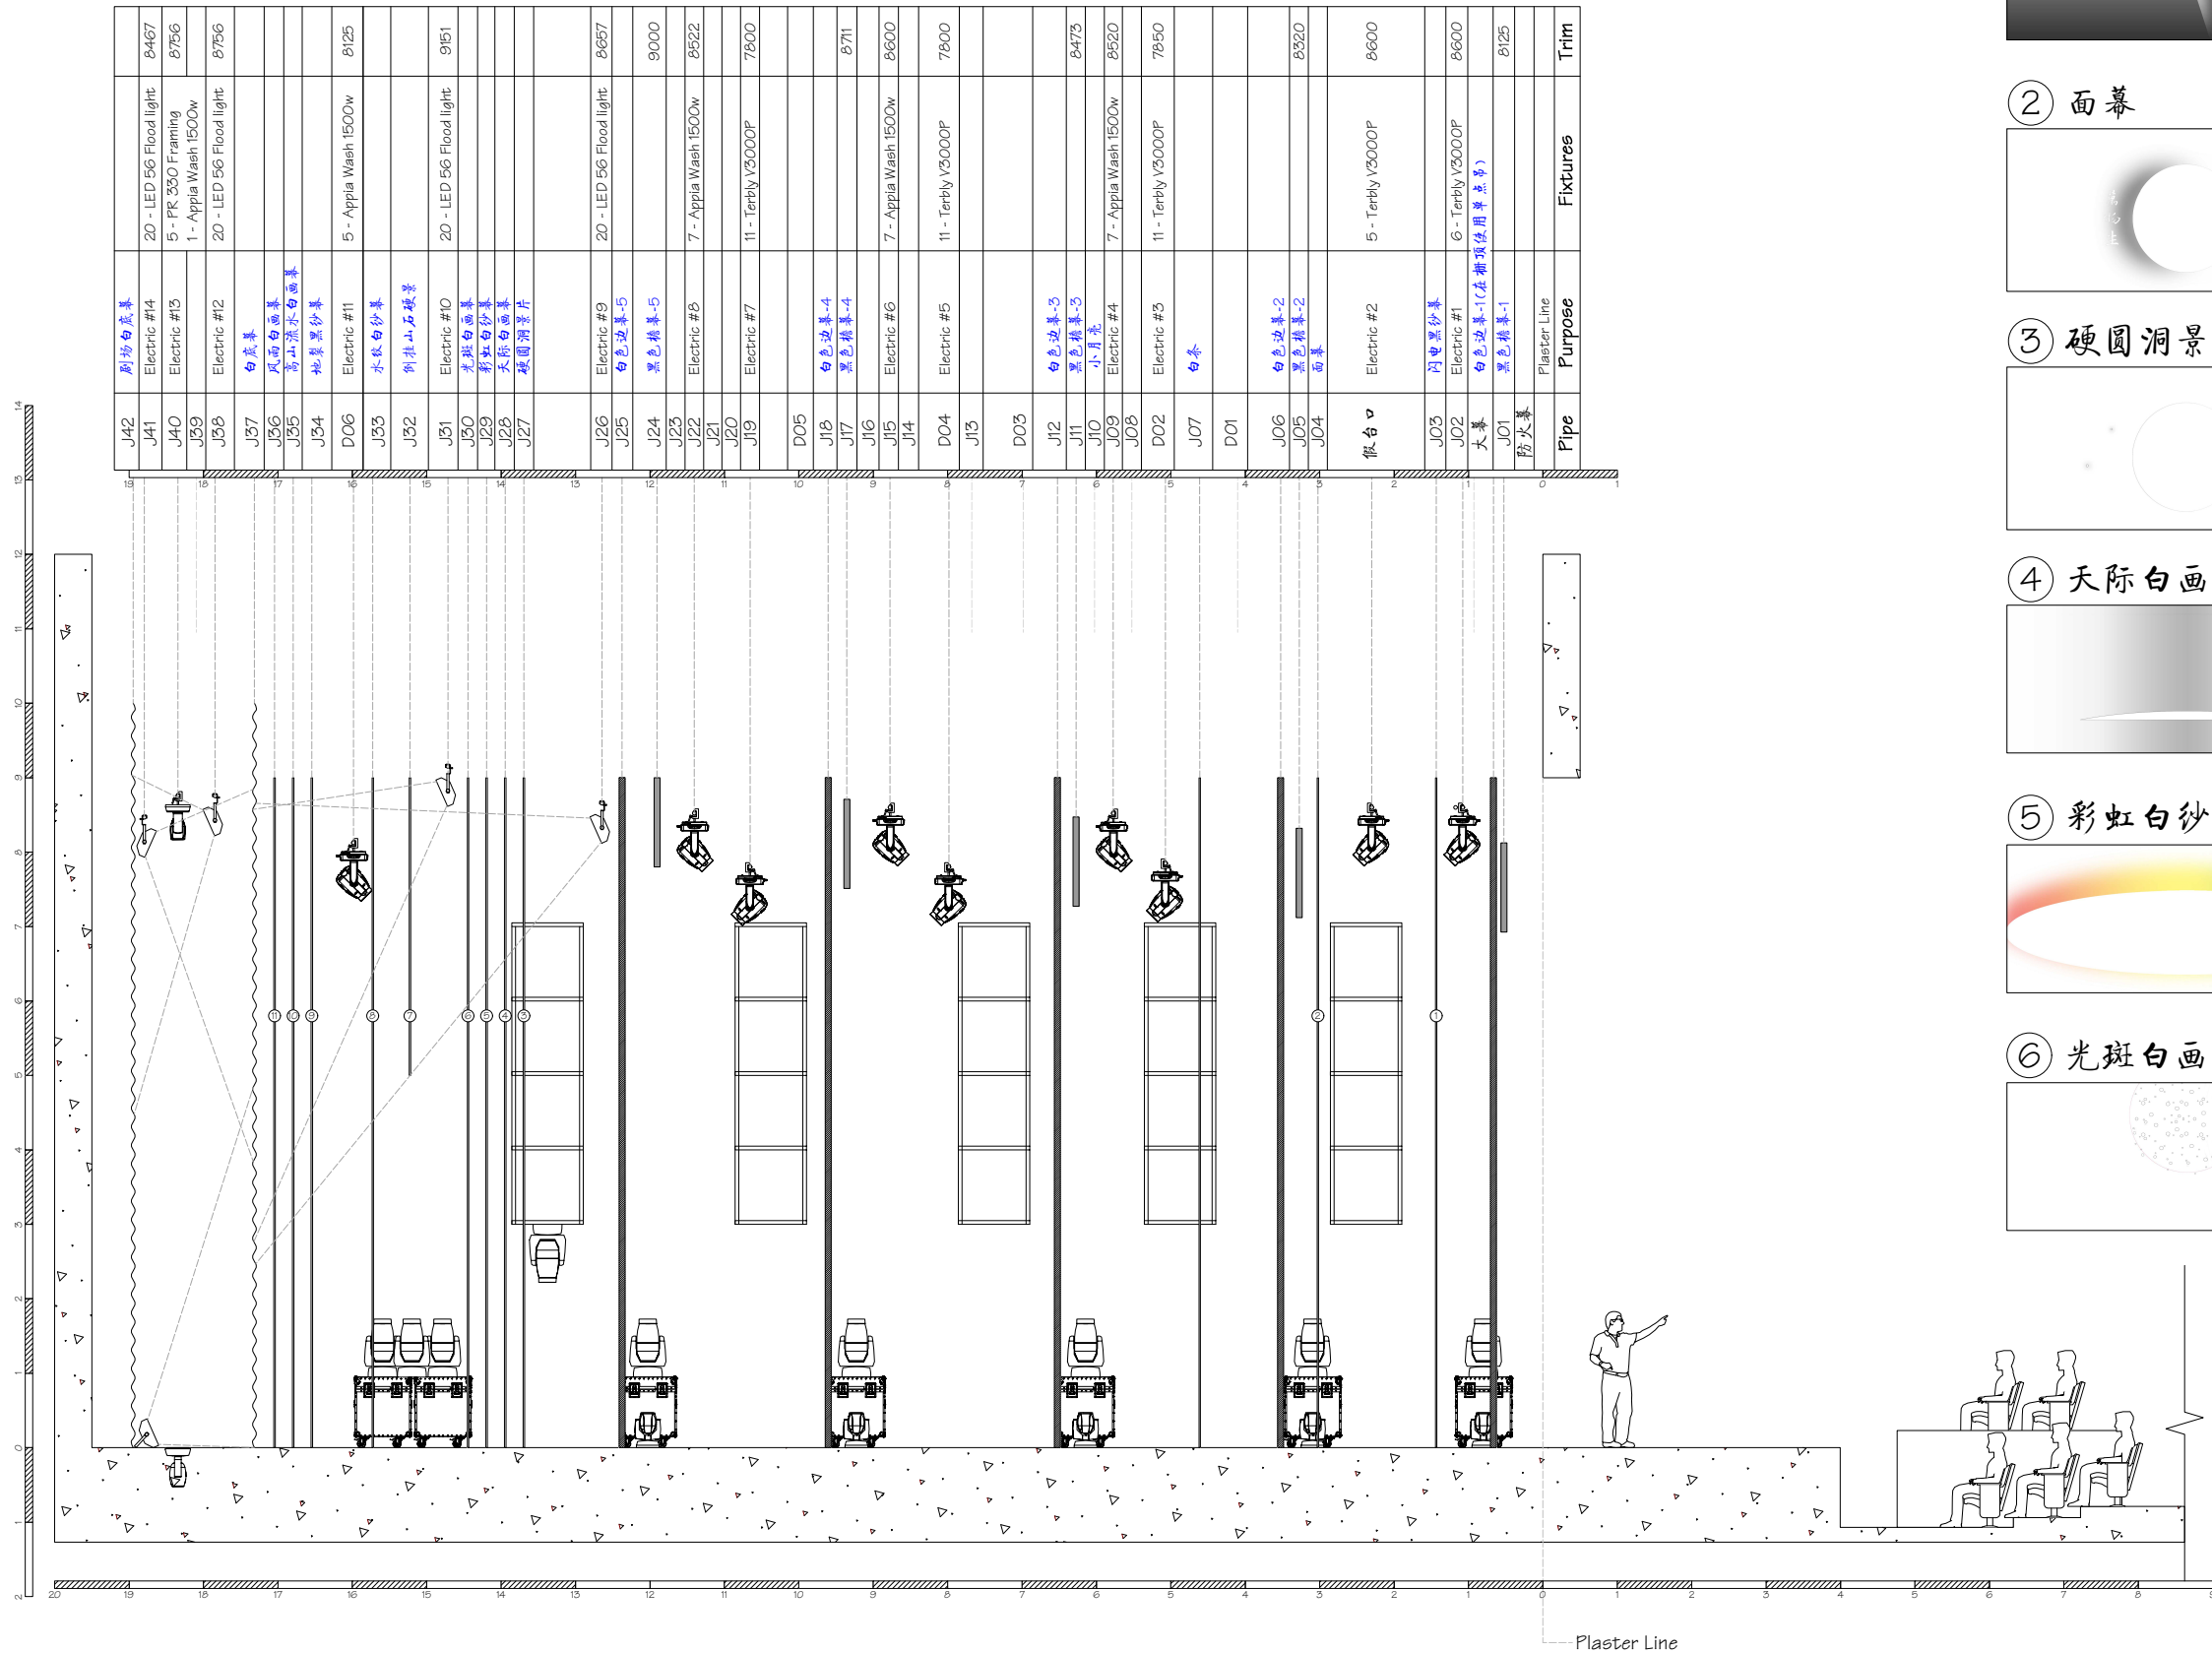


1 Section
1:100


① 闪电黑纱幕

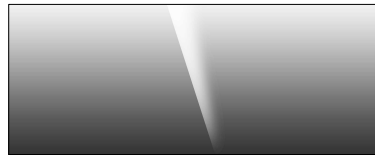


② 面幕

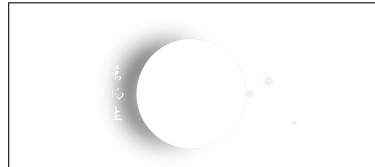


③ 硬圆洞景片

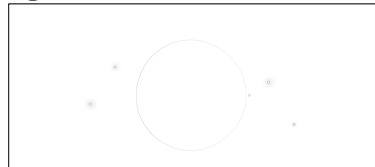


④ 天际白画幕

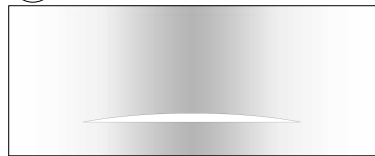

⑤ 彩虹白沙幕

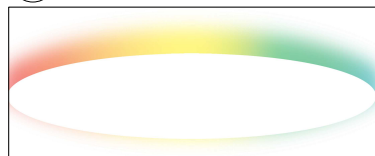


⑥ 光斑白画幕

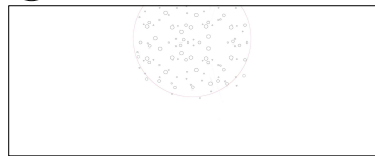


⑦ 倒挂山石硬景



⑧ 水纹白沙幕

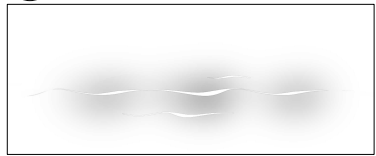


⑨ 地裂黑纱幕

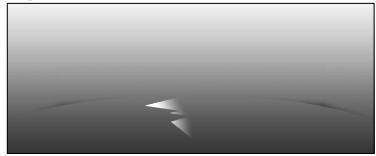

⑩ 高山流水白画幕



⑪ 风雨白画幕

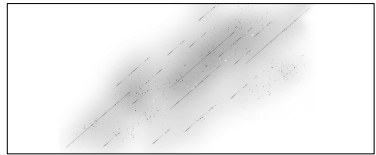

Show Name 《万物生》		Drawing Name Section	
Lighting Designer: 谭华 Lighting Assistant: 商仕敏		Director: 吕玲 闫红霞 Set Designer: 刘杏林	
上海国际舞蹈中心大剧院		Unit mm	Scale 1:100
		Draft 2017-9-25	Revision No 3
		A1	