

GENERAL NOTES 通用说明

1. THIS PLAN IS BASED ON A 50% DESIGN AND WILL BE ADJUSTED LATER ACCORDING TO THE LIGHTING DESIGN PLAN.
1.此方案基于50%设计方案，后期会根据灯光设计方案而调整。


2. THE NUMBER OF SERVER RACKS IS UNDETERMINED AND WILL BE DETERMINED BASED ON POWER CONSUMPTION AND THE NUMBER OF LIGHTS AFTER THE LIGHTING DESIGN IS COMPLETED.
2.机柜的数量未定，需等灯光设计完成后根据用电量和灯具数量而决定。

3. THE SPECIFIC LOCATION OF THE SERVER ROOM WILL BE DETERMINED AFTER ALLOCATION BY THE OWNER.
3.机房的具体位置待业主主分配后决定。

4. DETAILS OF THE INTERNAL RACKS AND WIRING WILL BE PROVIDED IN SUBSEQUENT DETAILED DRAWINGS.
4.机柜内部细节和连线参考后续深化图。

5. CABLES CONNECTING TO THE LIGHTING TIMECODE CONTROLLER WILL BE PROVIDED BY ANOTHER CONTRACTOR.
5.接入灯光时间码控制器的线缆由其他承包商提供。

6. SINCE THE EXTERIOR LIGHTING WAS DESIGNED BY ANOTHER COMPANY, THE CONNECTION PLAN IS YET TO BE DETERMINED.
6.由于外立面灯光由其他公司设计，接入方案待定。

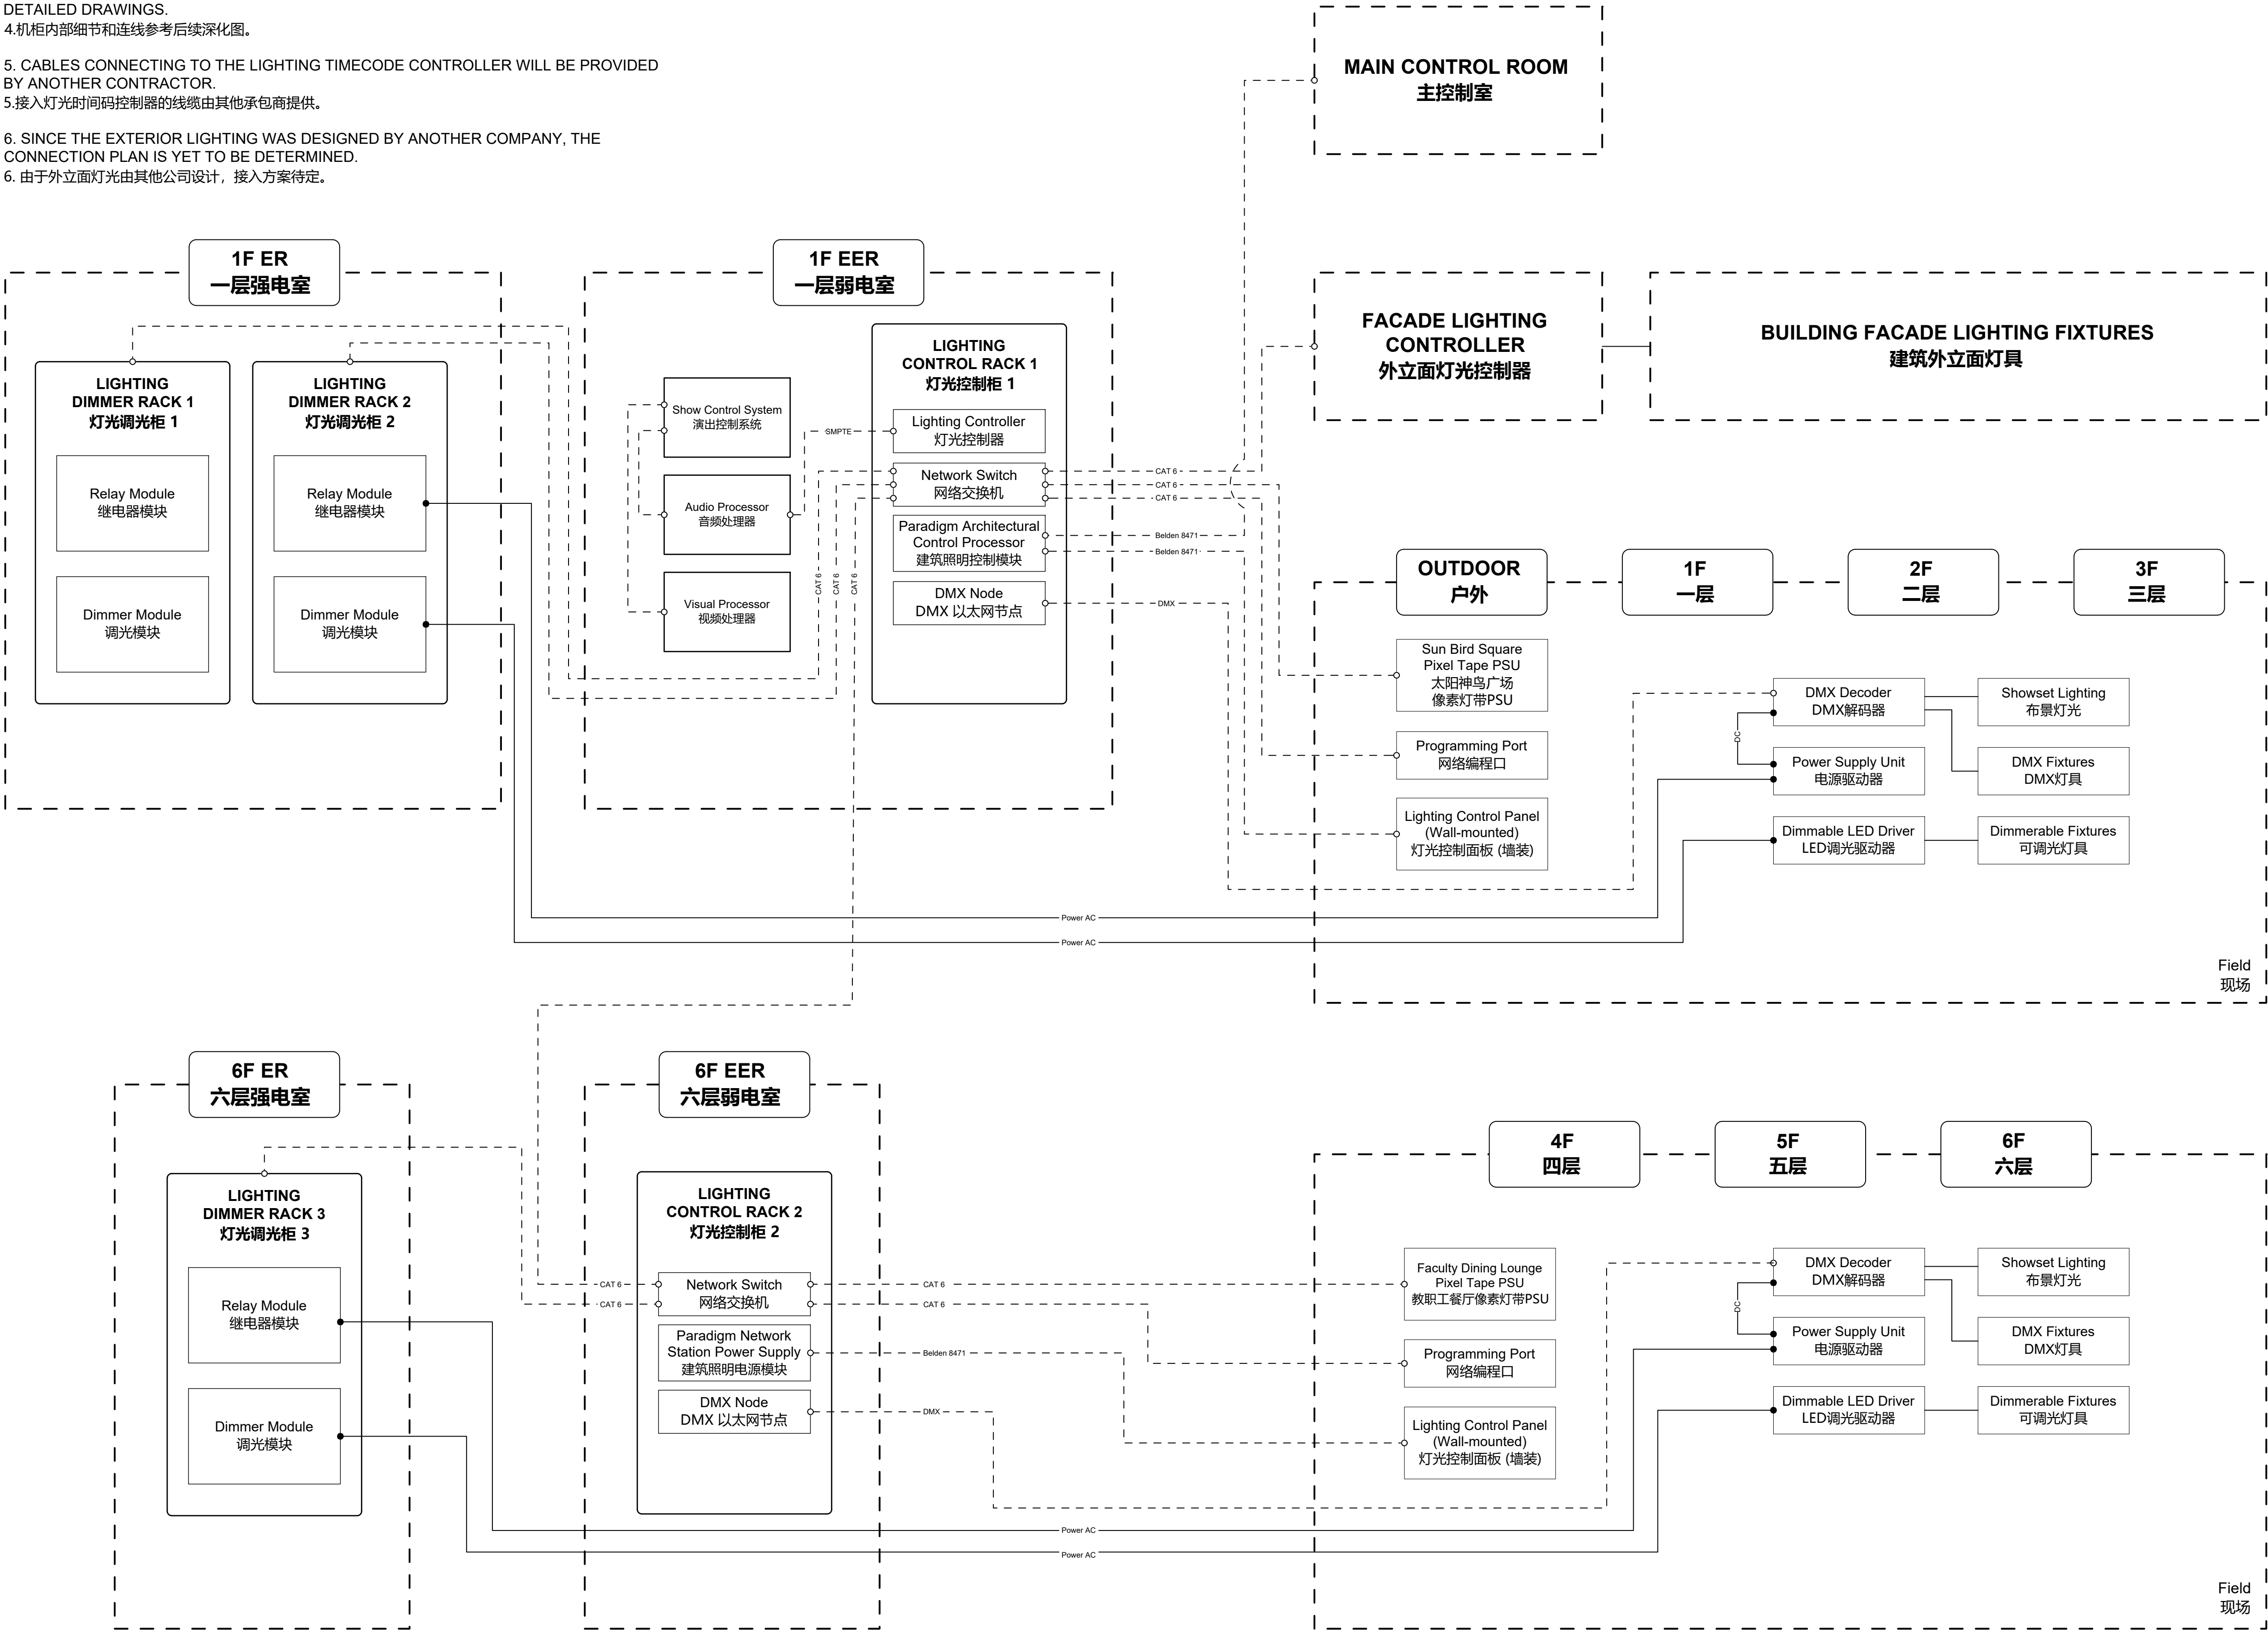

腾讯
Tencent

TAIT

481 WEST LINCOLN AVENUE
LITITZ, PENNSYLVANIA 17543 USA
T: +1 (717) 626-6671 - TAITTOWERS.COM

THIS DOCUMENT CONTAINS INFORMATION THAT IS
CONFIDENTIAL AND PROPRIETARY. ANY
UNAUTHORIZED USE, DISCLOSURE,
DISSEMINATION OR DUPLICATION IS STRICTLY
PROHIBITED.
本文件包含机密及专有信息，严禁任何未经授权的使用、
披露、传播或复制。

©2025 TAIT TOWERS, INC.
ALL RIGHTS RESERVED
版权所有

TAIT TOWERS (TAIT) IS NOT AN ARCHITECTURAL
OR ENGINEERING FIRM. THESE DRAWINGS
REPRESENT DESIGN INTENT FOR ARTISTIC
DIRECTION ONLY. THEY SHOULD NOT BE USED
FOR ANY OTHER PURPOSE, INCLUDING, BUT NOT
LIMITED TO, CONSTRUCTION, FABRICATION,
INSTALLATION, OR SITE ANALYSIS.
TAIT TOWERS (TAIT) 并非建筑或工程公司，这些图纸仅
代表艺术意图的设计意图，不得用于任何其他用途，包括但
不限于施工、制造、安装或现场分析。

TAIT ASSUMES NO RESPONSIBILITY FOR MISUSE,
OR ERRORS, OR OMISSIONS
TAIT 对任何误用、错误或遗漏概不负责。

CHENGDU HONOR OF KINGS
EXPERIENCE HALL PROJECT
成都王者荣耀体验馆项目

NOT FOR CONSTRUCTION
非施工用途

PROJECT STAGE 项目阶段:
SCHEMATIC DESIGN
方案设计

D ISSUANCES & REVISIONS 发布和修订:

#	DATE 日期	DESCRIPTION 说明
01	2026-03-22	50% SCHEMATIC DESIGN INTERIM SUBMISSION 50% 方案设计中期提交



THIS DOCUMENT CONTAINS INFORMATION THAT IS
CONFIDENTIAL AND PROPRIETARY. ANY
UNAUTHORIZED USE, DISCLOSURE,
DISSEMINATION OR DUPLICATION IS STRICTLY
PROHIBITED.
本文件包含机密及专有信息。严禁任何未经授权的使用、
披露、传播或复制。

TAJT TOWERS (TAJT) IS NOT AN ARCHITECTURAL OR ENGINEERING FIRM. THESE DRAWINGS REPRESENT DESIGN INTENT FOR ARTISTIC DIRECTION ONLY. THEY SHOULD NOT BE USED FOR ANY OTHER PURPOSE, INCLUDING, BUT NOT LIMITED TO, CONSTRUCTION, FABRICATION, INSTALLATION, OR SITE ANALYSIS.

CHENGDU HONOR OF KINGS
EXPERIENCE HALL PROJECT
成都王者荣耀体验馆项目

PROJECT STAGE 项目阶段:
SCHEMATIC DESIGN
方案设计

D ISSUANCES & REVISIONS 发布和修订:

#	DATE 日期	DESCRIPTION 说明
01	2026-03-22	50% SCHEMATIC DESIGN INTER SUBMISSION 50% 方案阶段设计图

PROJECT CODE 项目代码: HOKCHE

DRAWN BY 制图人:

DESIGN LEAD 设计负责人:

PLOT DATE 绘图日期

FILE NAME 文档名称

PROJECT SEGMENT 项目部分:

ZONE/SCENE 区域/场景:

DELIVERABLE ID 交付成果章节

SHEET TITLE 图纸标题

LIGHTING DIMMER
RACK DETAILS
灯光调光柜细节图

SHEET NUMBER 图纸编号:


LX-0000-002

1. DIMMER RACK ENCLOSURE IS 16 GA. FORMED STEEL. FINISHED IN A FINE-TEXTURED BLACK EPOXY PAINT.


-
- Technical drawing of the rear view of the device. The drawing shows a rectangular panel with a central circular fan (FAN) and two rectangular ventilation grilles on the right side. Dimensions are indicated by arrows and numbers: 22 (top left corner), 320 (top width), 28 (top right corner), 226 (left side height), 512 (total left side height), 70 (bottom left corner), and 70 (bottom right corner). The fan is labeled "FAN" and "排风扇" (Exhaust Fan).

Top View 俯视图

Cable inlet
(Top or bottom are both acceptable)
进线口 (顶部和底部都可)

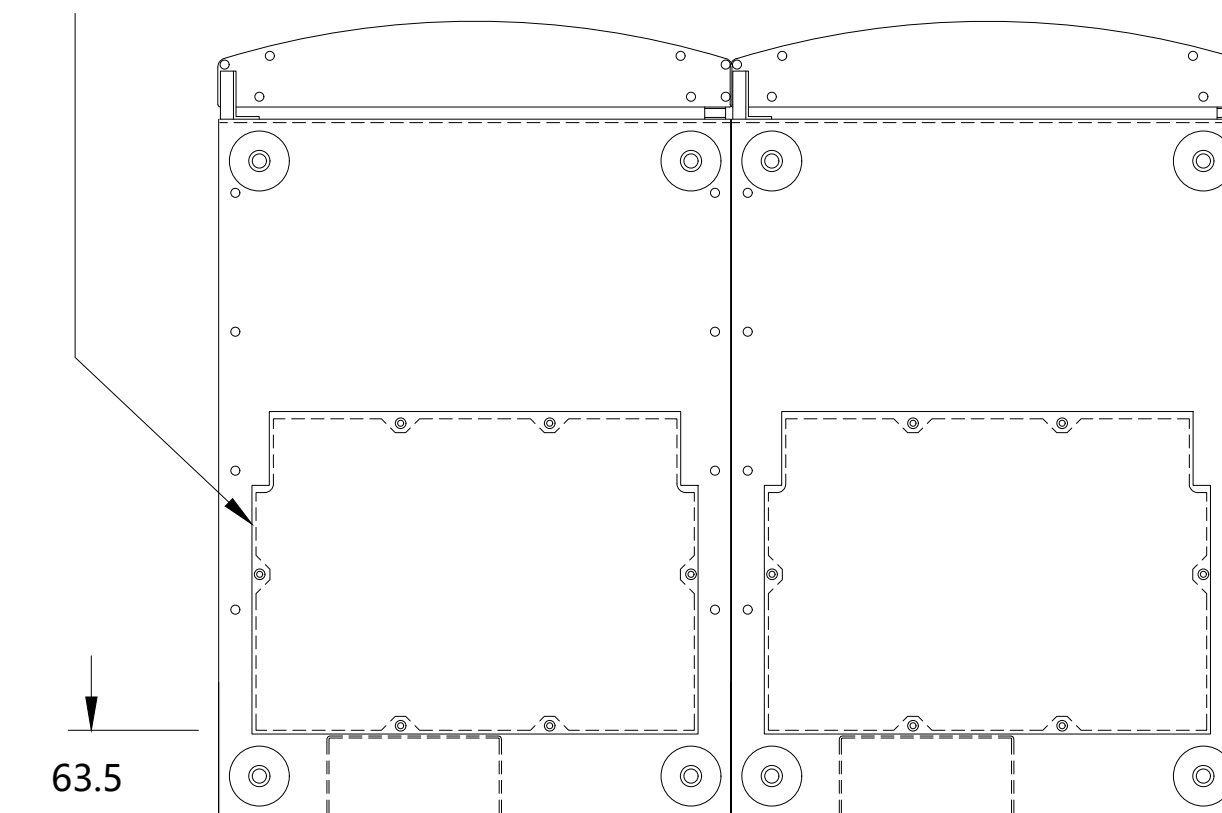


Bottom View 仰视图

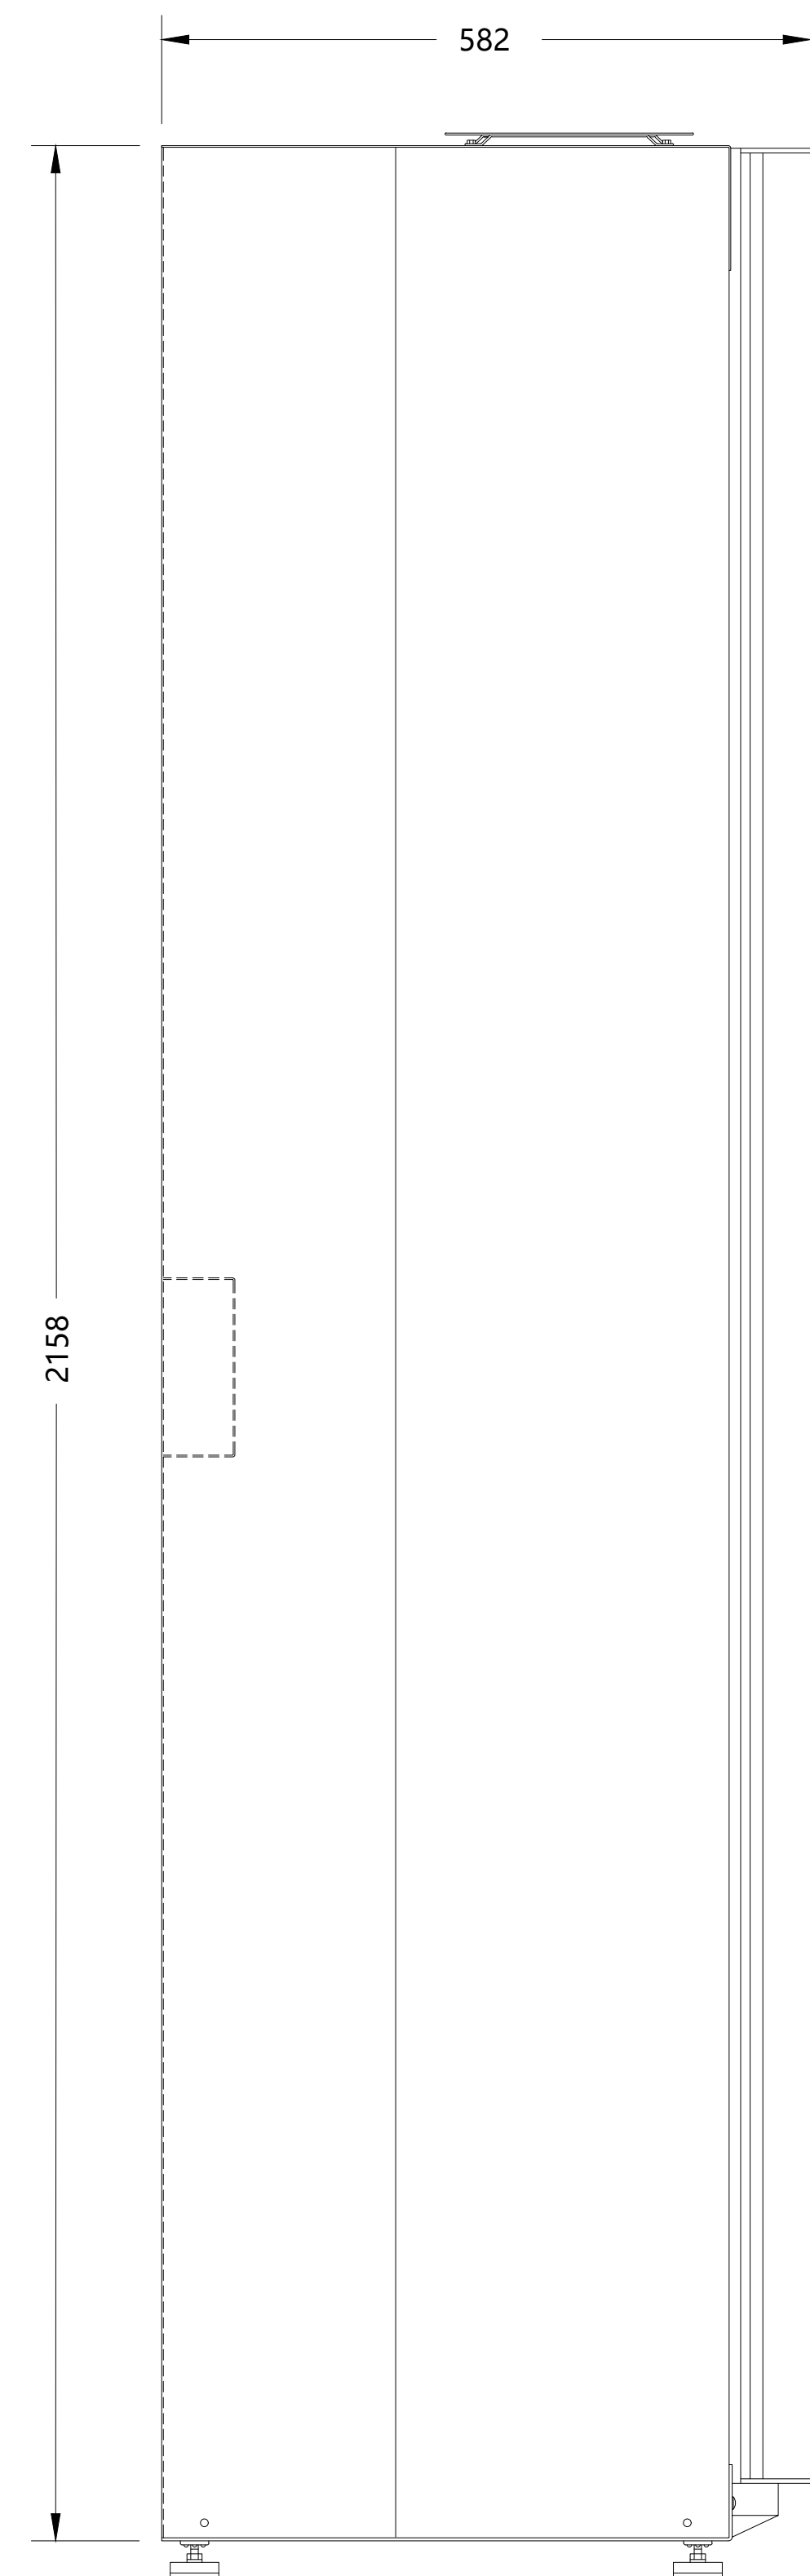


Side View 侧视图

1

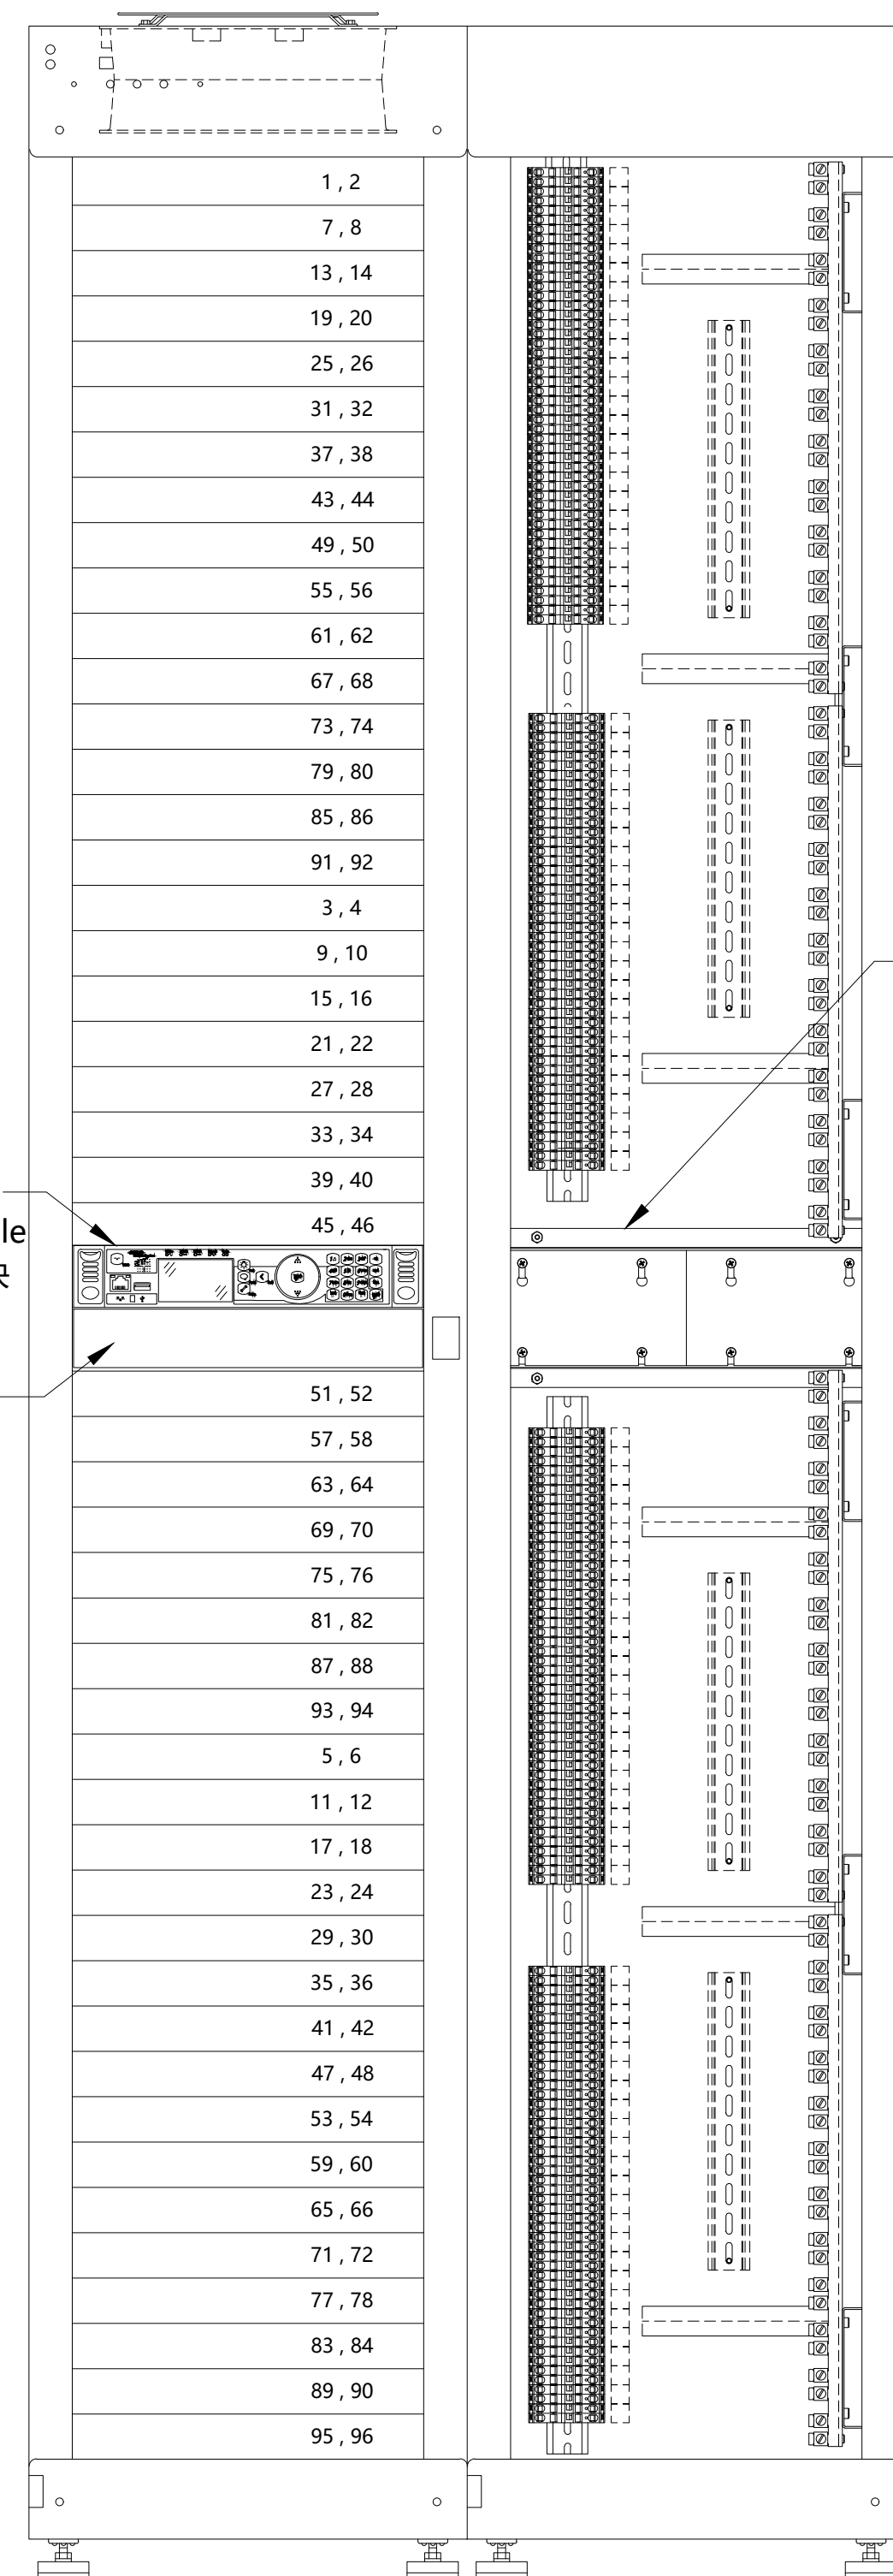

Front View 正视图

2

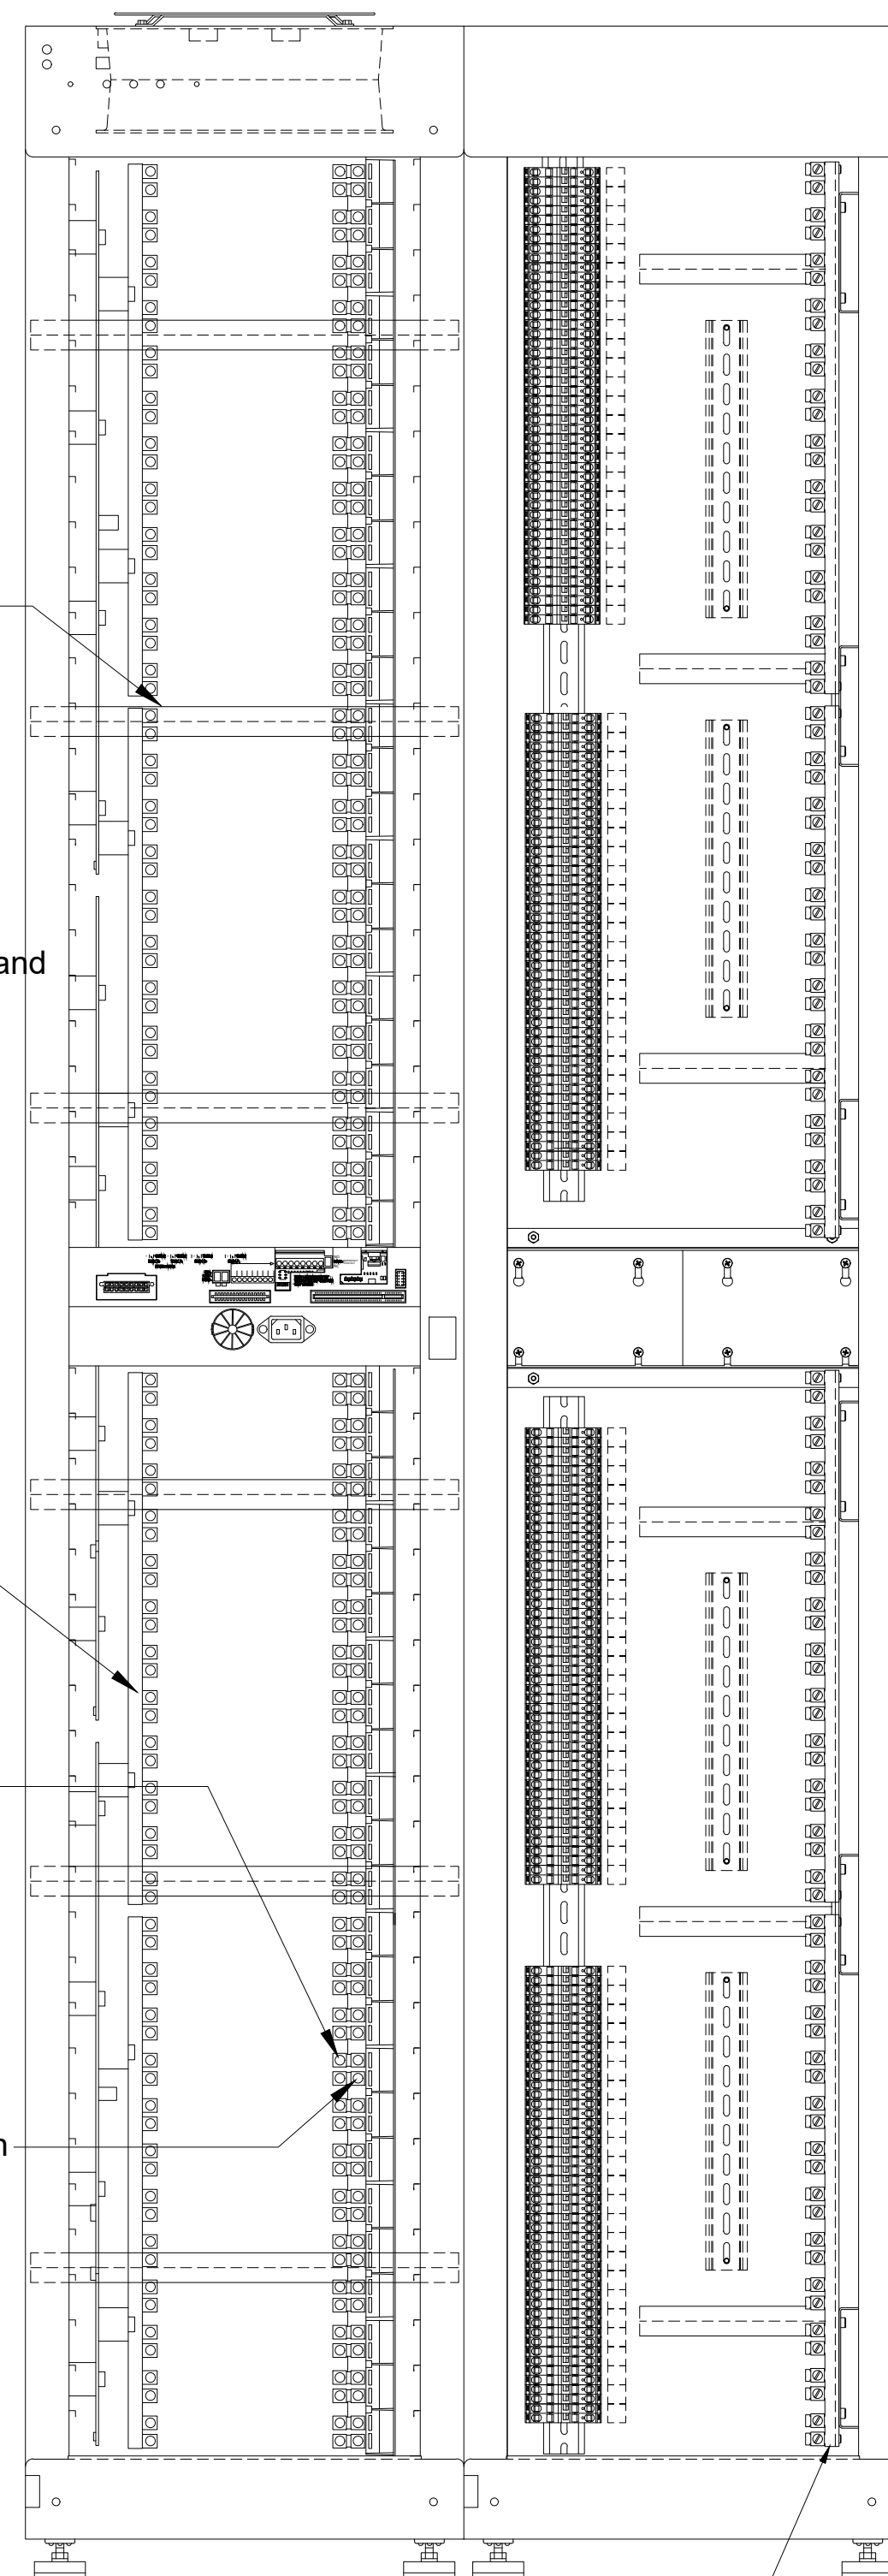

Front View (Module removal) 正视图 (模块移除)

Ground
接地排

