



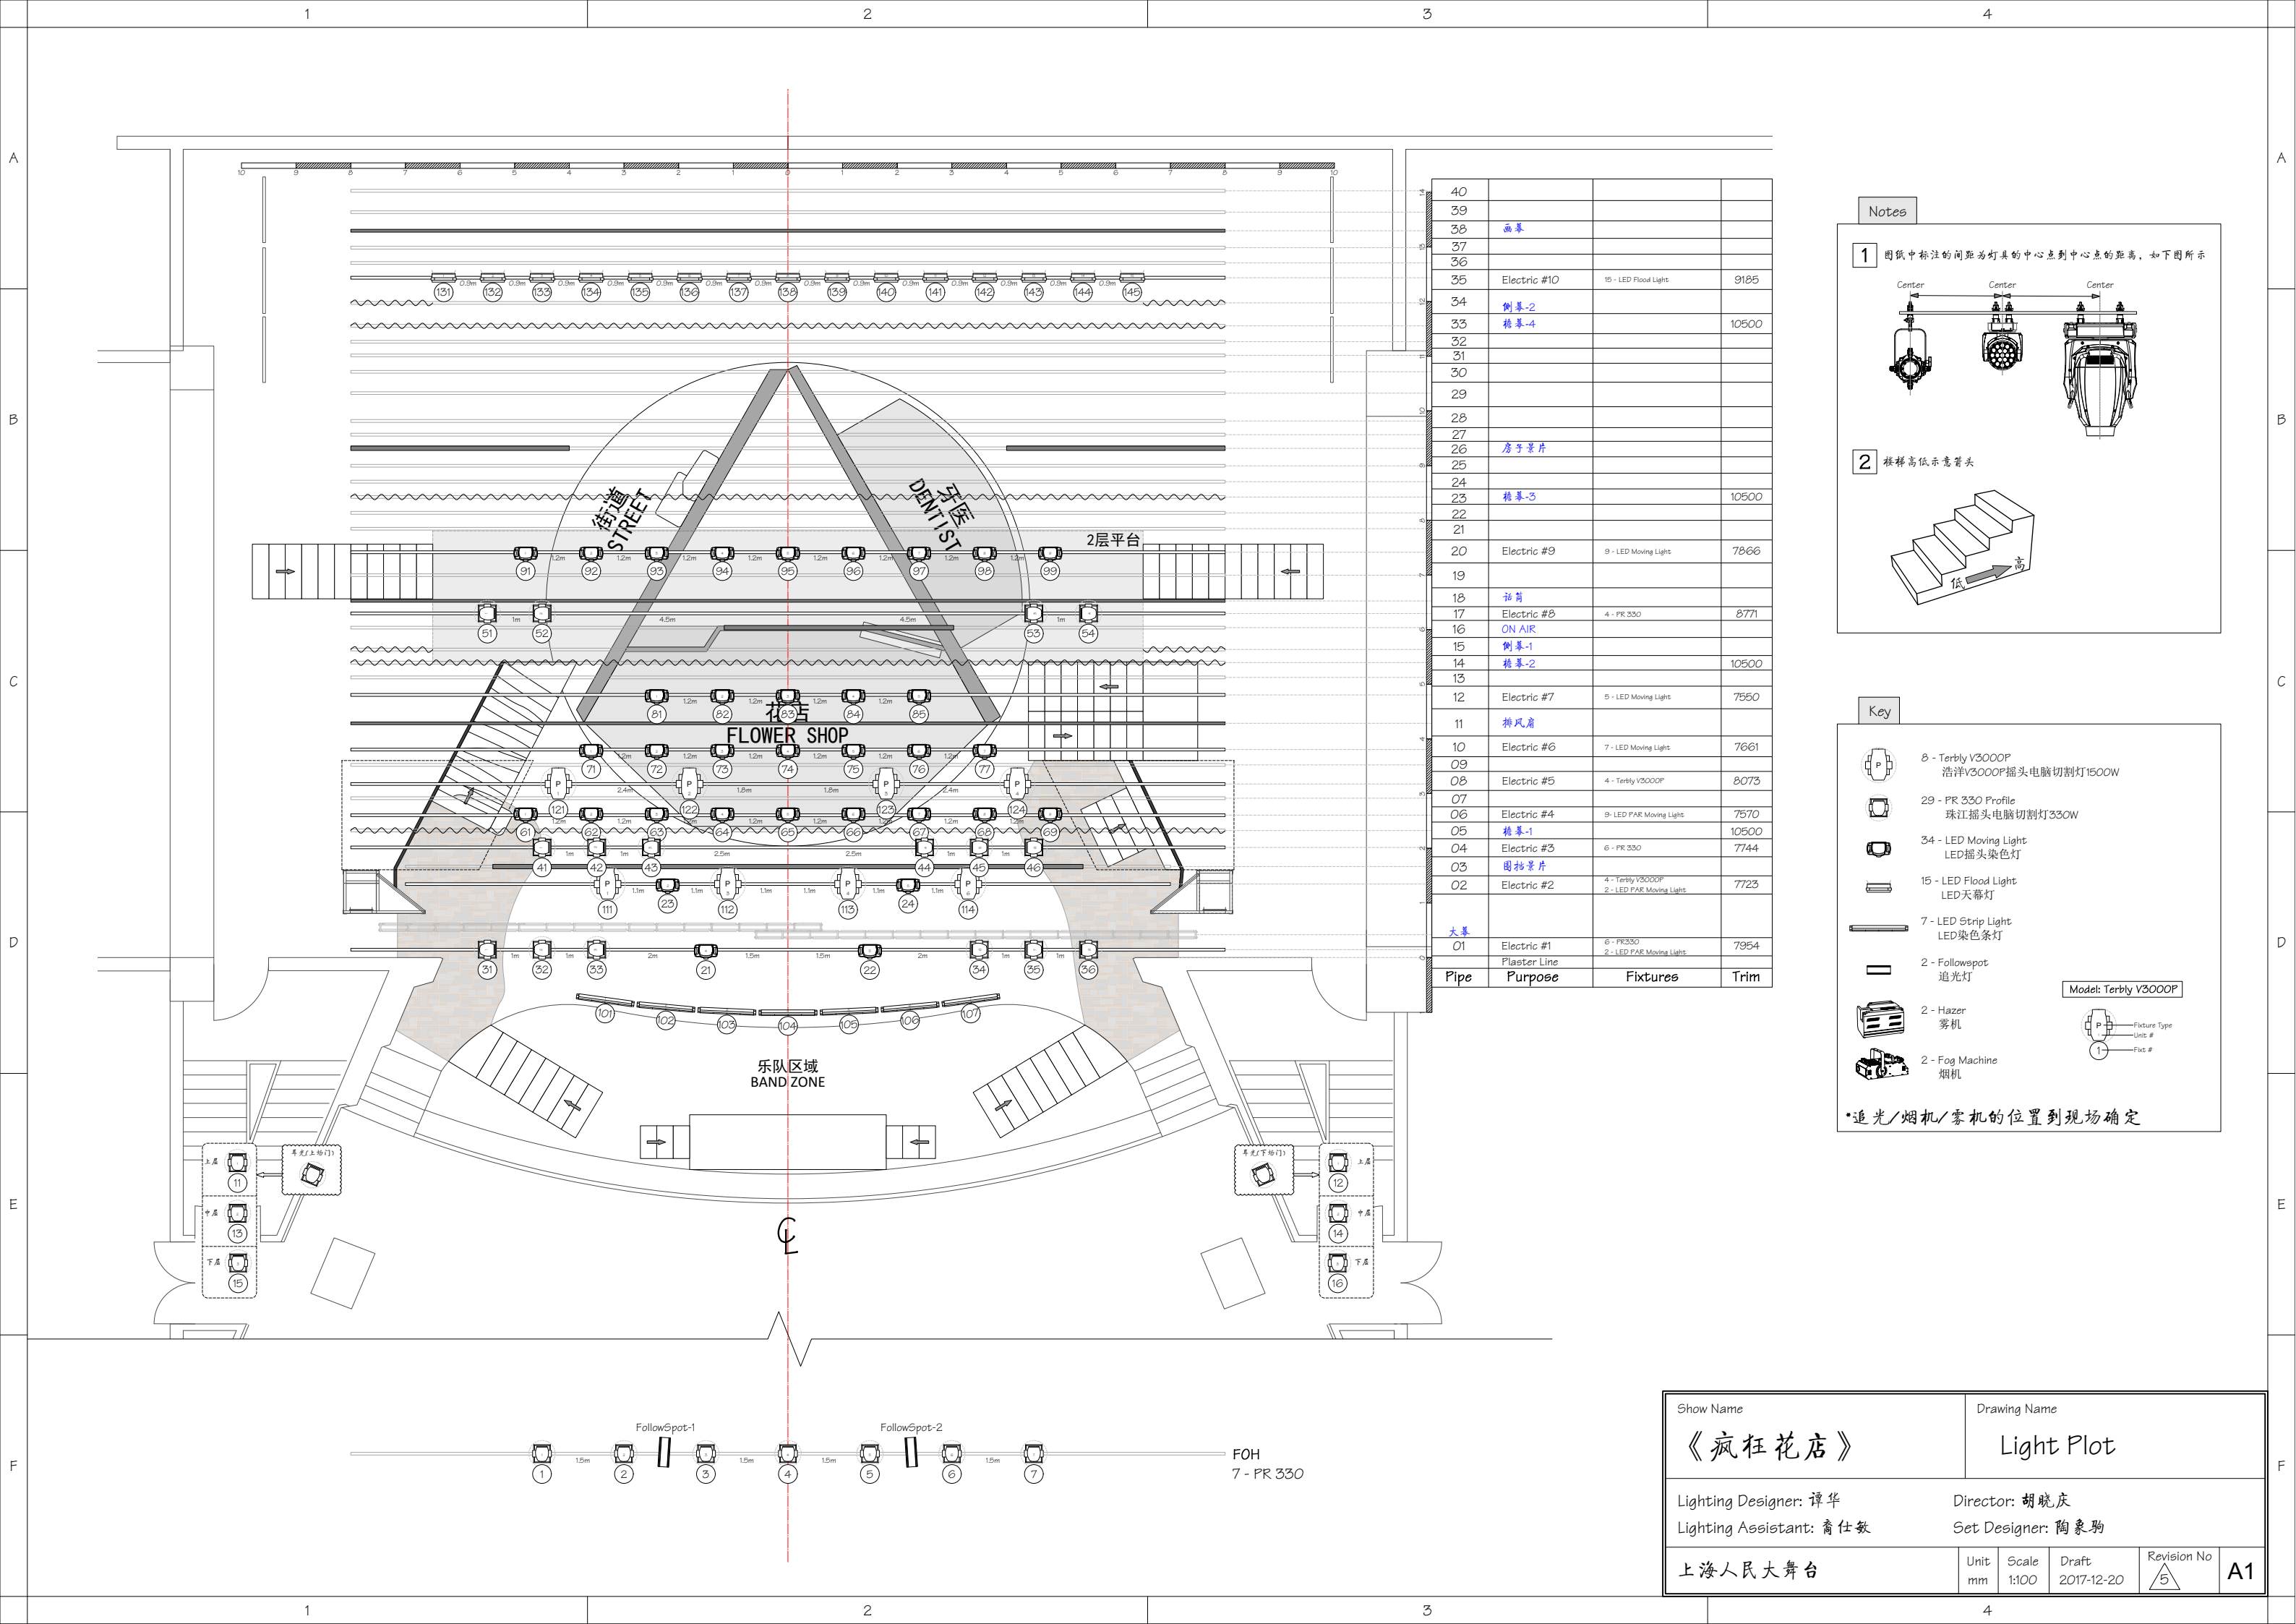


Notes

1 图纸中标注的间距为灯具的中心点到中心点的距离，如下图所示

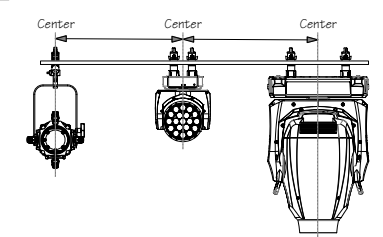

2 楼梯高低示意箭头

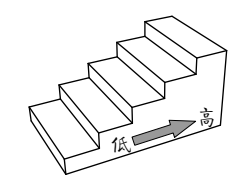

Key

- 8 - Terby V3000P 浩洋V3000P摇头电脑切割灯1500W
 - 29 - PR 330 Profile 珠江摇头电脑切割灯330W
 - 34 - LED Moving Light LED摇头染色灯
 - 15 - LED Flood Light LED天幕灯
 - 7 - LED Strip Light LED染色条灯
 - 2 - Followspot 追光灯
 - 2 - Hazer 雾机
 - 2 - Fog Machine 烟机
- Model: Terby V3000P
- Fixture Type
Unit #
Fixt #

*追光/烟机/雾机的位置到现场确定

40			
39			
38	画幕		
37			
36			
35	Electric #10	15 - LED Flood Light	9185
34	侧幕-2		
33	侧幕-4		10500
32			
31			
30			
29			
28			
27	房子景片		
26			
25			
24	侧幕-3		10500
23			
22			
21			
20	Electric #9	9 - LED Moving Light	7866
19			
18	帘幕		
17	Electric #8	4 - PR 330	8771
16	ON AIR		
15	侧幕-1		
14	侧幕-2		10500
13			
12	Electric #7	5 - LED Moving Light	7550
11	排风扇		
10	Electric #6	7 - LED Moving Light	7661
09			
08	Electric #5	4 - Terby V3000P	8073
07			
06	Electric #4	9 - LED PAR Moving Light	7570
05	侧幕-1		10500
04	Electric #3	6 - PR 330	7744
03	侧幕-2		
02	Electric #2	4 - Terby V3000P 2 - LED PAR Moving Light	7723
01	Electric #1	6 - PR 330 2 - LED PAR Moving Light	7954
Pipe	Purpose	Fixtures	Trim

Show Name
《疯狂花店》

Drawing Name
Light Plot

Lighting Designer: 谭华
Lighting Assistant: 裔仕敏

Director: 胡晓庆
Set Designer: 陶象驹

上海人民大舞台


Unit
mm

Scale
1:100


Draft
2017-12-20

Revision No
5

A1

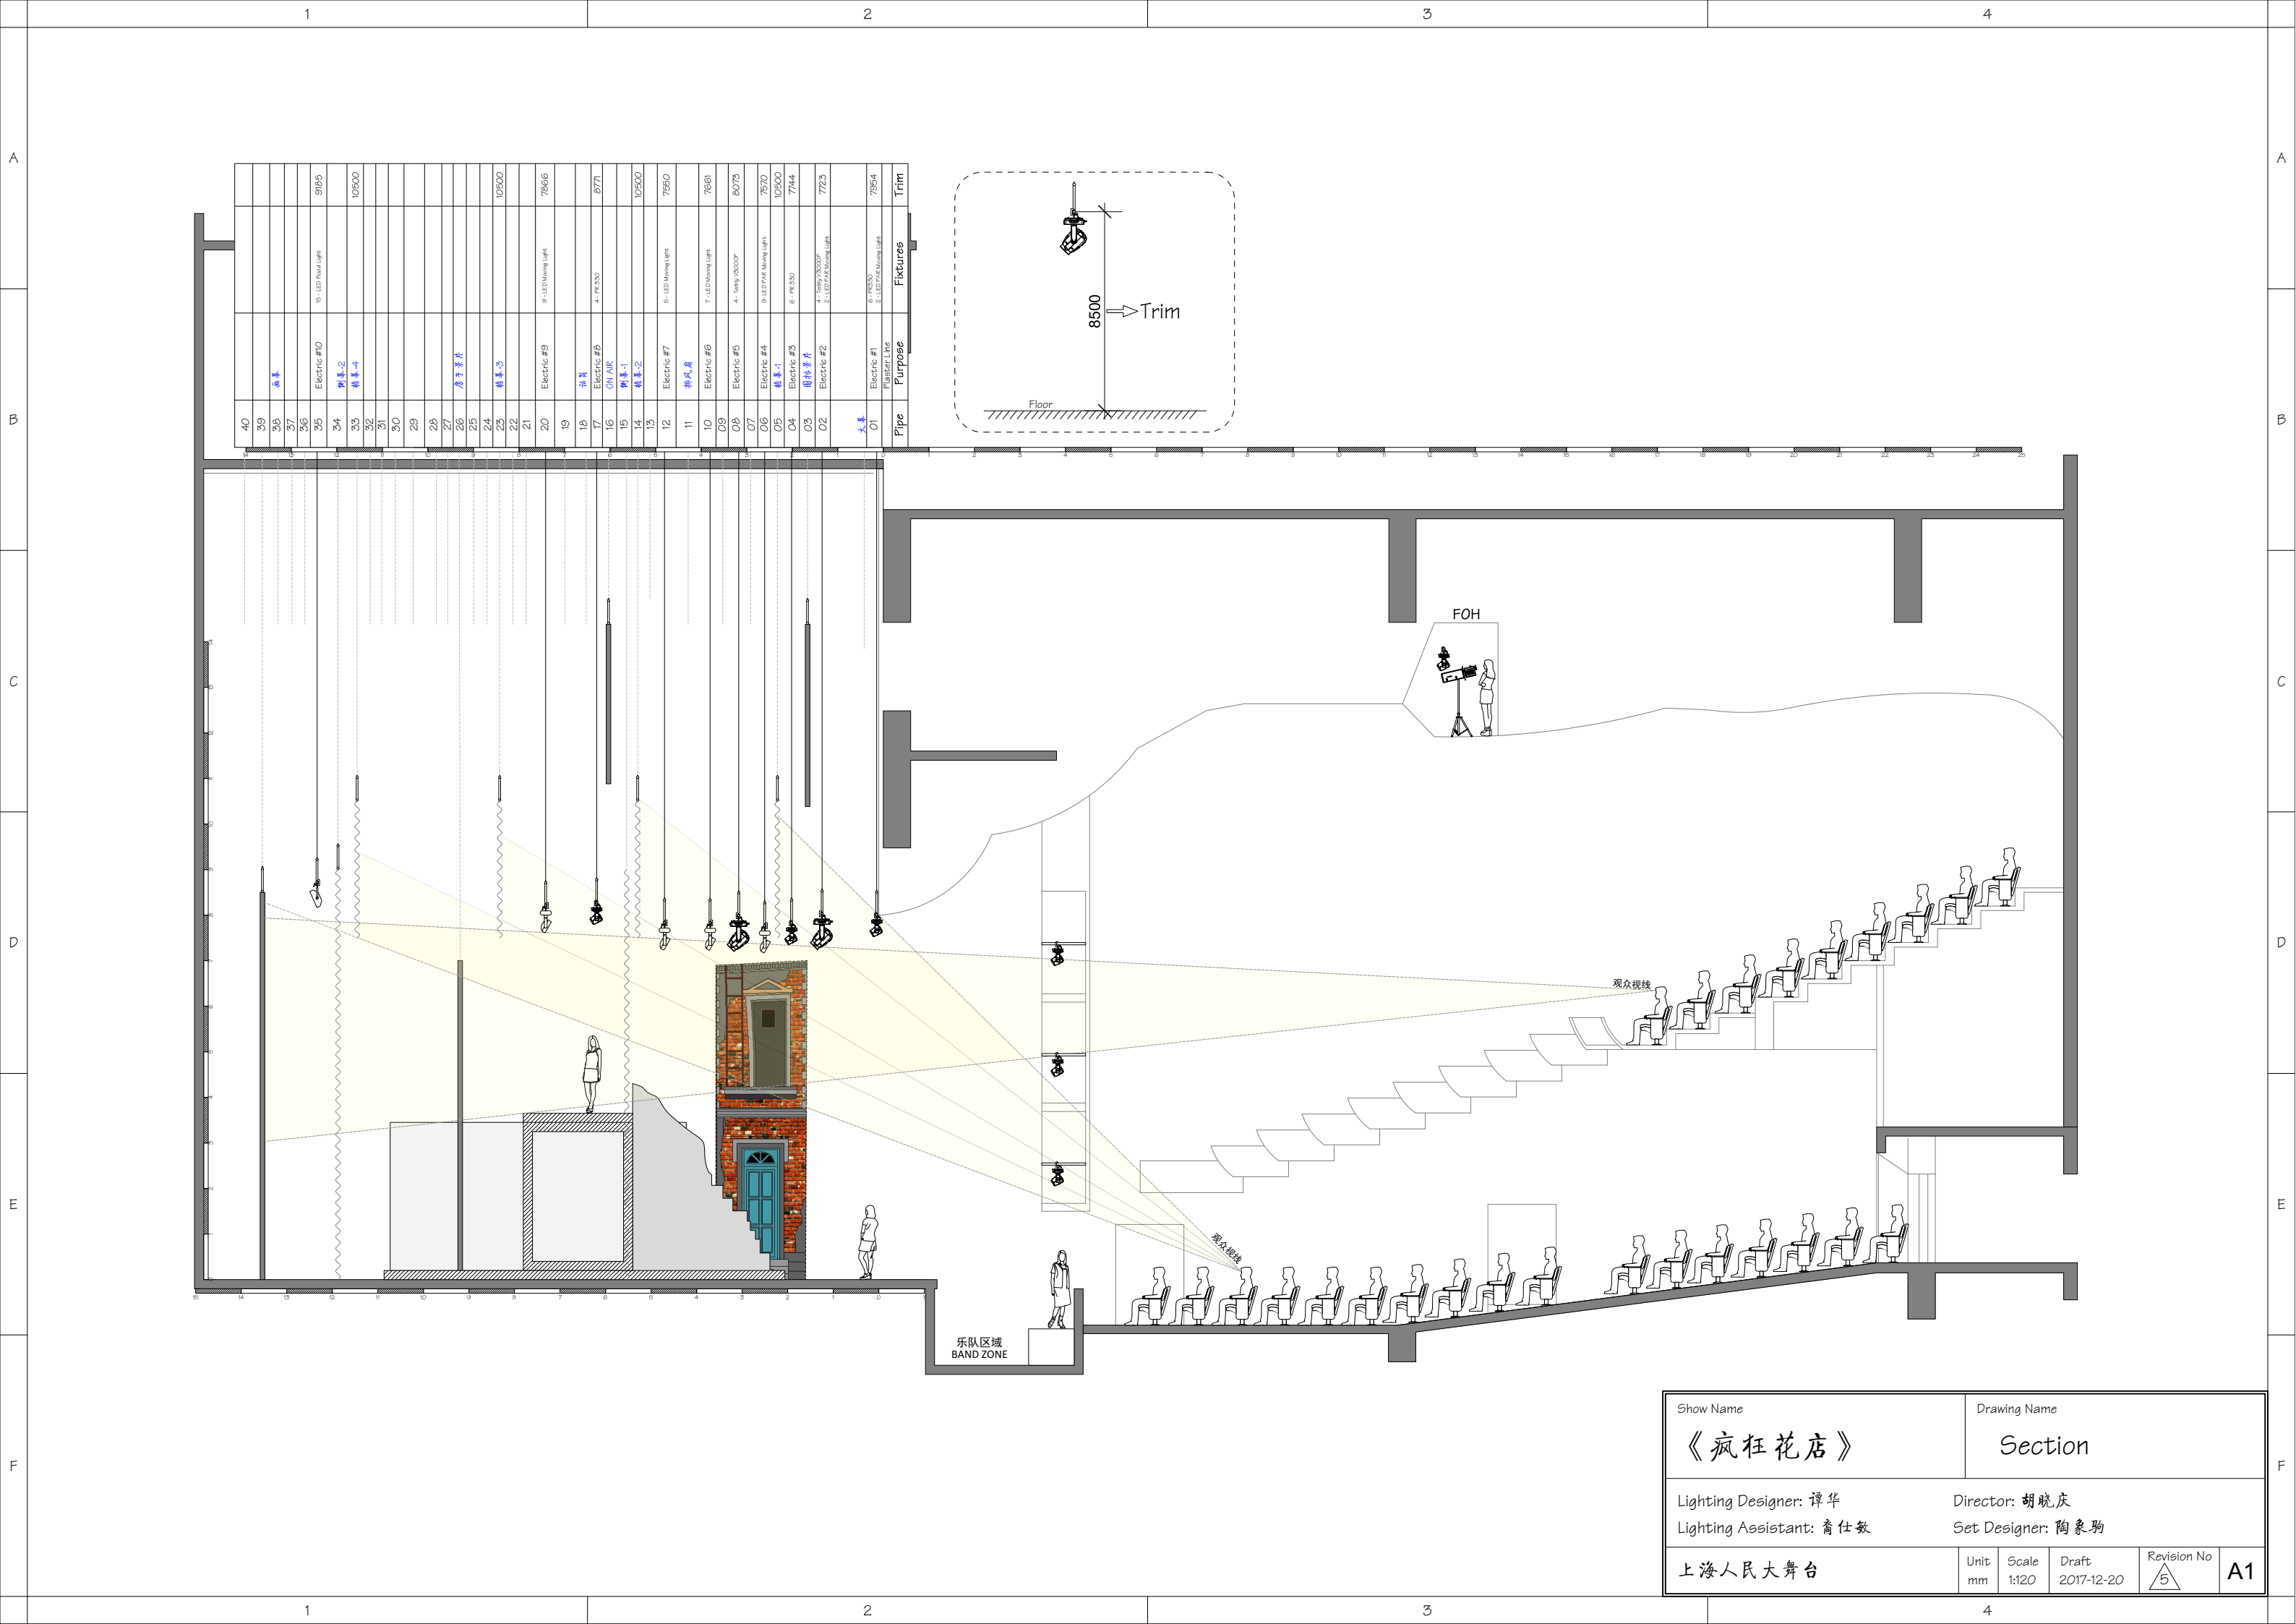

Show Name		Drawing Name			
《疯狂花店》		Section			
Lighting Designer: 谭华		Director: 胡晓庆			
Lighting Assistant: 裔仕敏		Set Designer: 陶象驹			
上海人民大舞台		Unit mm	Scale 1:120	Draft 2017-12-20	Revision No 5 A1

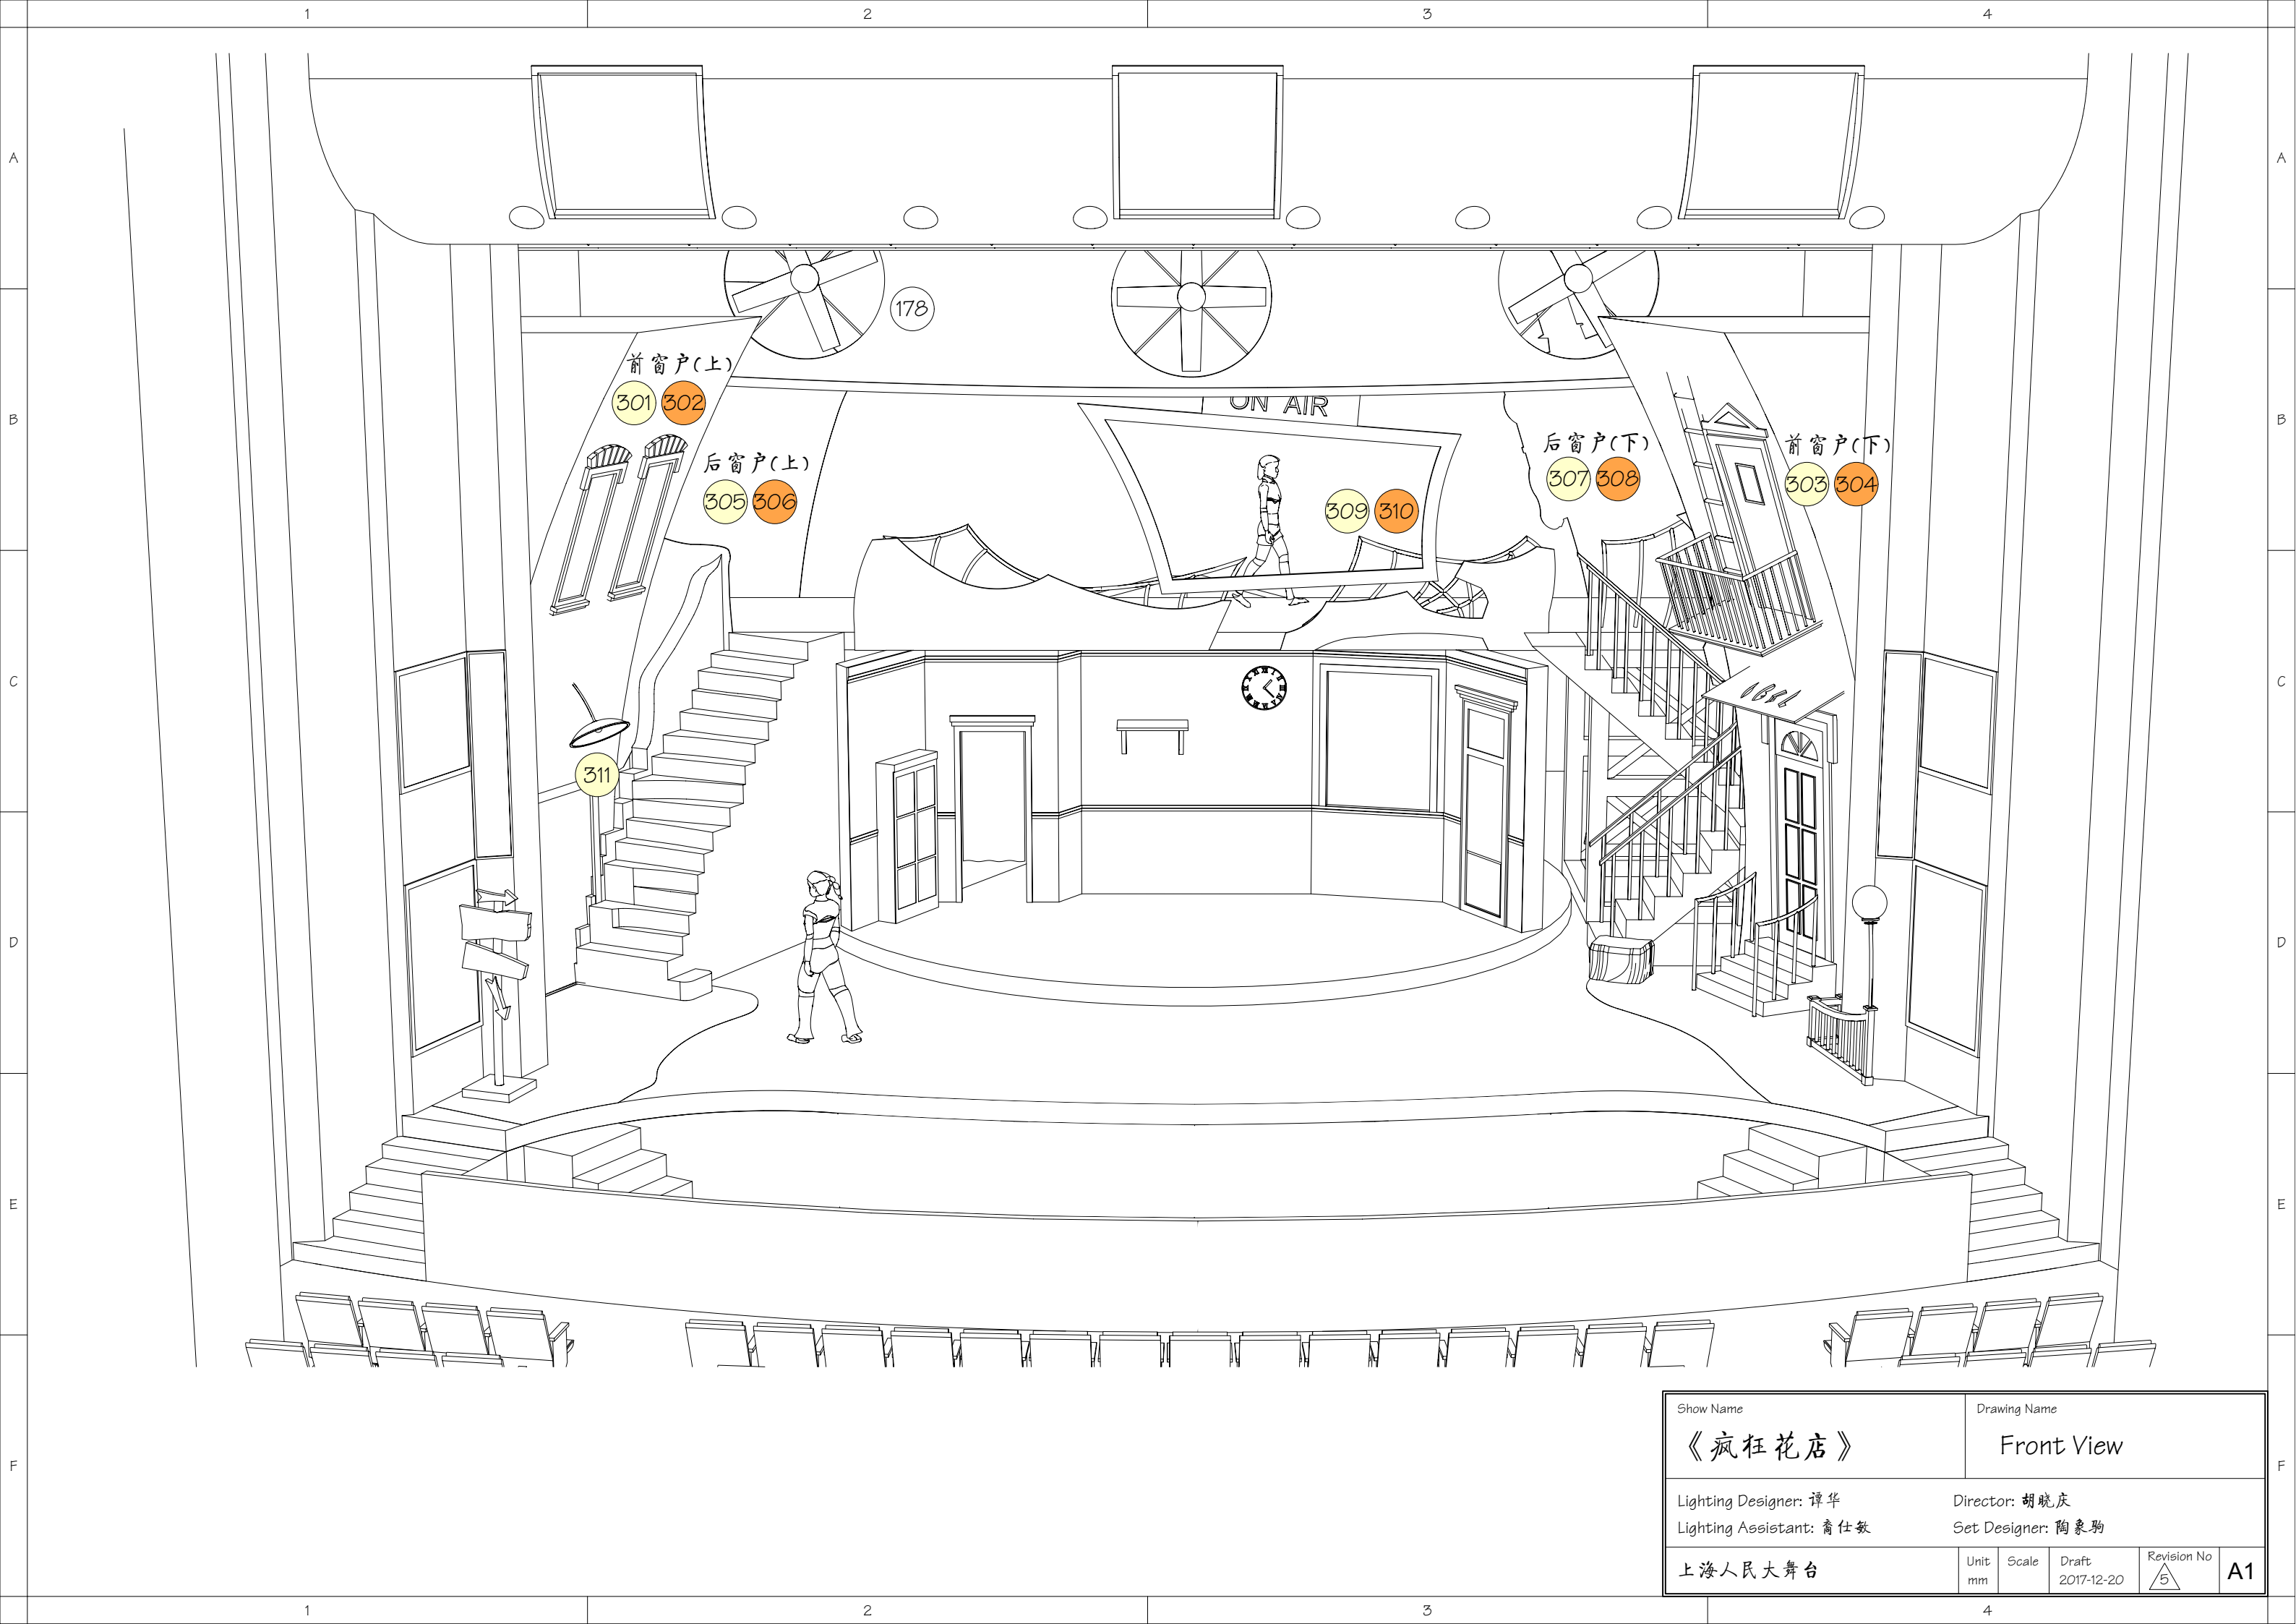

Show Name 《疯狂花店》		Drawing Name Front View	
Lighting Designer: 谭华 Lighting Assistant: 詹仕敏		Director: 胡晓庆 Set Designer: 陶象驹	
上海人民大舞台	Unit mm	Scale 2017-12-20	Revision No 5 A1

Magic Sheet for lighting

○ — Fixt #
■ — Group

1 面光 Front Light

1 2 3 4 5 6 7

2 耳光 Side Light

11 上层 12
13 中层 14
15 下层 16

3 高位侧 Cross Light

53 51 54 52 13
41 44 42 45 43 46 12
31 34 32 35 33 36 11

4 逆光 Back Light

91 92 93 94 95 96 97 98 99 17
81 82 83 84 85 16
71 72 73 74 75 76 77 15
61 62 63 64 65 66 67 68 69 14

5 顶光 Down Light

121 122 123 124 19
111 112 113 114 18

6 景片染色 SETs Wash

23 24
21 22

7 其它 Others

天排 131 132 133 ... 145 21
脚光 101 102 103 104 105 106 107 20
烟机 201 雾机 202

暖 红 暖 红
前窗户(上) 301 302 前窗户(下) 303 304
暖 红 暖 红
前窗户(上) 305 306 前窗户(下) 307 308
暖 红
ON AIR 309 310 路灯 311 排风扇 178

吊杆编号 Pipe No.

高位侧	1, 4, 17	顶光	2, 8
逆光	6, 10, 12, 20	景片染色	1, 2
檐幕	5, 14, 23, 33	侧幕	15, 34
围挡景片	3	排风扇	11
食人花	13	ON AIR	16
话筒	18	房子景片	26
画幕	38		