


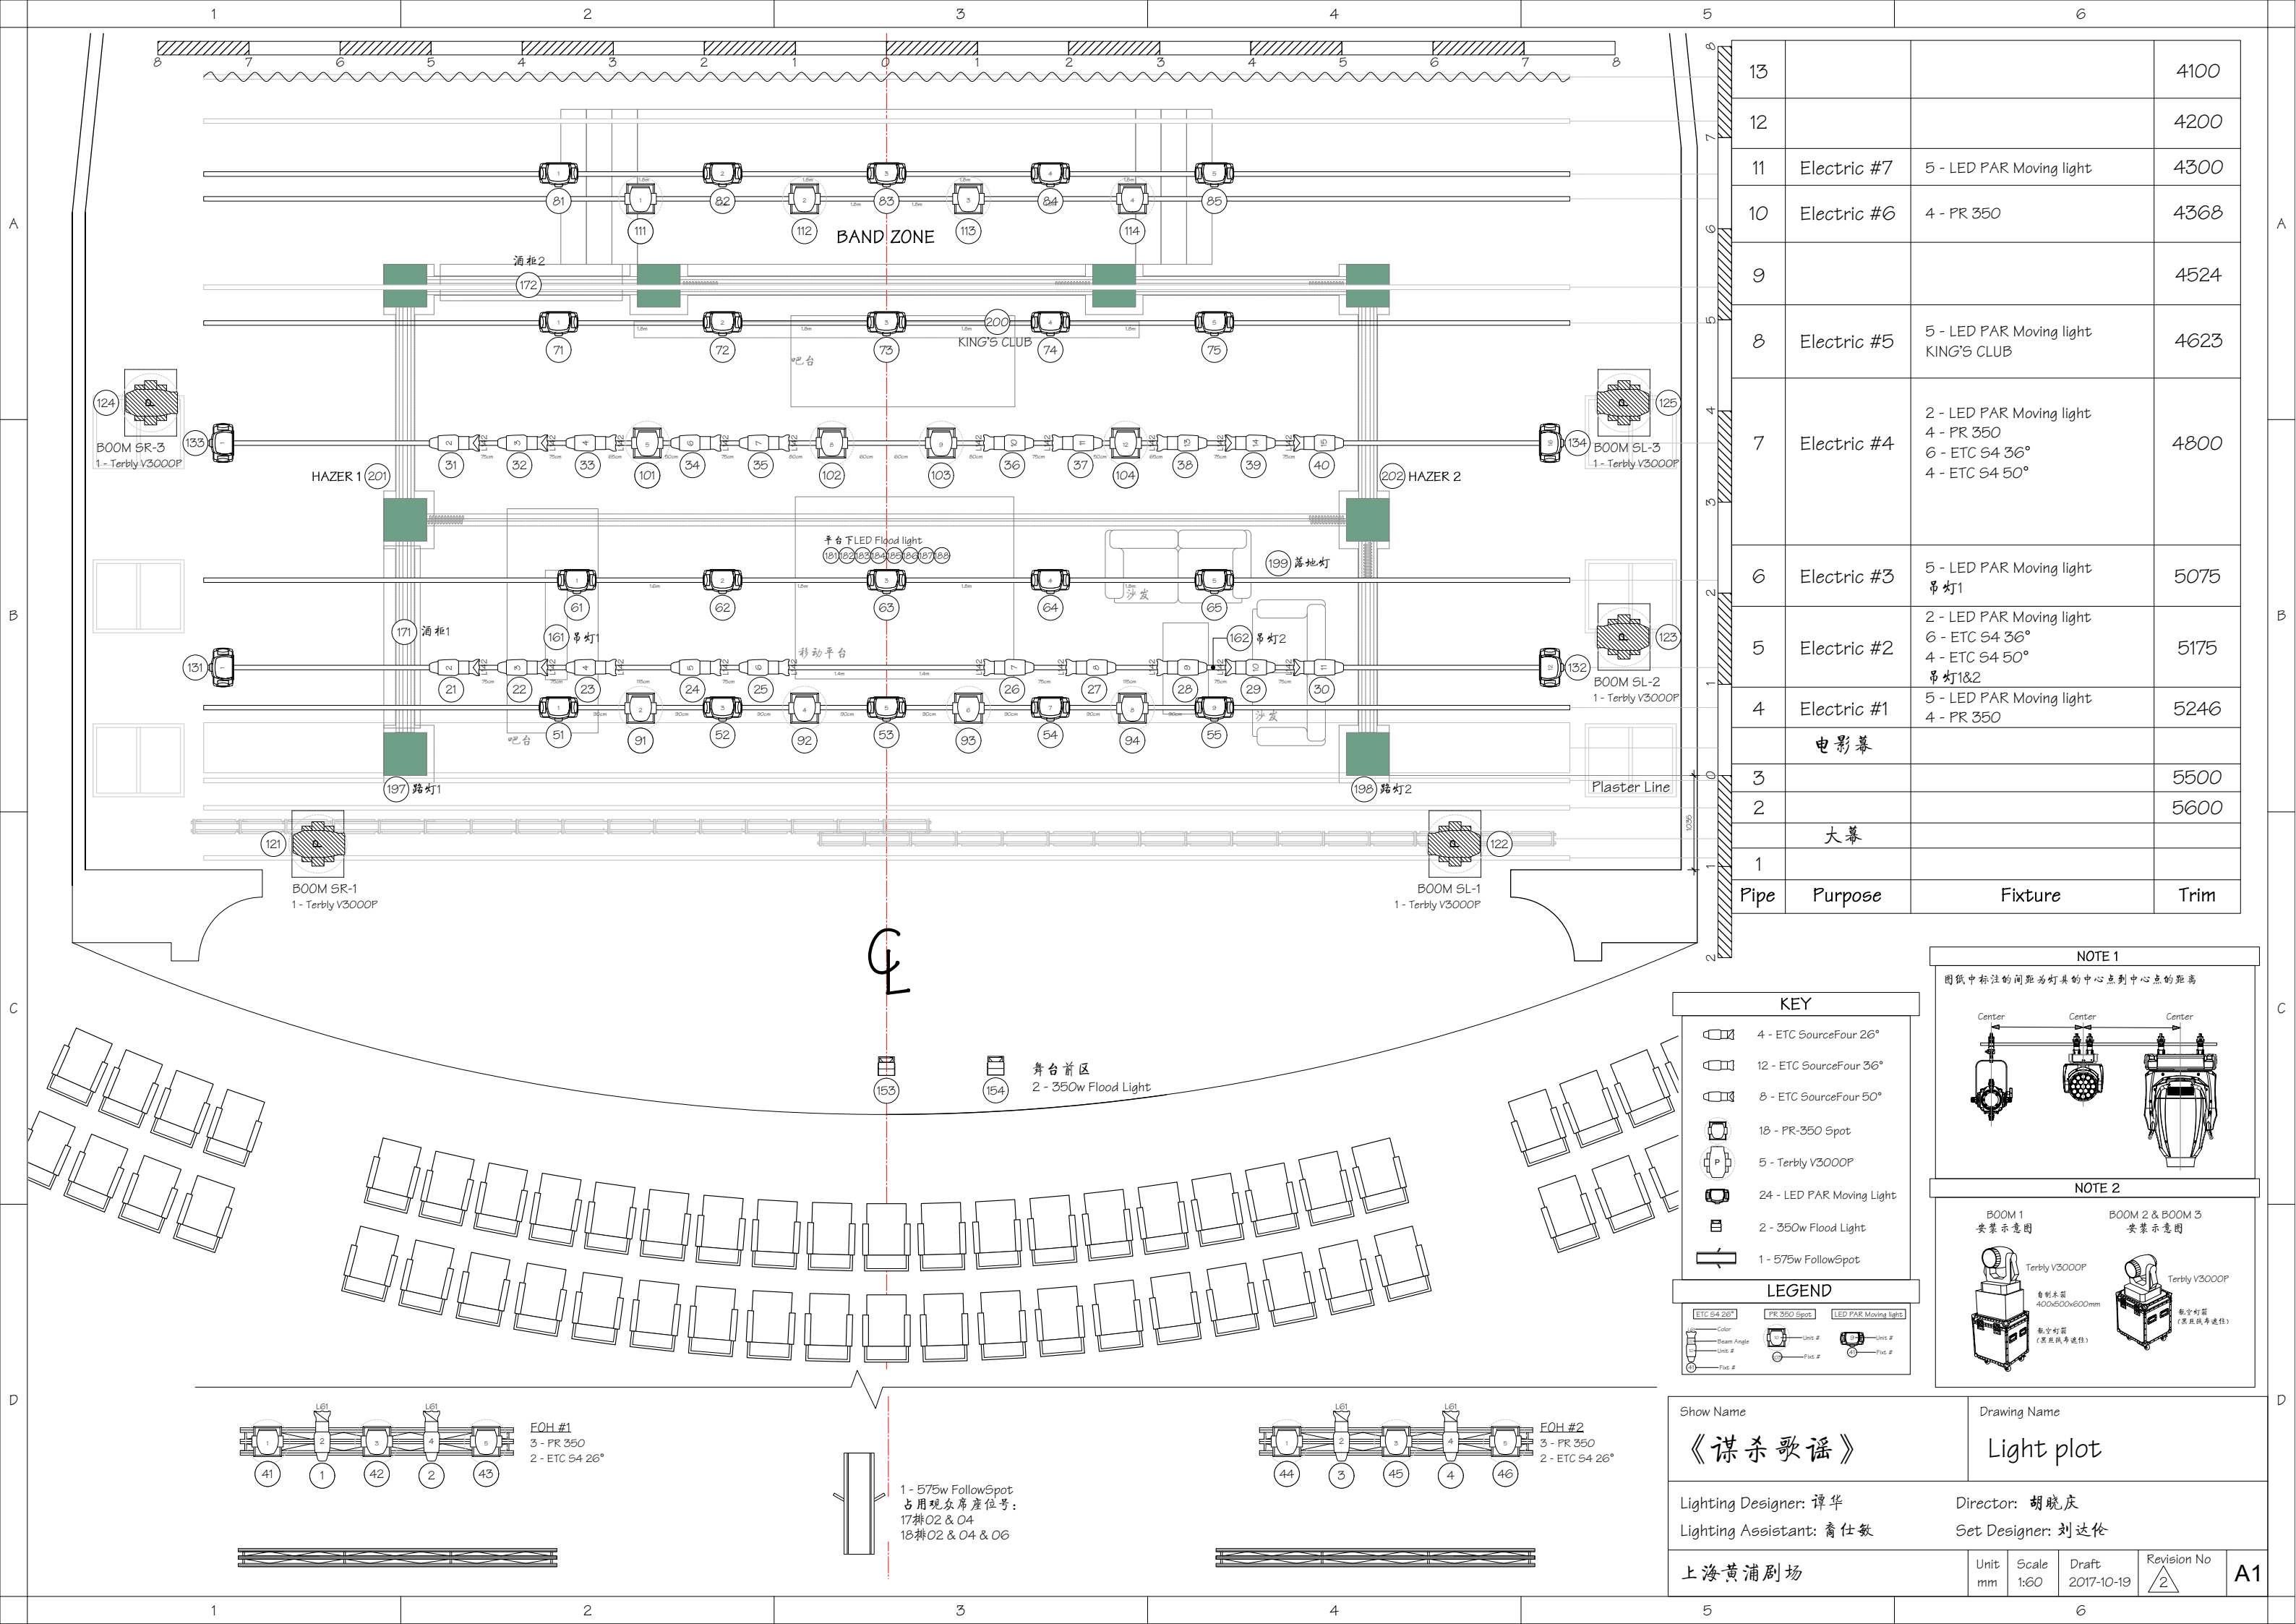

13			4100
12			4200
11	Electric #7	5 - LED PAR Moving light	4300
10	Electric #6	4 - PR 350	4368
9			4524
8	Electric #5	5 - LED PAR Moving light KING'S CLUB	4623
7	Electric #4	2 - LED PAR Moving light 4 - PR 350 6 - ETC S4 36° 4 - ETC S4 50°	4800
6	Electric #3	5 - LED PAR Moving light 吊灯1	5075
5	Electric #2	2 - LED PAR Moving light 6 - ETC S4 36° 4 - ETC S4 50° 吊灯1&2	5175
4	Electric #1	5 - LED PAR Moving light 4 - PR 350	5246
	电影幕		
3			5500
2			5600
	大幕		
1			
Pipe	Purpose	Fixture	Trim

KEY

4 - ETC SourceFour 26°

12 - ETC SourceFour 36°

8 - ETC SourceFour 50°

18 - PR-350 Spot

5 - Terbly V3000P

24 - LED PAR Moving Light

2 - 350w Flood Light

1 - 575w FollowSpot

LEGEND

ETC S4 26°

PR 350 Spot

LED PAR Moving Light

Color

Beam Angle

Units #

Fixt #

NOTE 1

图中标注的间距为灯具的中心点到中心点的距离

Center

Center

Center

NOTE 2

BOOM 1
安装示意图

BOOM 2 & BOOM 3
安装示意图

Terbly V3000P
自制吊杆
400x500x600mm
数字灯臂
(高低线吊挂)

Terbly V3000P
数字灯臂
(高低线吊挂)

Show Name

《谋杀歌谣》

Drawing Name

Light plot

Lighting Designer: 谭华

Lighting Assistant: 詹仕敦

Director: 胡晓庆

Set Designer: 刘达伦

上海黄浦剧场

Unit mm

Scale 1:60

Draft 2017-10-19

Revision No 2

A1