



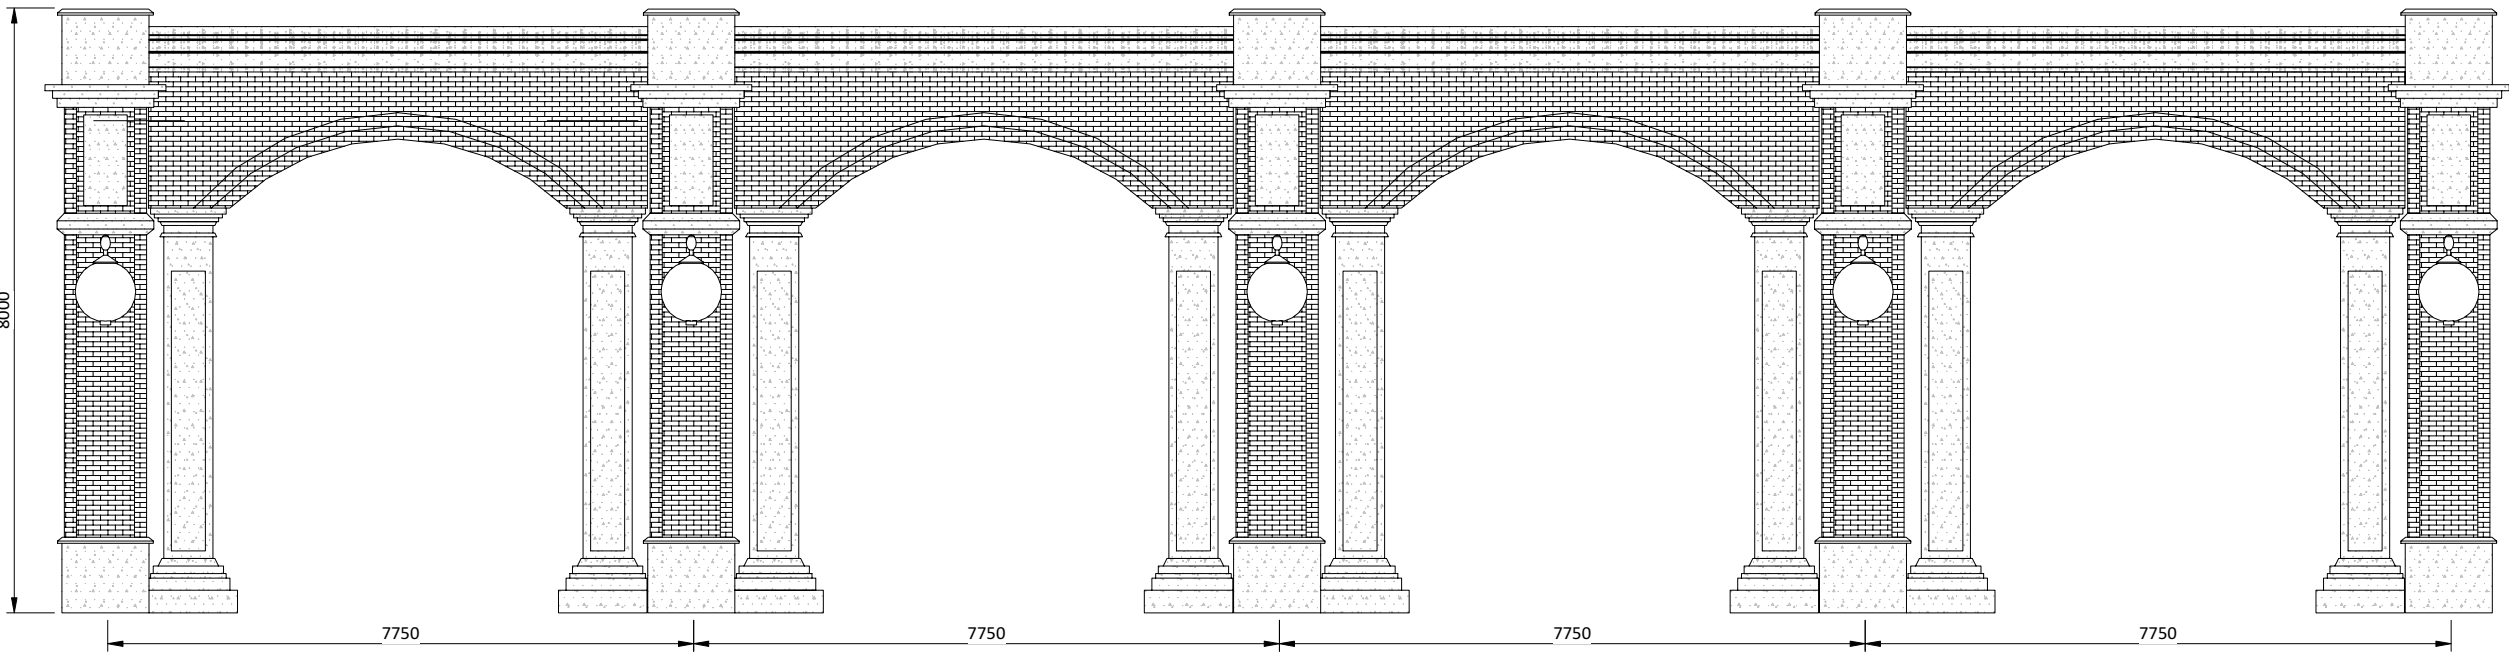


舞台正视图
1:100

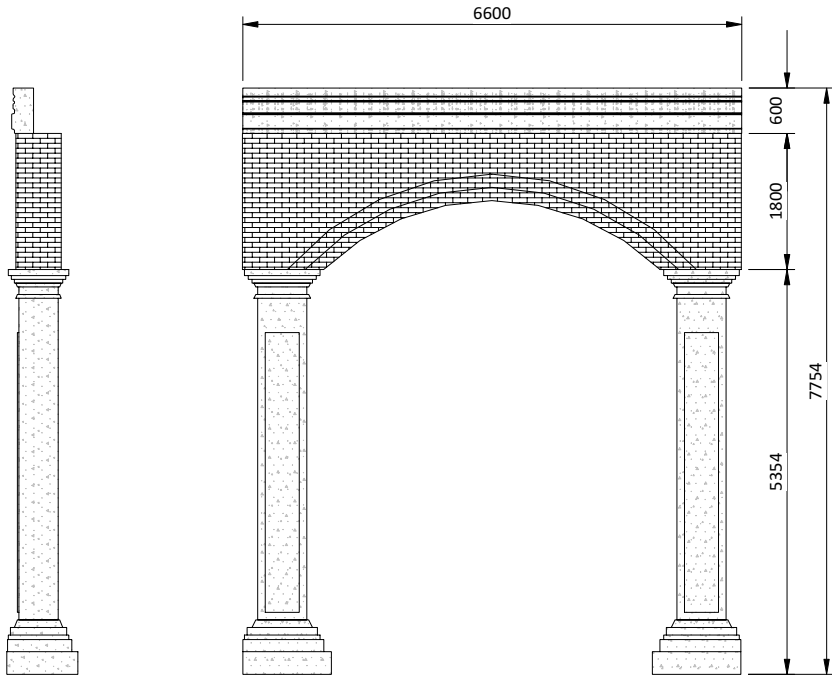


拱门-左视图
1:100

拱门-正视图
1:100

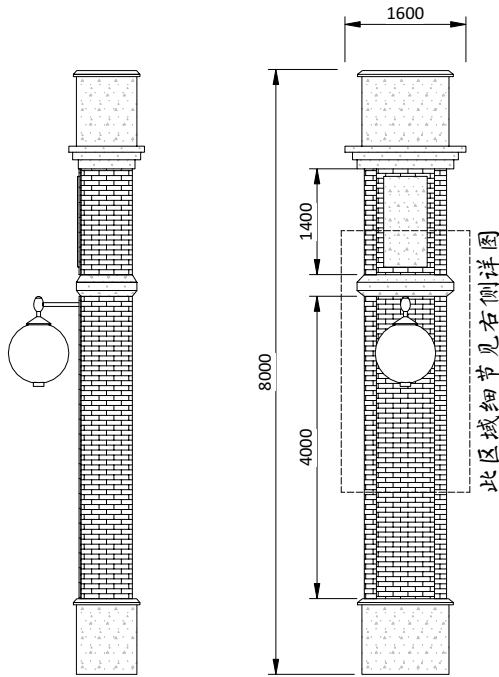


柱子-左视图
1:100


柱子-正视图
1:100

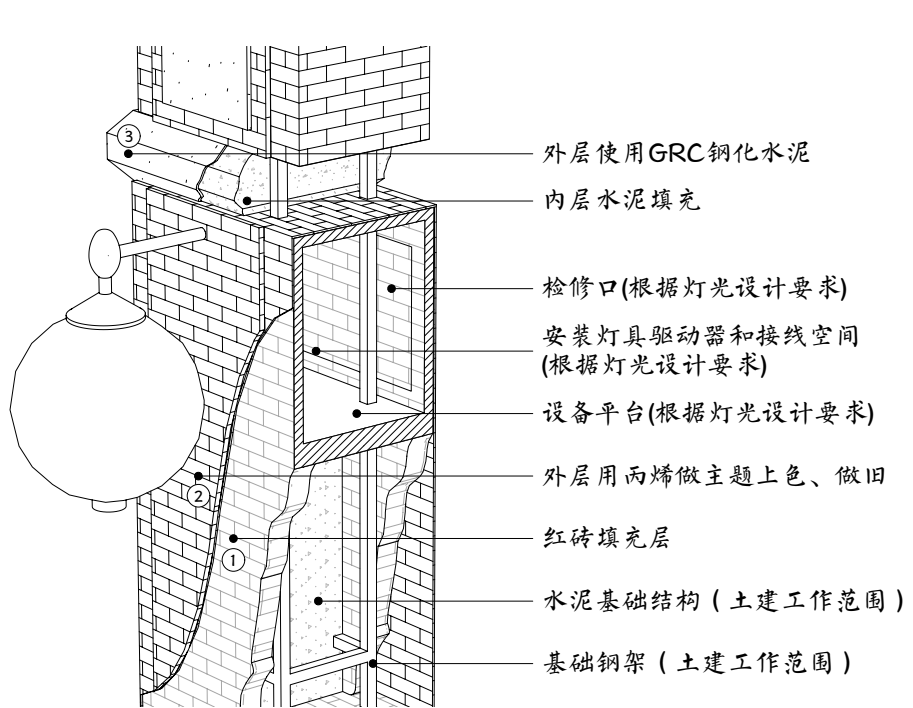

柱子结构解剖示意图

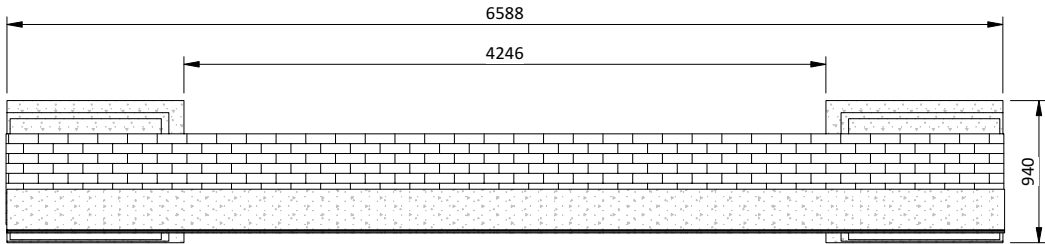

拱门-顶视图
1:50

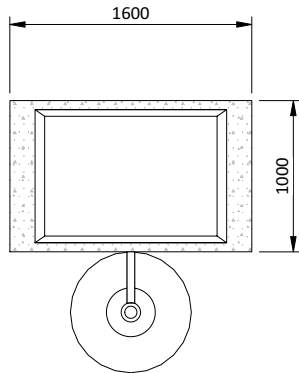

柱子-顶视图
1:50

材质参考



深化设计：与导演、舞台设计、灯光设计、机械设计沟通，配合完成细节结构深化及艺术效果的体现。

舞美制作工序步骤：

第一步：砌砖，砌石头，抹墙，抹石灰水泥，安瓦片等
第二步：做装饰类的安装。把翻模好的钢化石膏线条或钢化水泥，玻璃钢，门窗等安装好。
第三步：把平面的图纸按要求主体工程完工后，开始按图纸要求做场景的主题效果上色、仿古做旧或彩绘。按设定的故事背景，情节和要求还原场景的真实写照。
第四步：摆道具按照场景的大效果结合道具效果，做最后的调整 and 统一。

修正版次:		
版次	日期	内容

项目名称:		导演: 王潮歌	
《只有河南》		舞台设计:	
		技术总监:	
		深化设计:	
专业: 舞台制作		校对:	

图纸名称:			
局部深化设计示例图 场景1-1			

第 页	单位:	制图日期:	版次:	A3
共 页	mm	2019.1.18		

非最终施工图纸