

图例

符号	灯具型号	数量
	Ayrton EURUS TC	70
	Martin Viper Wash DX	35
	雪花机	4

通用说明:

Center

Dimension

Center

Dimension

Center

Dimension

Center

Dimension

Beam Angle

Unit #

Unit #

Unit #

10

10


10

Figure #


Figure #

Figure #


表示地面安装灯具

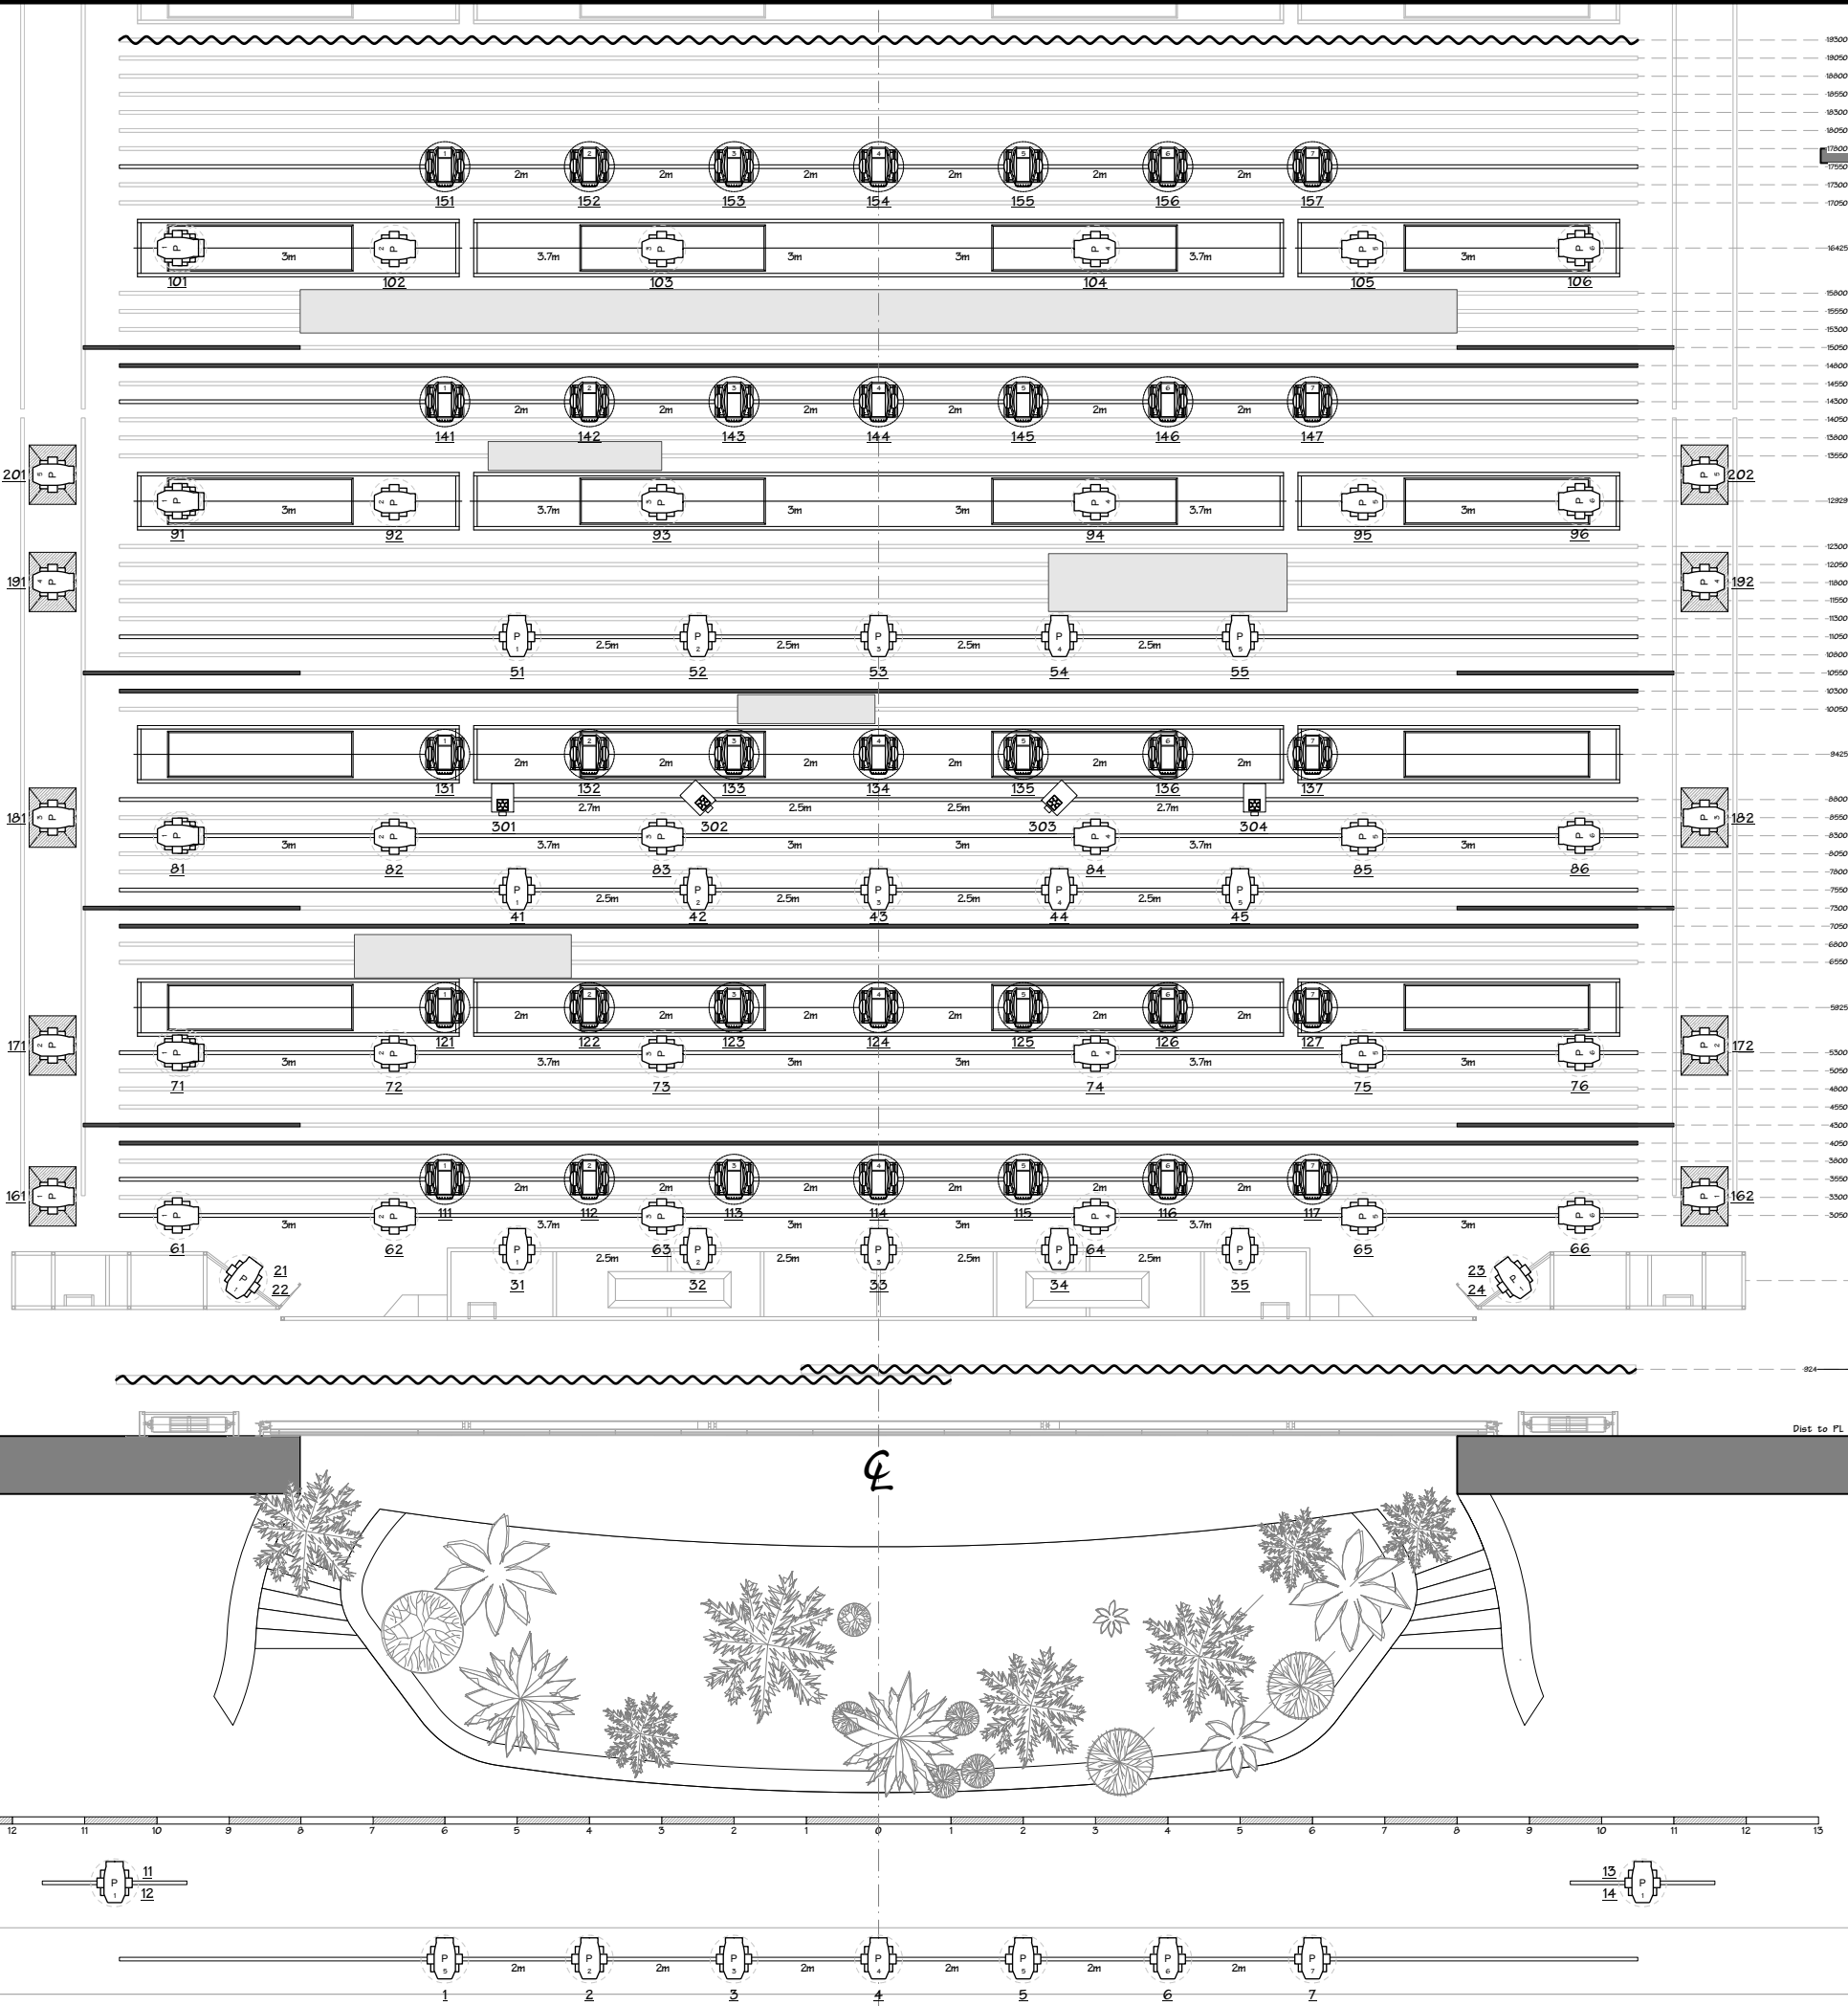

350	黑幕		
349			
348			
347			
346			
345			
344			
343	Electric #12	9200	
342			
341			
D4	Electric #11	8900	
340			
339	三角装置		
338			
337	侧幕4		
336	侧幕4		
335			
334	Electric #10	9900	
333			
332			
331	高梁4—流苏		
D3	Electric #9	9400	
330			
329			
328	高梁1—开场/拉幕/翻桥		
327			
326			
325	Electric #8	8800	
324	侧幕3		
323	侧幕3		
322	侧幕3		
321	高梁5—留种		
D2	Electric #7	9600	
320	雪花机		
319			
318	Electric #6	9100	
317			
316			
315	Electric #5	8800	
314	侧幕2		
313	侧幕2		
312			
311	高梁2—野合		
D1	Electric #4	9400	
310	Electric #3	9100	
309			
308			
307			
306	侧幕1		
305	侧幕1		
304			
303			
302	Electric #2	9200	
301			
300	Electric #1	9000	
假台口			
大幕			
序号 LINE#	用途 PURPOSE	高度 TRIM	重量 WEIGHT(KG)

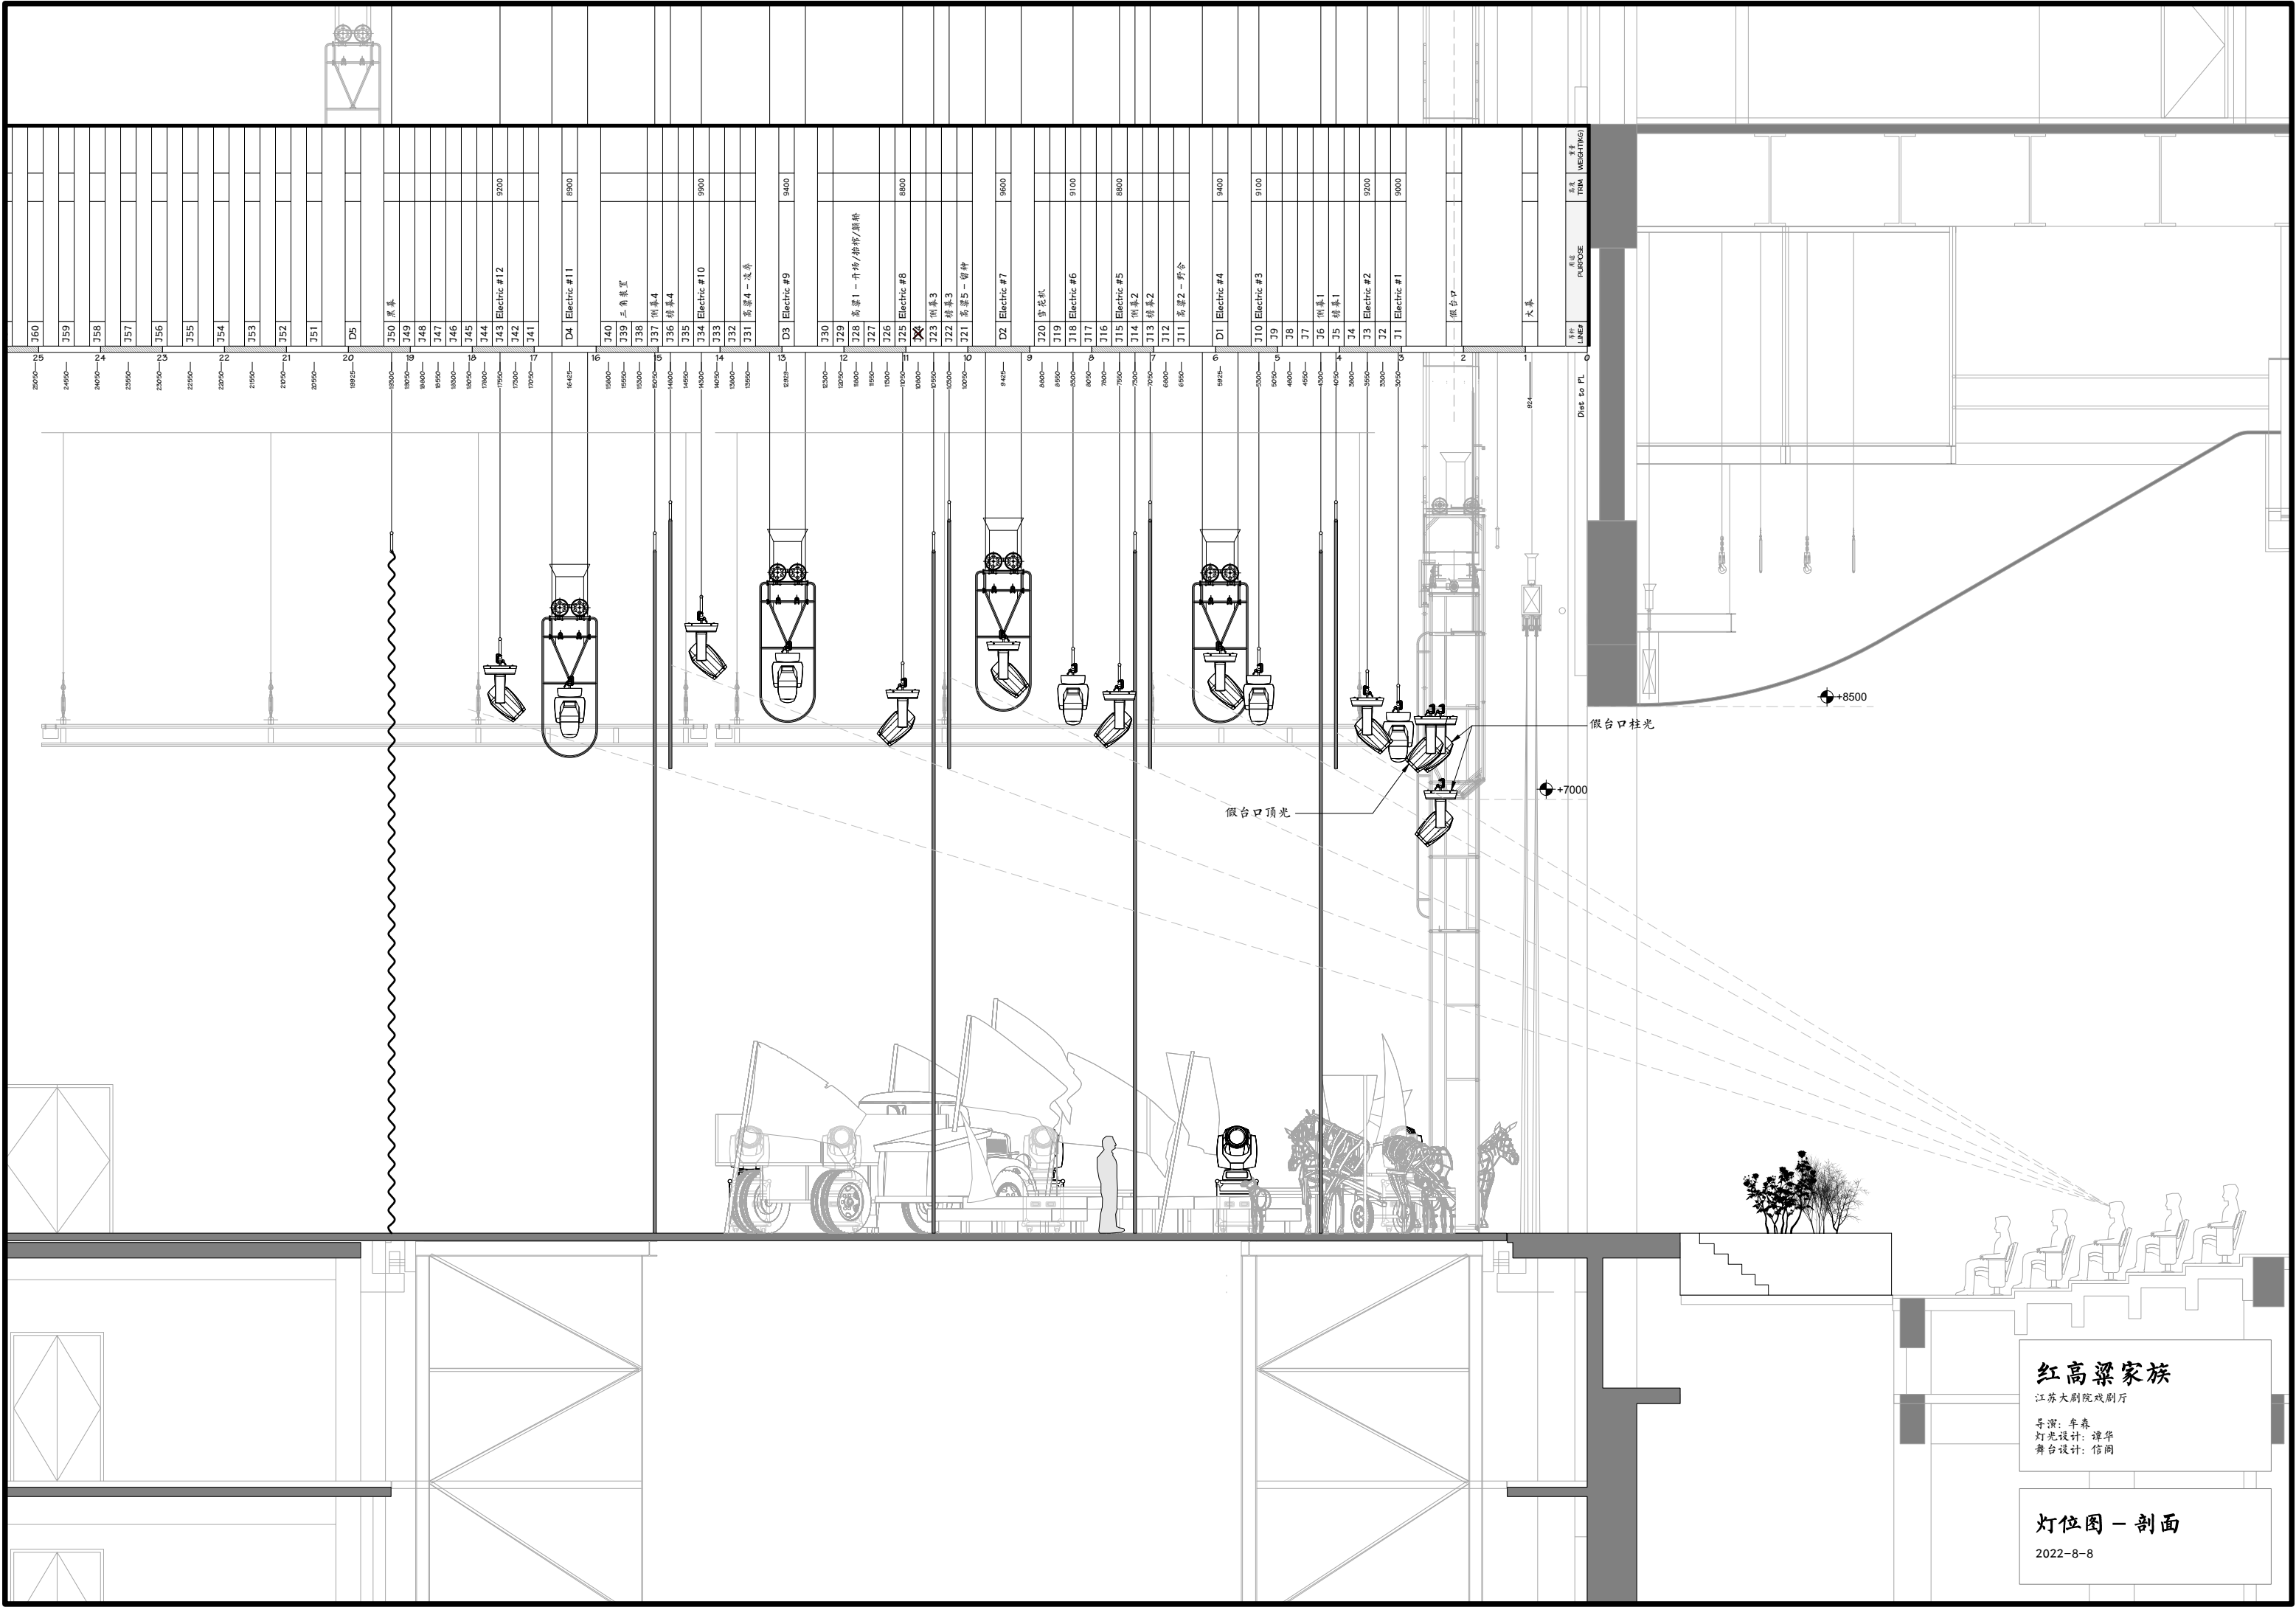

LINE#	用途	用途	重量
LINE#	PURPOSE	PURPOSE	TRM (WEIGHTKG)
760			
759			
758			
757			
756			
755			
754			
753			
752			
751			
D5			
150	黑车		
149			
148			
147			
146			
145			
144	Electric #12		9200
143			
142			
141			
D4	Electric #11		8900
140			
139	三角装置		
138			
137	侧幕4		
136	侧幕4		
135			
134	Electric #10		9900
133			
132			
131	侧幕4 - 设备		
D3	Electric #9		9400
130			
129			
128	侧幕1 - 吊钩/吊钩/吊钩		
127			
126			
125	Electric #8		8800
124			
123	侧幕3		
122	侧幕3		
121	侧幕5 - 留种		
D2	Electric #7		9600
120	雪花机		
119			
118	Electric #6		9100
117			
116			
115	Electric #5		8800
114	侧幕2		
113	侧幕2		
112			
111	侧幕2 - 新合		
D1	Electric #4		9400
110	Electric #3		9100
109			
108			
107			
106			
105			
104			
103			
102			
101			
100			
99			
98			
97			
96			
95			
94			
93			
92			
91			
90			
89			
88			
87			
86			
85			
84			
83			
82			
81			
80			
79			
78			
77			
76	侧幕1		
75	侧幕1		
74			
73	Electric #2		9200
72			
71	Electric #1		9000
70			
69			
68			
67			
66			
65			
64			
63			
62			
61			
60			
59			
58			
57			
56			
55			
54			
53			
52			
51			
50			
49			
48			
47			
46			
45			
44			
43			
42			
41			
40			
39			
38			
37			
36			
35			
34			
33			
32			
31			
30			
29			
28			
27			
26			
25			
24			
23			
22			
21			
20			
19			
18			
17			
16			
15			
14			
13			
12			
11			
10			
9			
8			
7			
6			
5			
4			
3			
2			
1			

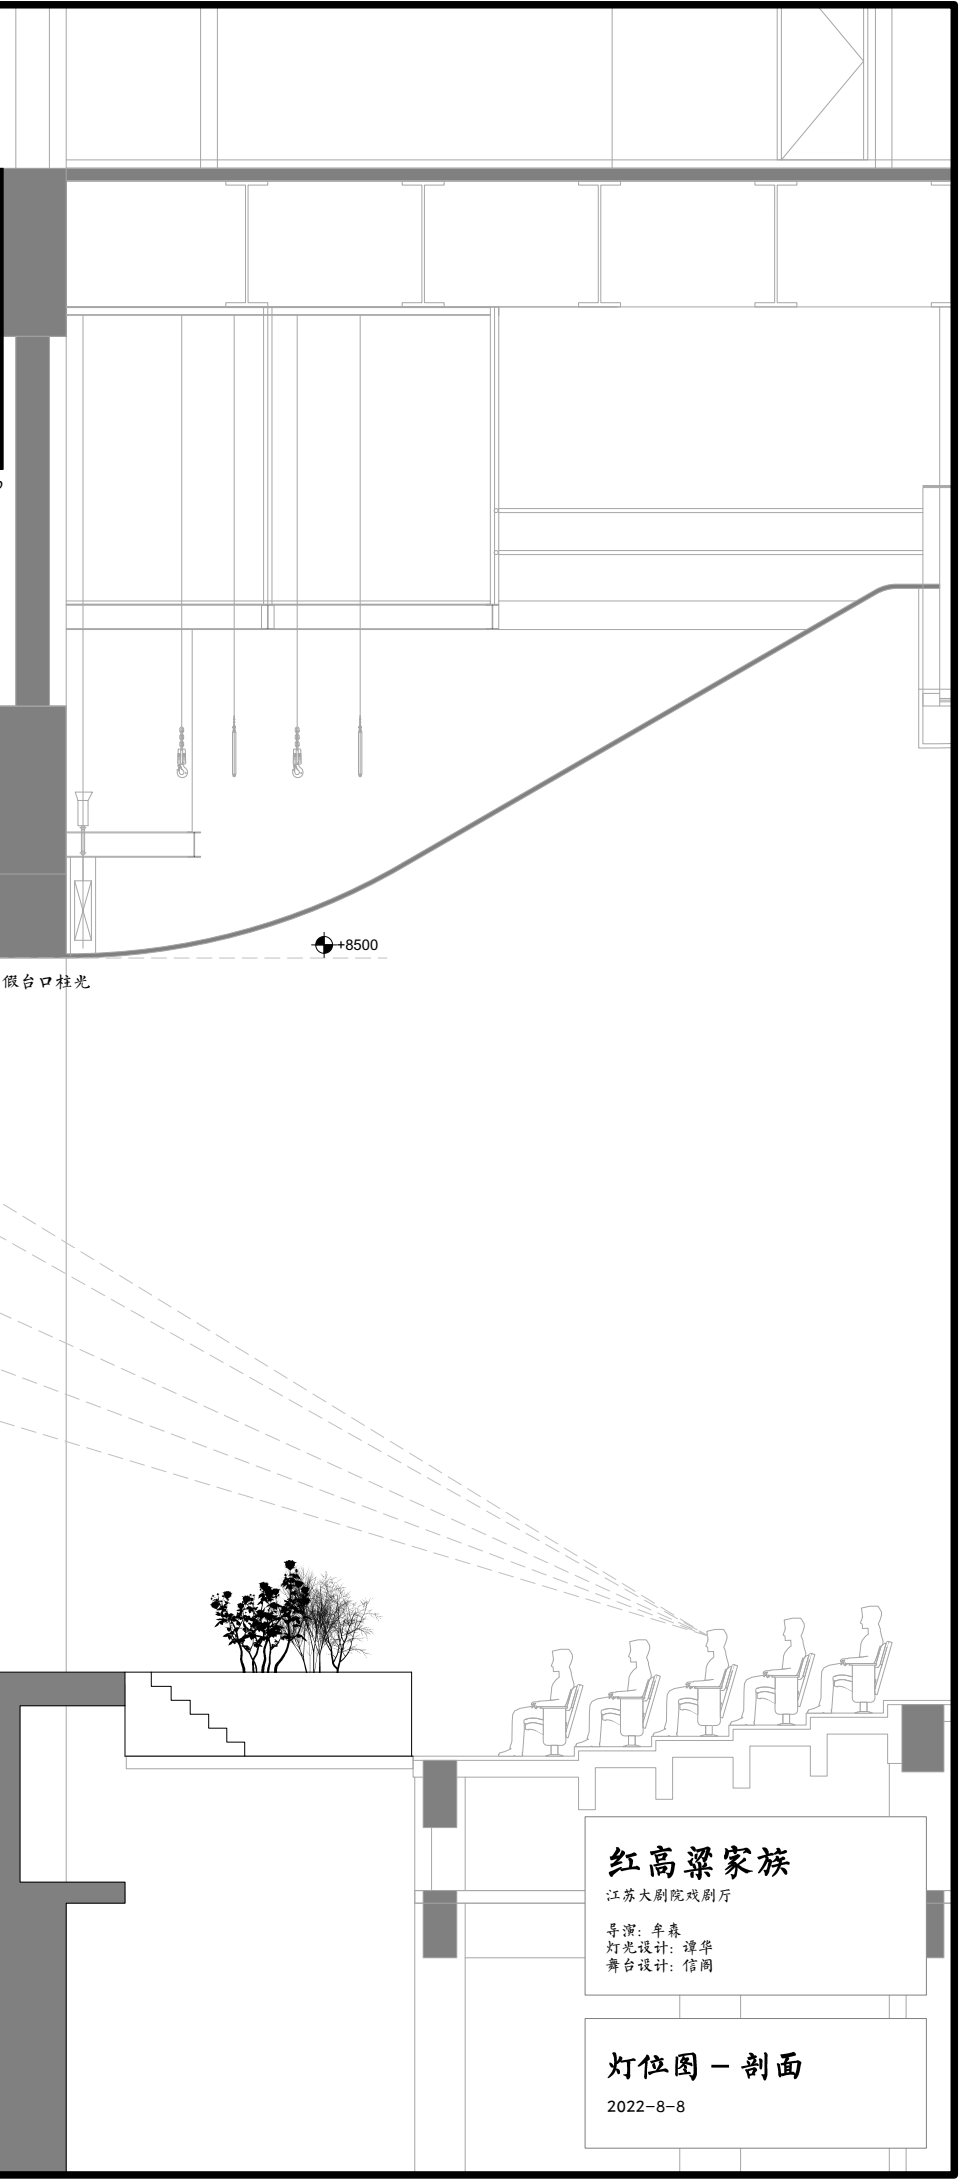

红高粱家族
江苏大剧院戏剧厅
导演: 牟森
灯光设计: 谭华
舞台设计: 信周

灯位图 - 剖面
2022-8-8