


2013东亚运动会
开幕式

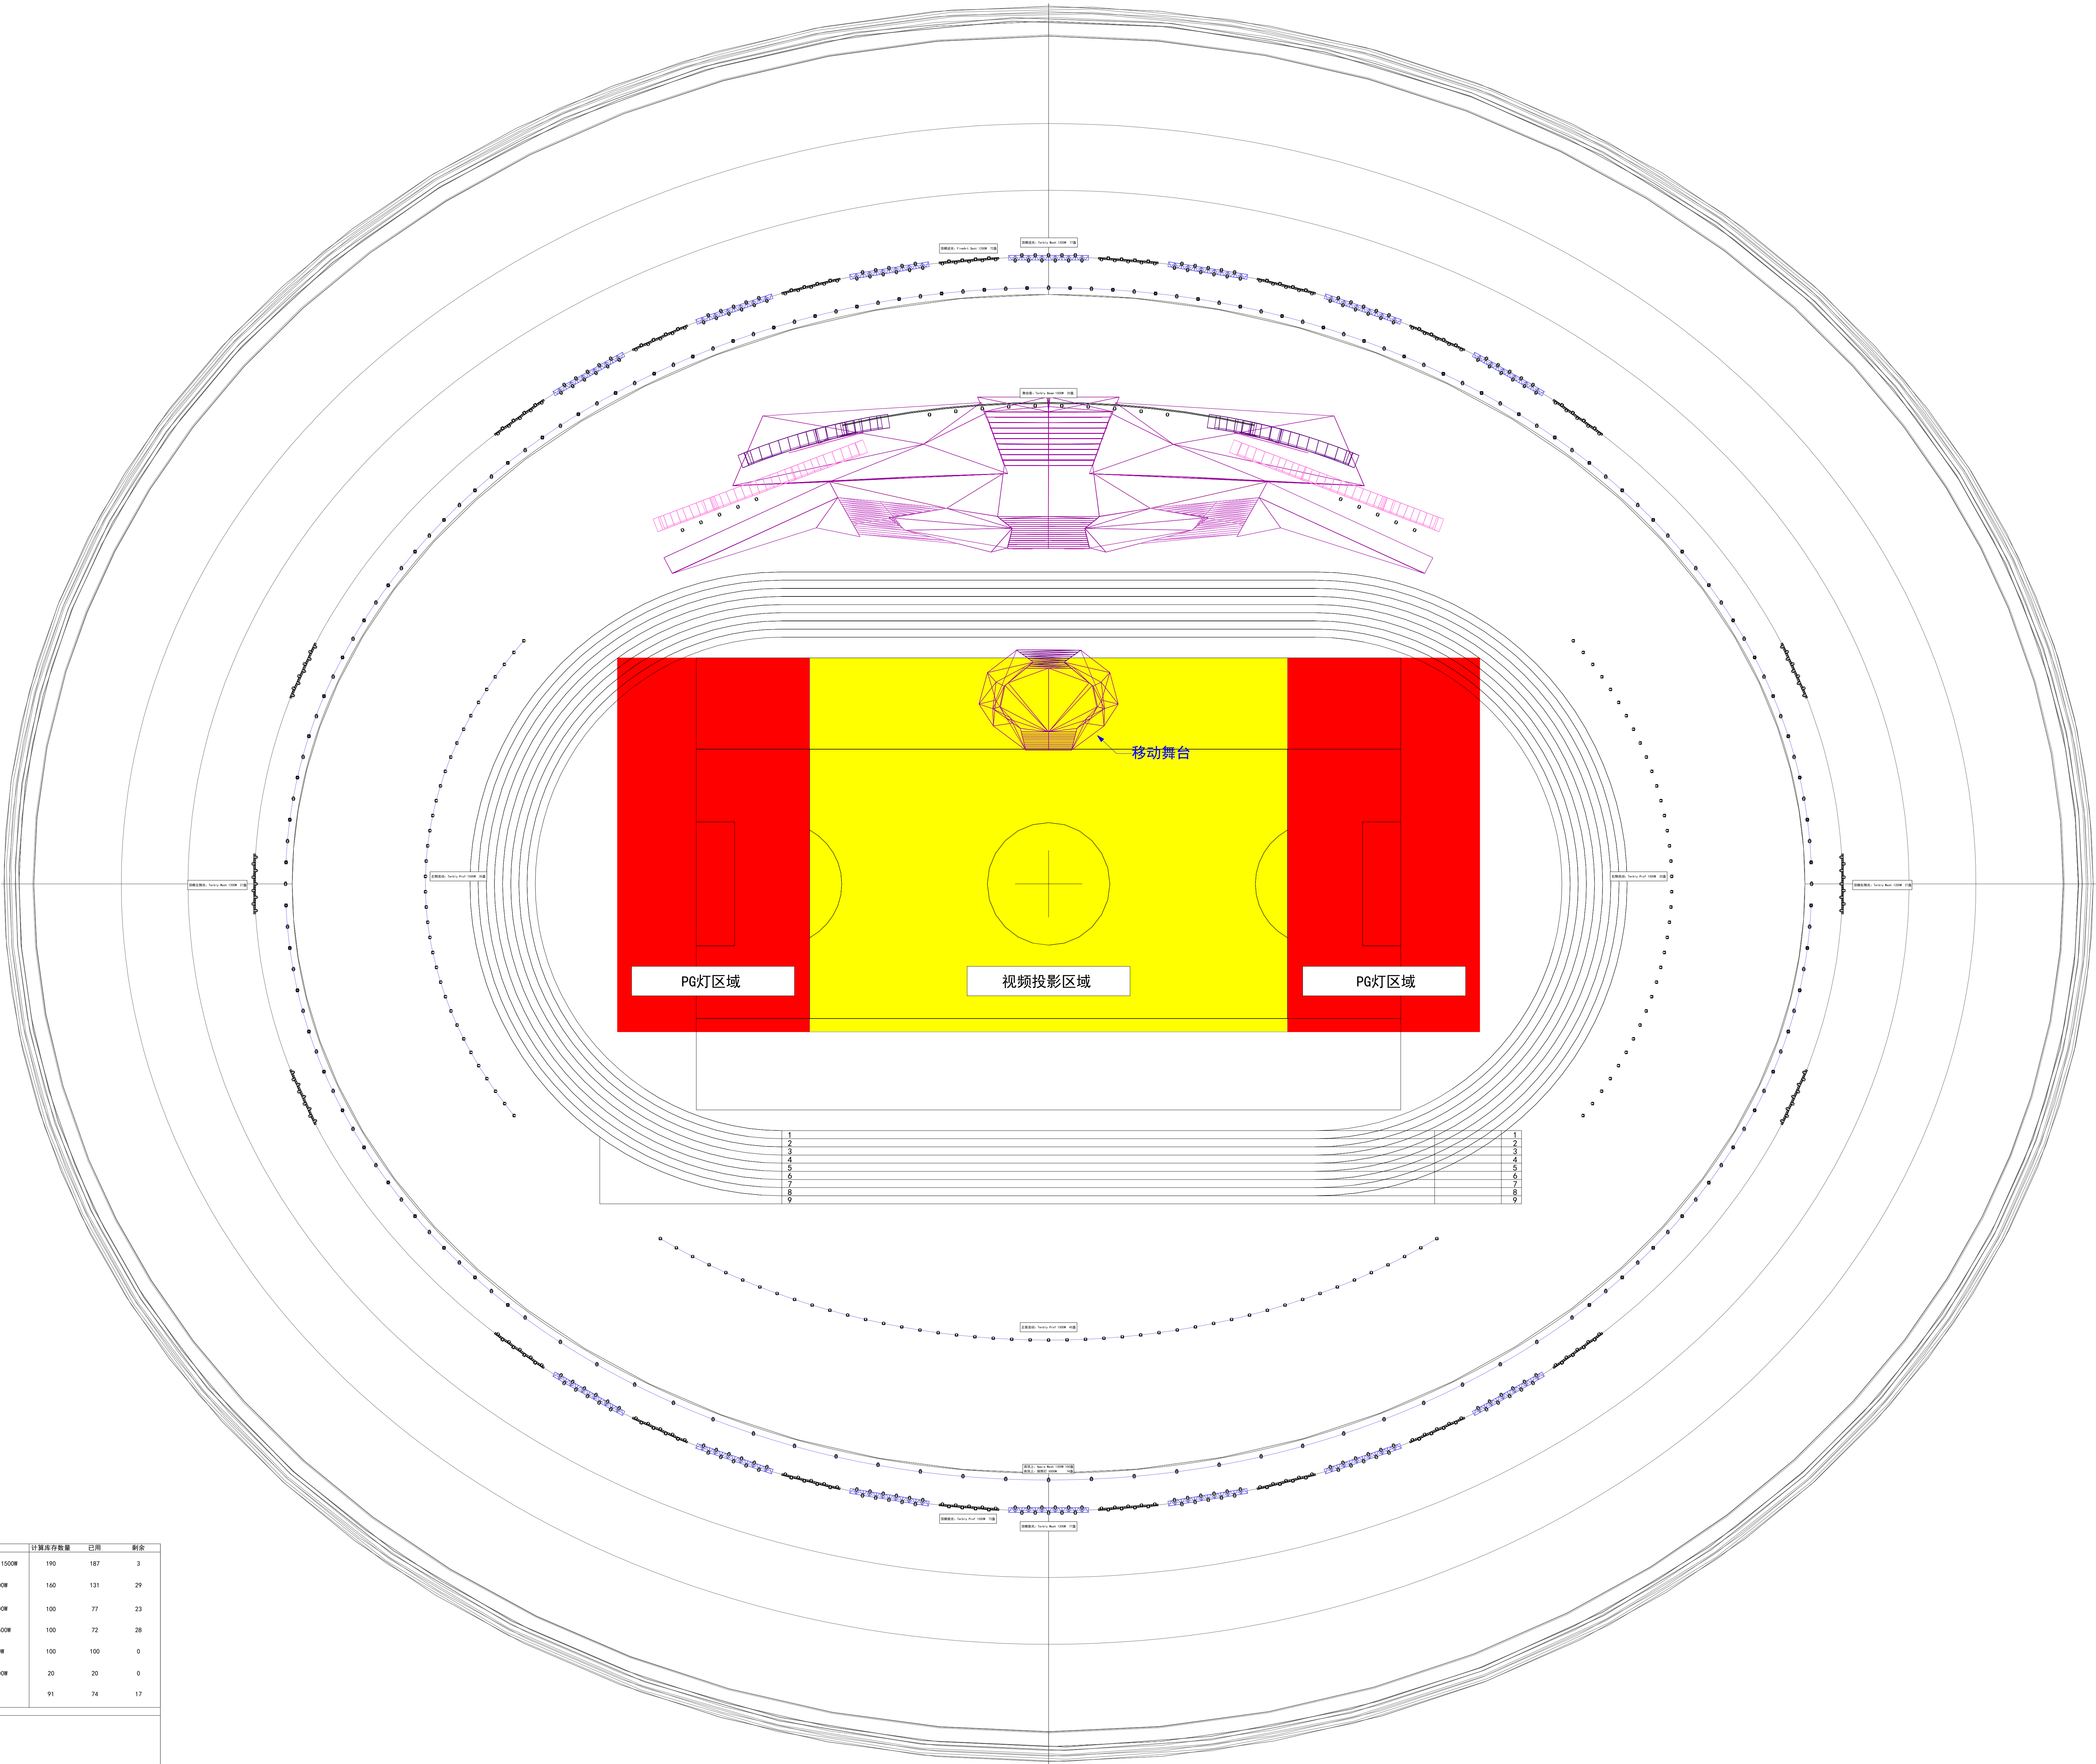

设备	计算原有数量	已用	剩余
● Teribly Profile 1500W	190	187	3
● Teribly Wash 1200W	160	131	29
● Teribly Wash 1500W	100	77	23
● FineArt Spot 1500W	100	72	28
● Apollo Wash 1200W	100	100	0
● Teribly Beam 1500W	20	20	0
● 探照灯 5000W	91	74	17
图例			

图 名：
DRAWING:

总灯位图

审 定：
APPROVED BY:

设 计： 萧 丽 河 (Lea Xiao)
DESIGN BY:

制 图： 裔 仕 敏 (Yi Shi Min)
DRAWN BY:

校 对： 陈 敦 (Chen Dun)
CHECKED BY:

图 号： 1
DWG NO.:

比 例： 日 期: 2013. 9. 30
SCALE: DATE: September. 30. 2013

设计单位：
COMPANY:

上海萧丽河灯光设计有限公司
SHANGHAI LEALIGHTING CO. LTD

上海市静安区华山路620号奥力孚利华大厦7E
620 Hua Shan Rd. Olive Plaza, 7E, Shanghai 200040
Tel.: 86. 21. 5456. 1488 www.lealighting.com