



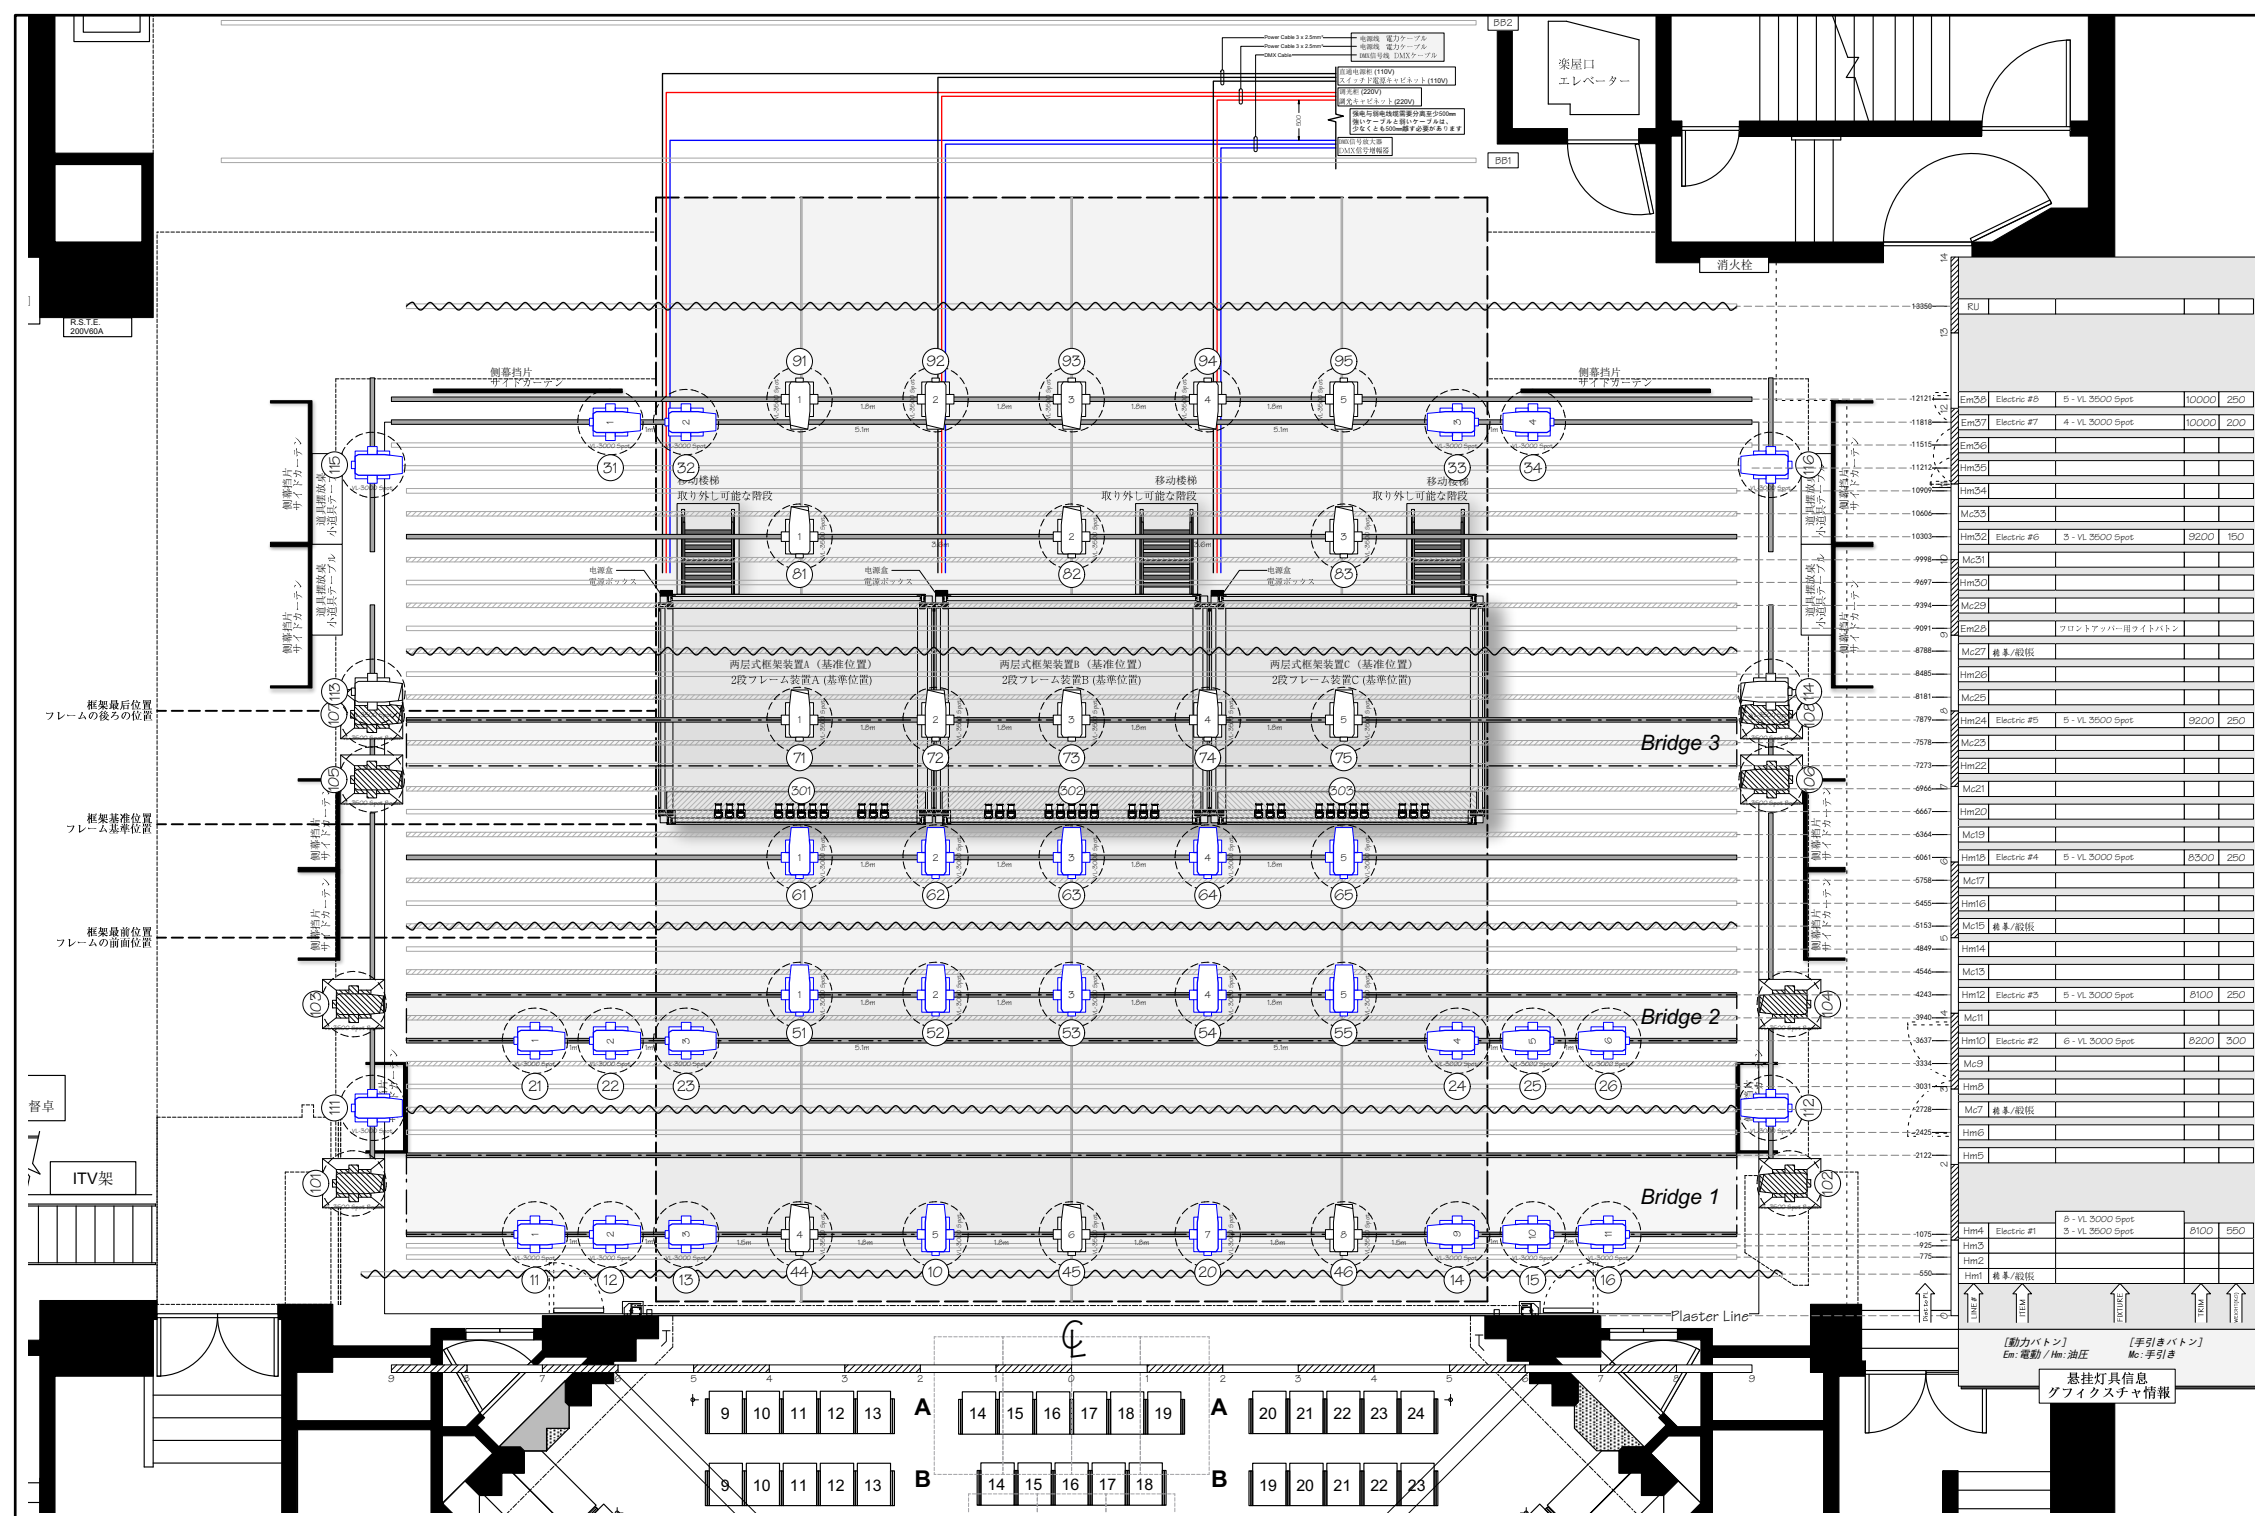

1 舞台区域灯位图 ステージエリアライトプロット
Scale 1:100 / A3

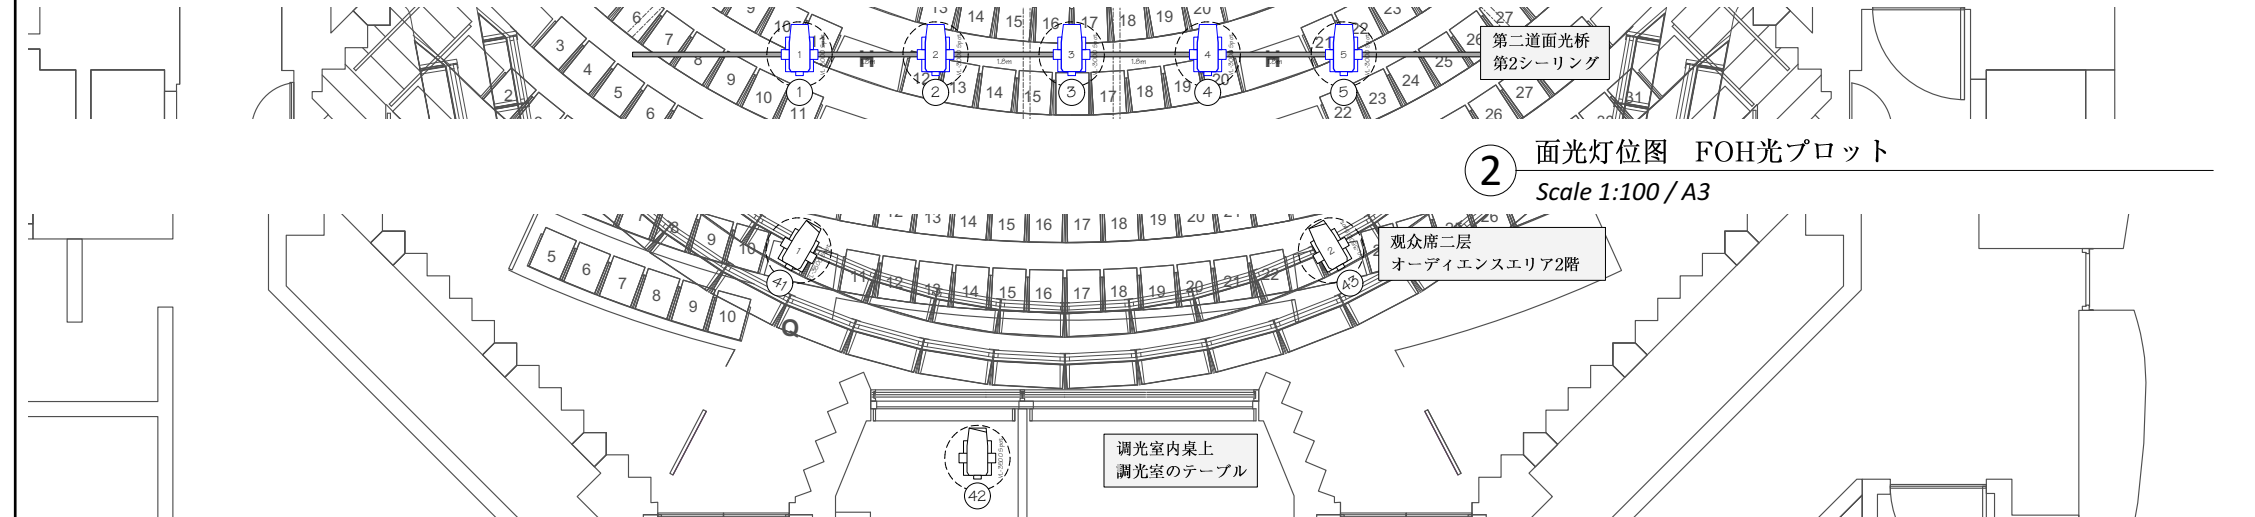


2 面光灯位图 FOH光プロット
Scale 1:100 / A3


3 观众席后区灯位图 講堂のポスターエリア
Scale 1:100 / A3

通用说明 General Notes

图中标注的间距为灯具的中心点到中心点的距离，如下图所示
図中の距離は、下図のようにランプの中心点から中心点までの距離です

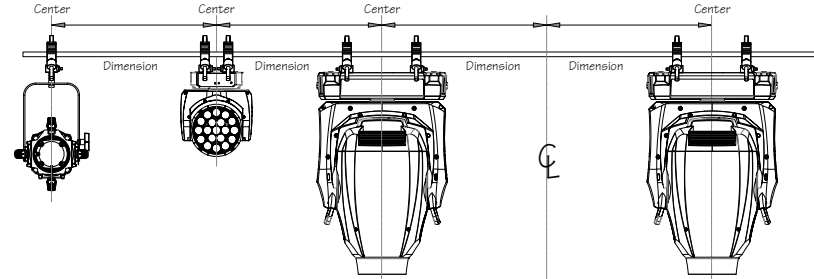

图例 Key & Legend

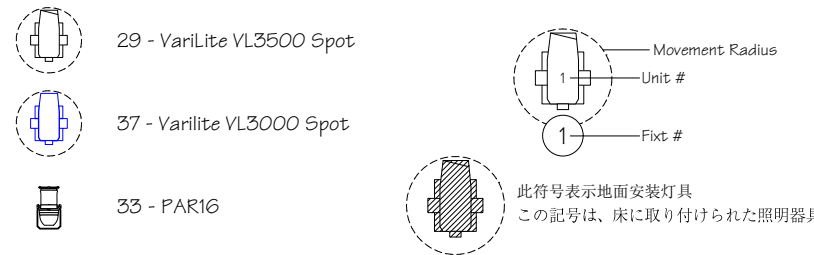


两层式框架装置内灯具
2段フレーム装置内側のライト

内置LED-RGBW灯带共90米
合計90mの内蔵LED-RGBWランプ
一樓天花下安裝PAR-16共33台
1階の天井には合計33台のPAR-16
が設置されています


正视图/正面図
Not to scale

舞台细节
ステージ詳細

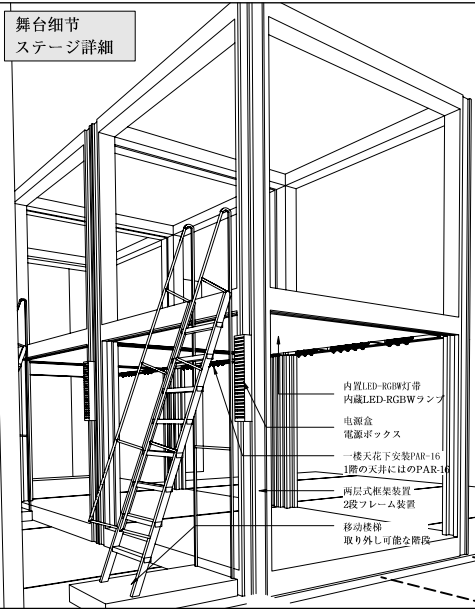

流动电脑灯安装方法
地上照明の設置方法

灯具高度约离地850mm
(Fixture 105-108灯具离地高度为1.7m)
ランプの高さは地面から約850mmです
(105-108照明器具の高さは1.7mです)

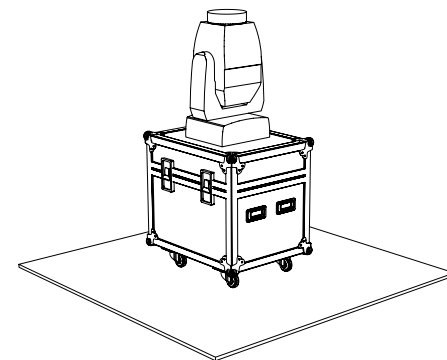

7	舞台完成后調整	2018-10-5
6	調整了側幕片の尺寸和位置	2018-9-8
5	調整了灯具和格幕位置	2018-7-29
4	更新了灯光吊杆	2018-7-27
3	重新分配灯具数量	2018-7-22
2	更新舞美方案、修改灯型	2018-7-16
1	初稿	2018-6-9
修正 REV	修正内容 REVISION CONTENT	日期 DATE

导演 DIRECTED BY: 田沁鑫
Tian Qin Xin

舞台设计 SCENERY BY: 沈力
Shen Li

灯光设计 LIGHTING BY: 谭华
Tan Hua

日本东京世田谷公共剧场(主剧场)
世田谷パブリックシアター (主劇場)
演出时间 2018-10-6

灯位图
照明のレイアウト


比例 SCALE 1:100

日期 DATE 2018-10-5


制图 DRAWN 喬仕敏
Elvis Yi

Original Sheet Size | 原稿図紙大小・A3

カーテンの特定の高さは、照明設計によって決定される。

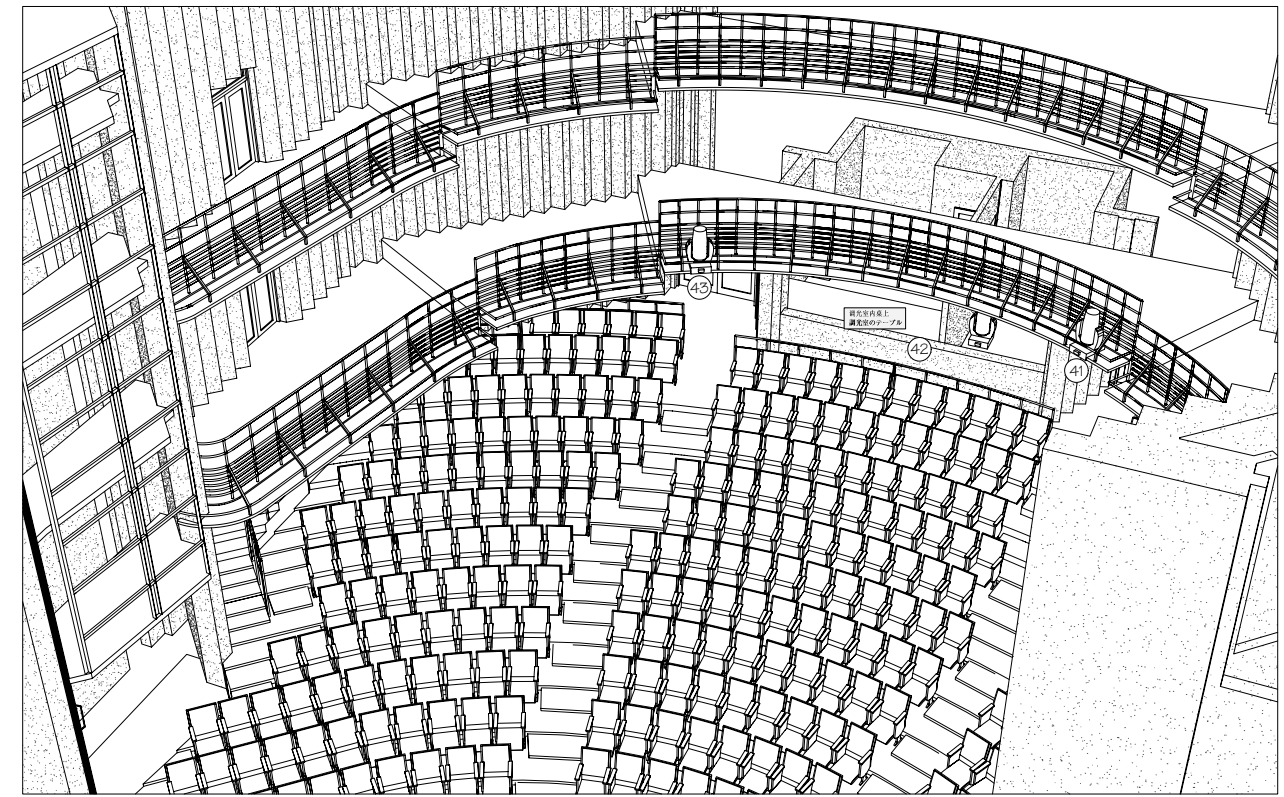

2 观众席灯位安装细节 オーディトリウム照明の設置の詳細
Not to scale

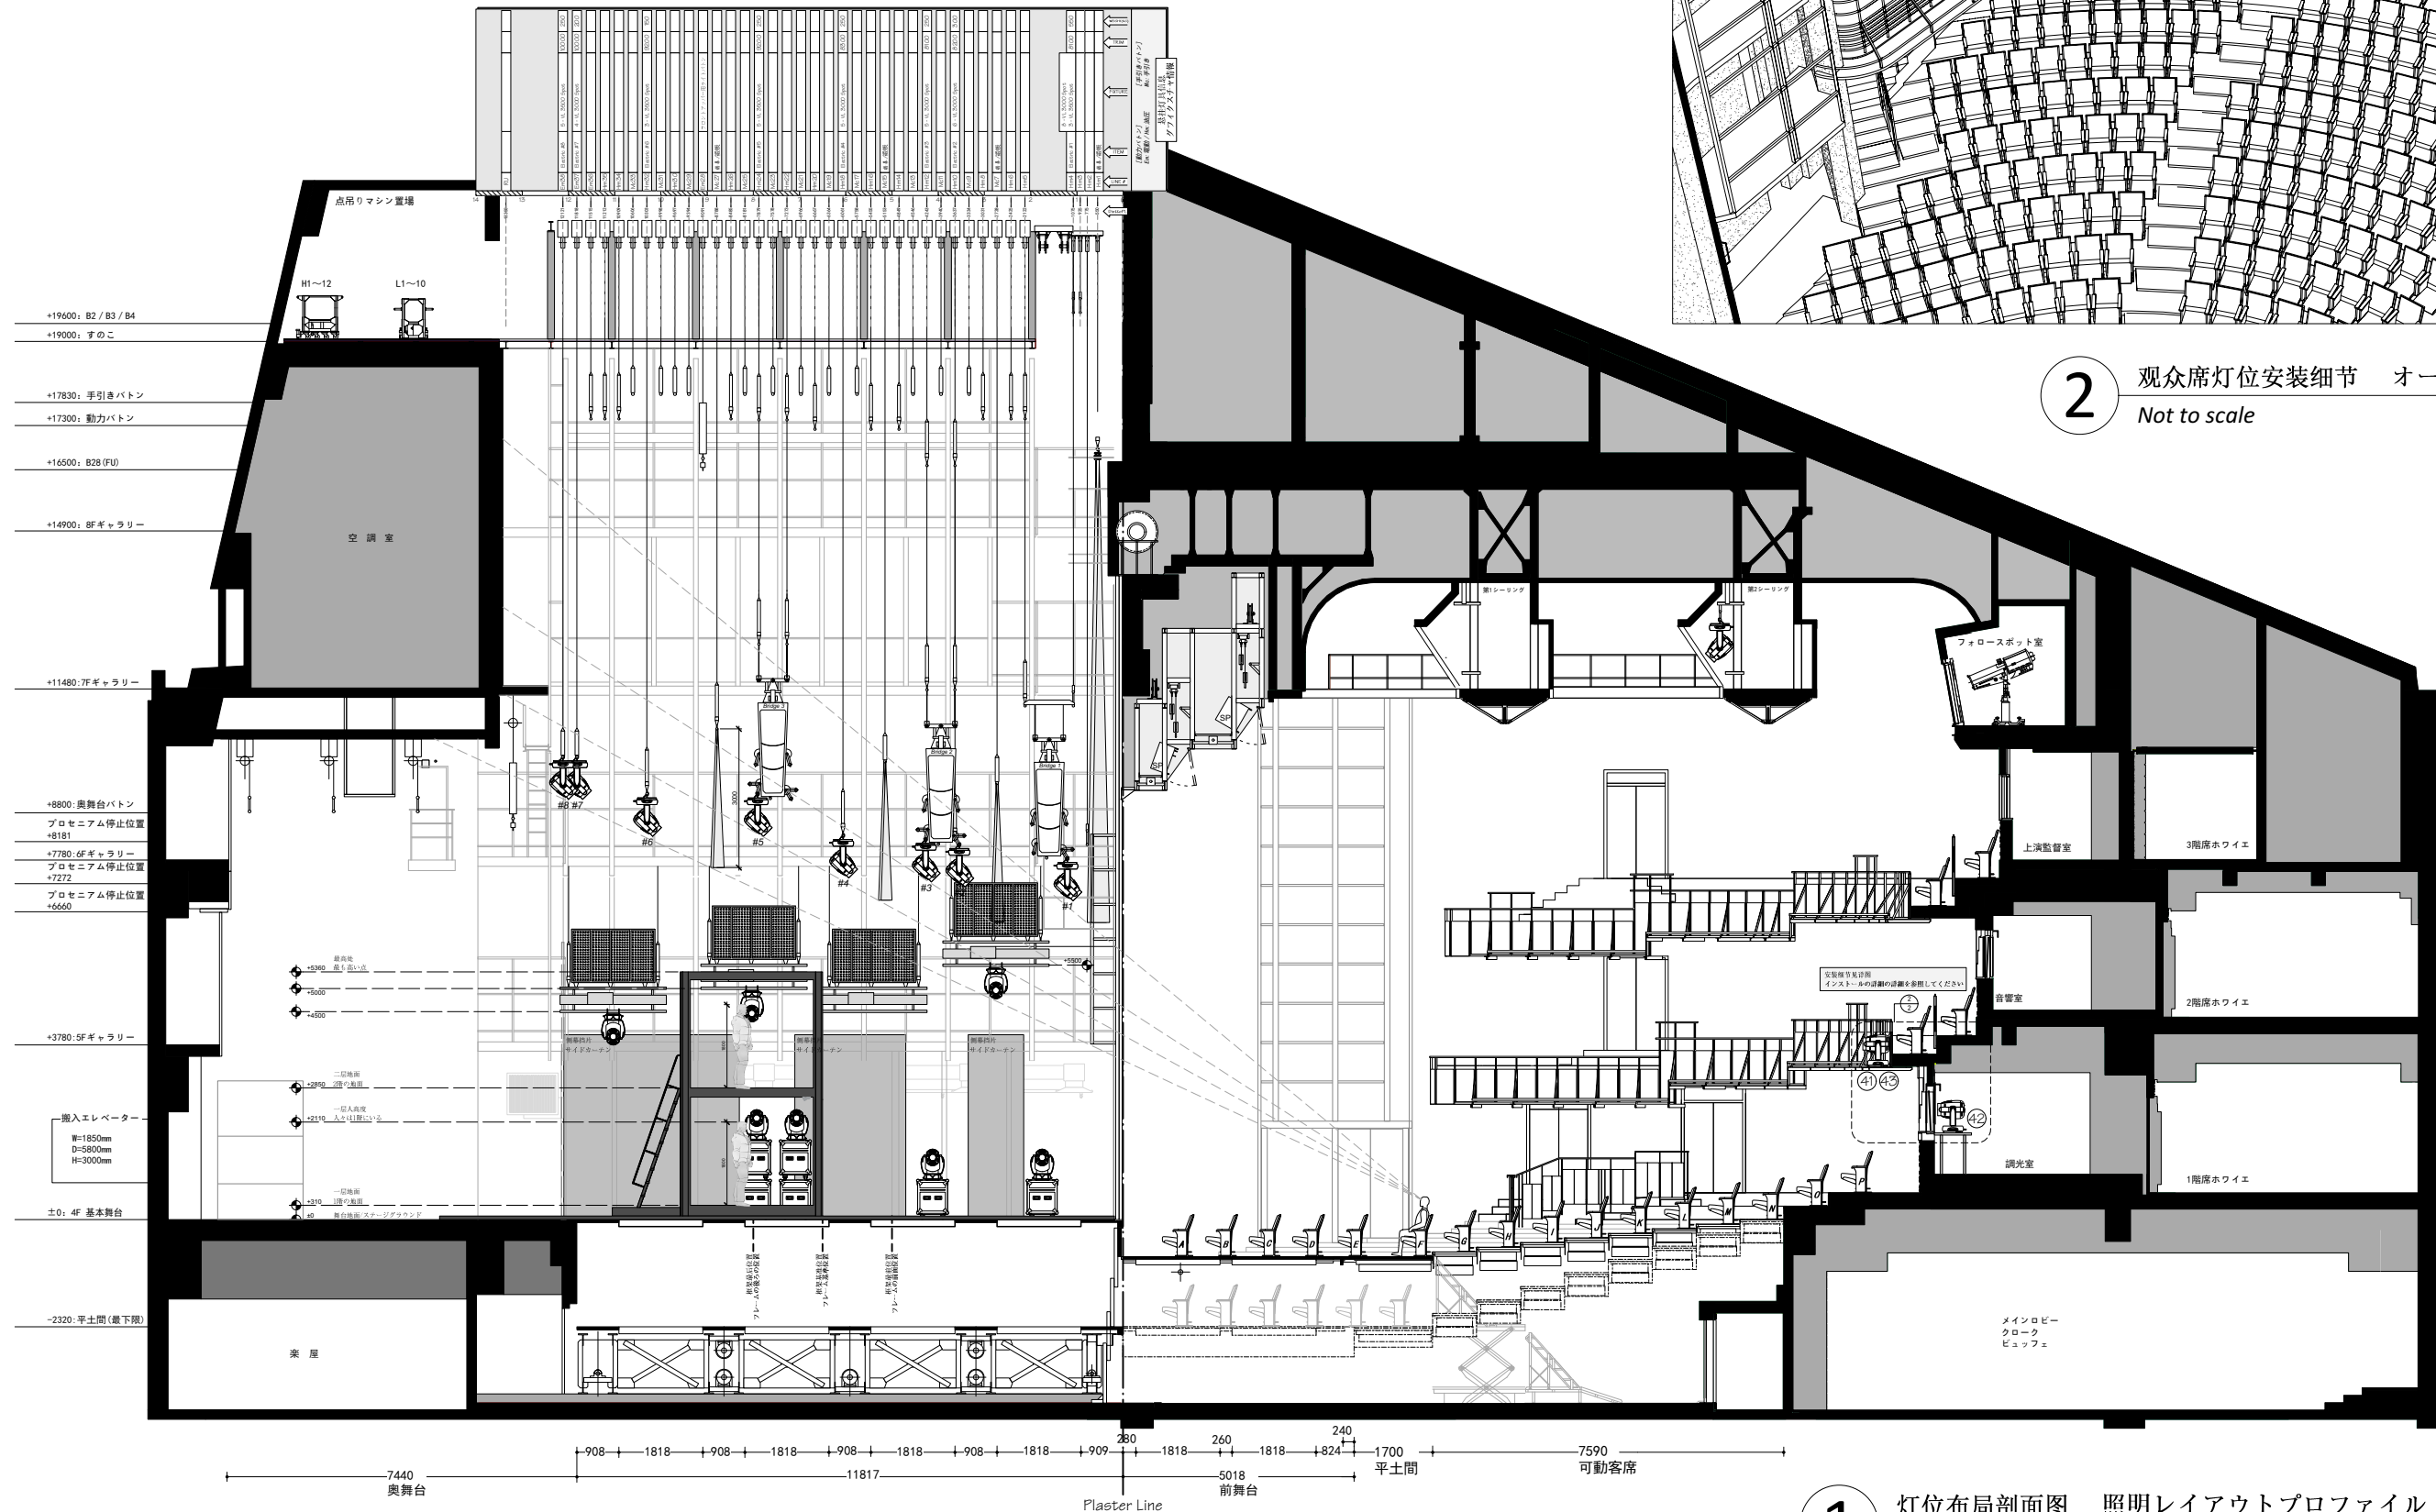

7	舞台完成后调整	2018-10-5
6	调整了侧幕挑片的尺寸和位置	2018-9-8
5	调整了灯具和转幕位置	2018-7-29
4	更新了灯光吊杆	2018-7-27
3	重新分配灯具数量	2018-7-22
2	更新布景方案, 修改灯型	2018-7-16
1	初稿	2018-6-9
修正 REV	修正内容 REVISION CONTENT	日期 DATE

	导演	田沁鑫
	DIRECTED BY:	Tian Qin Xin
	舞台设计	沈力
	SCENERY BY:	Shen Li
	灯光设计	谭华
	LIGHTING BY:	Tan Hua

日本東京世田谷公共劇場(主劇場)
世田谷パブリックシアター (主劇場)
演出時間 2018-10-6

灯位剖面图
照明レイアウトプロファイル

比例 SCALE	1:100	
日期 DATE	2018-10-5	2 of 2
制图 DRAWN	肖仕敏 Elvis Yi	
Original Sheet Size		原始图纸大小 • A3