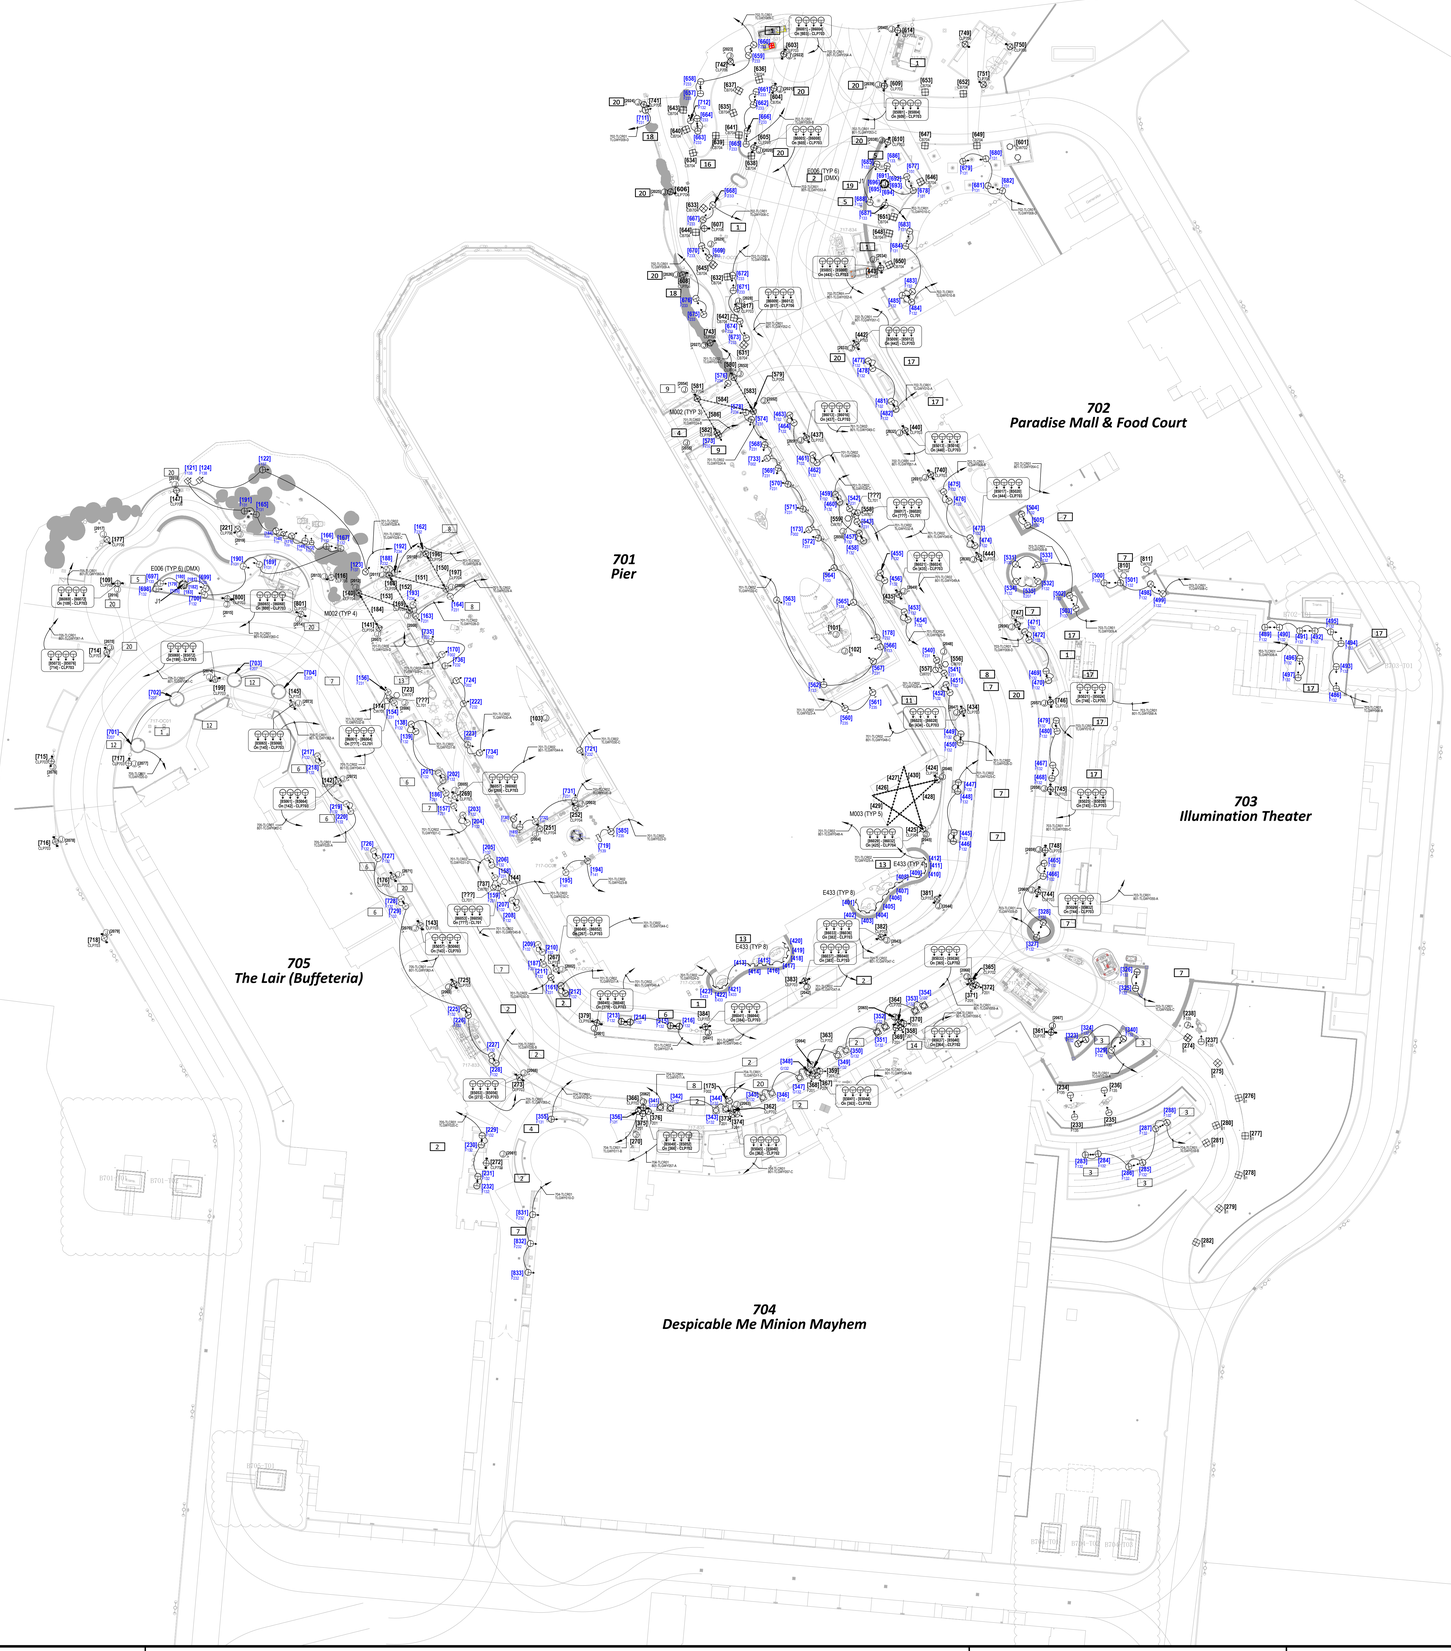

Universal Beijing Resort	717 - Minion Land 700 - Area Development	Plan View - Themed Lighting	Lighting Control	For JV/GC coordination	Drawn: Elvis.Yi Recent Update: 2021-05-25