




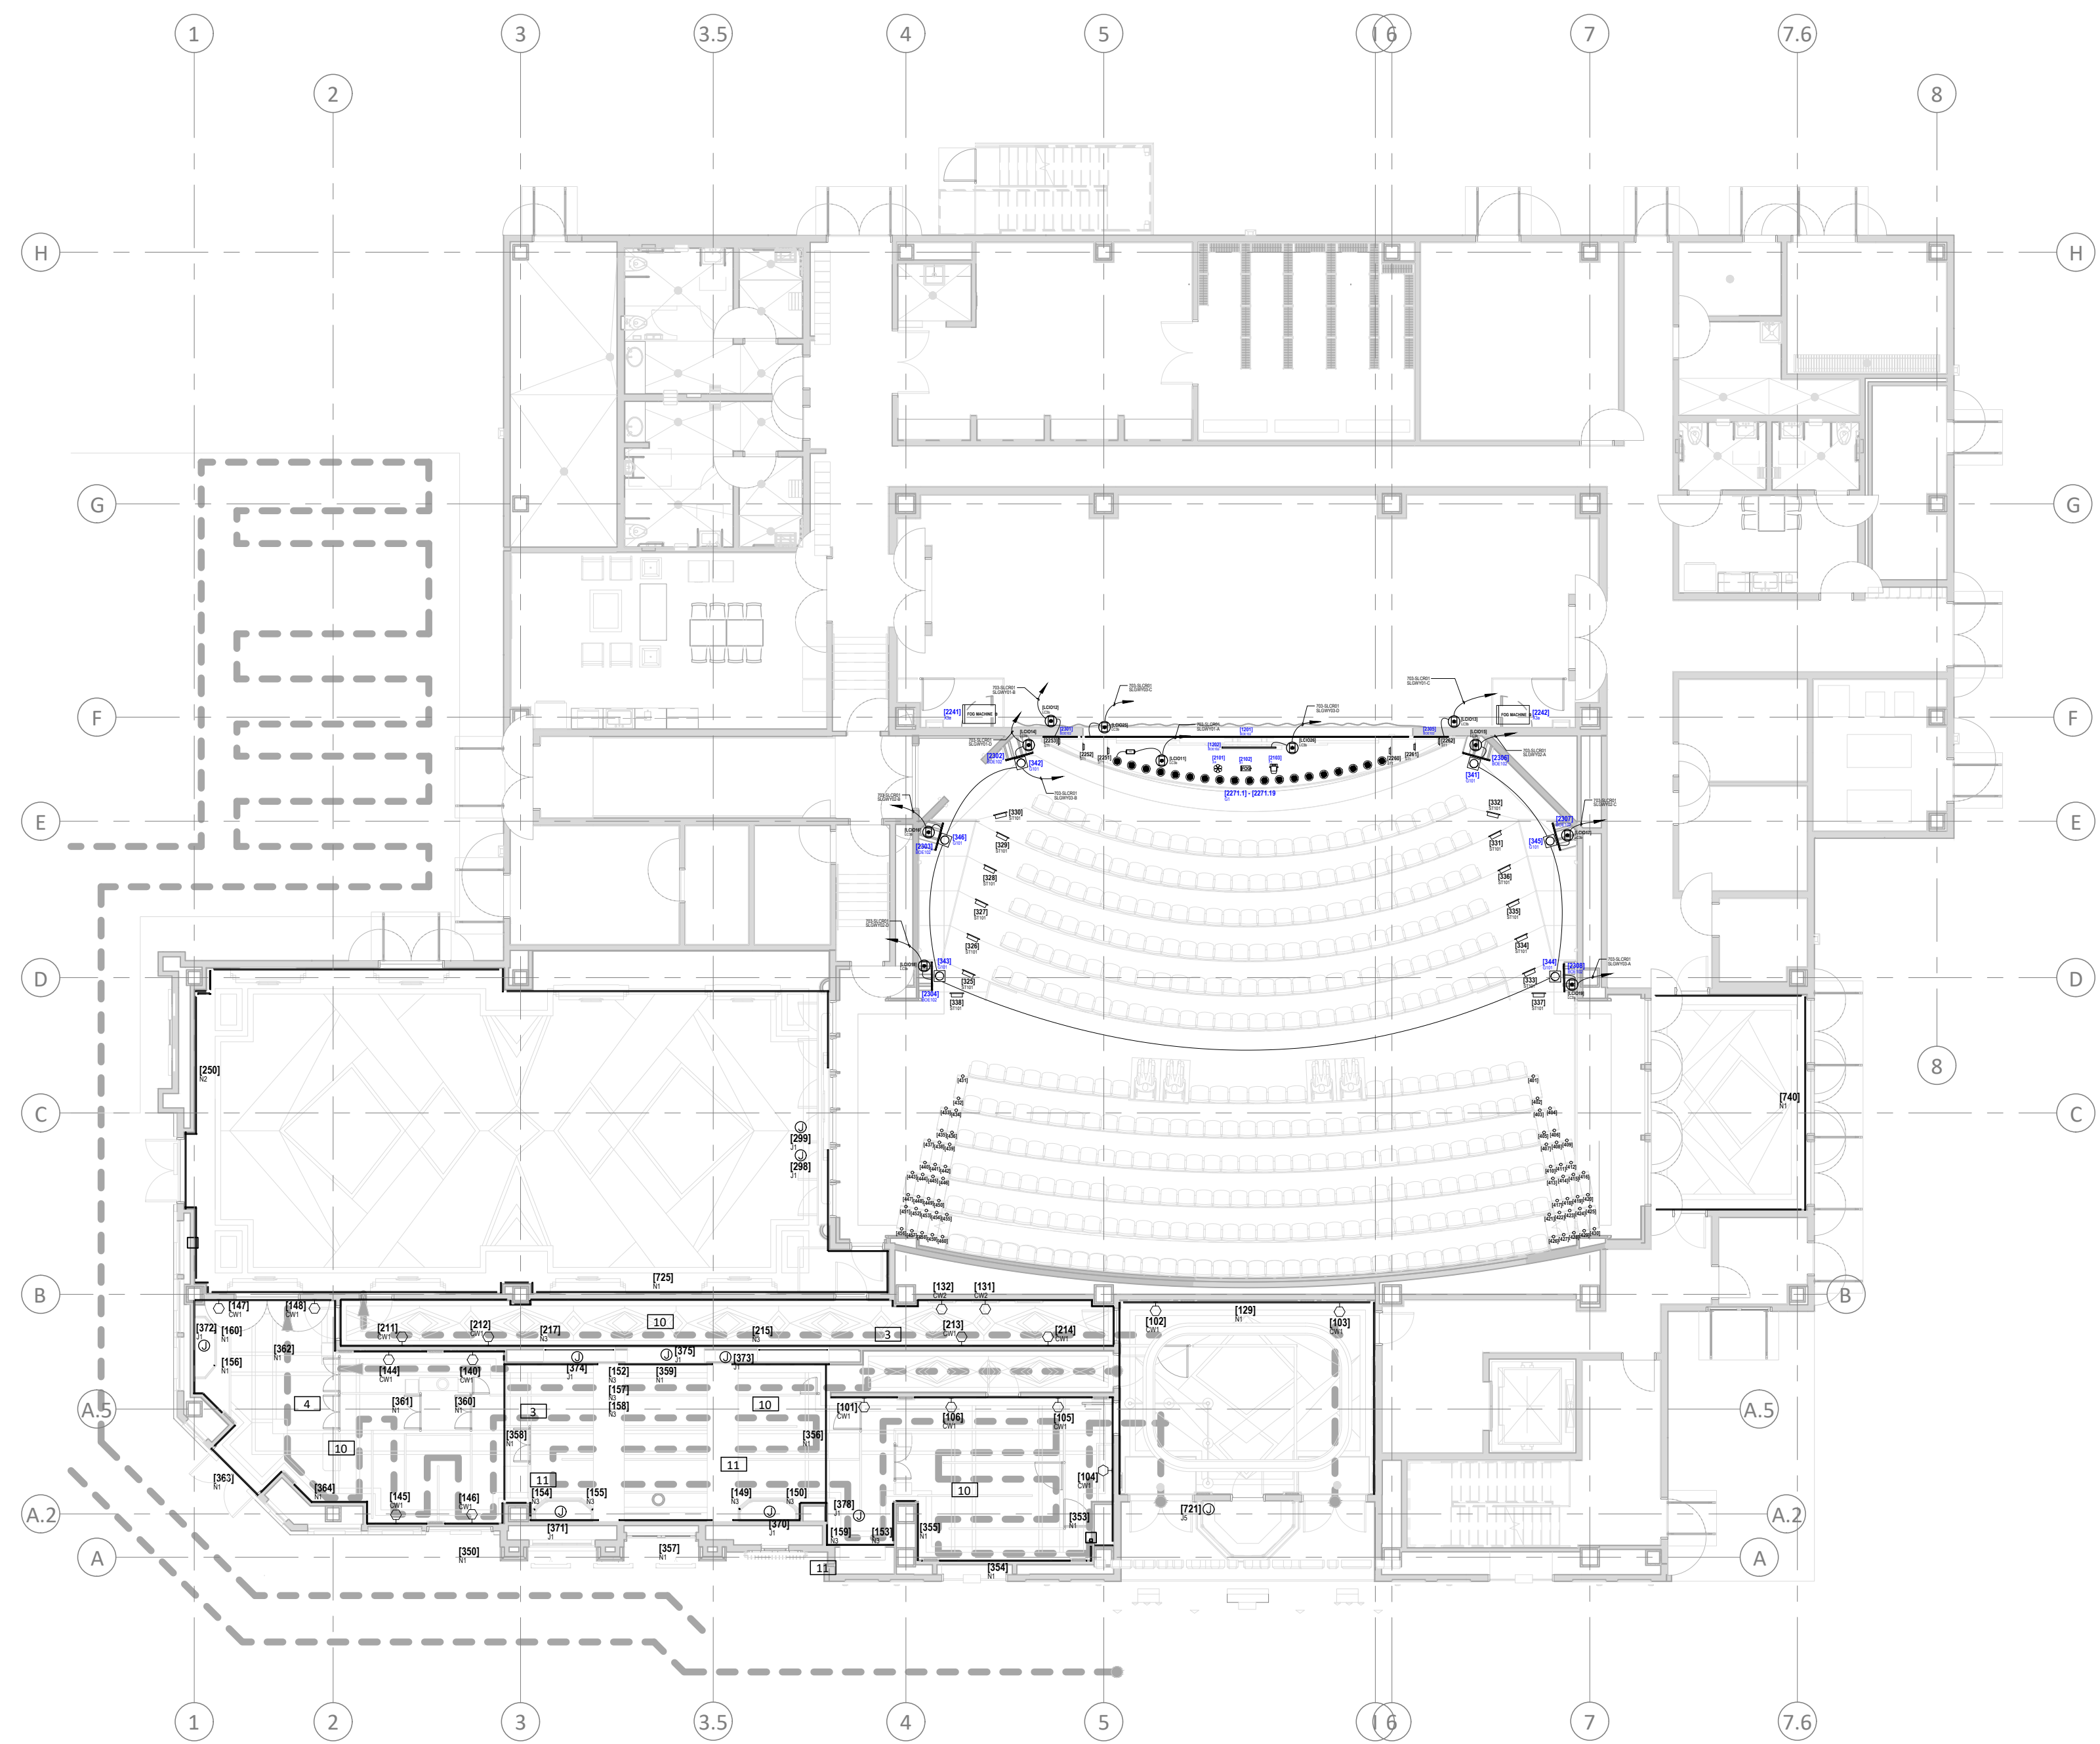


首层平面图 - 主题灯光
1 FLOOR PLAN - THEMED LIGHTING
TL122f

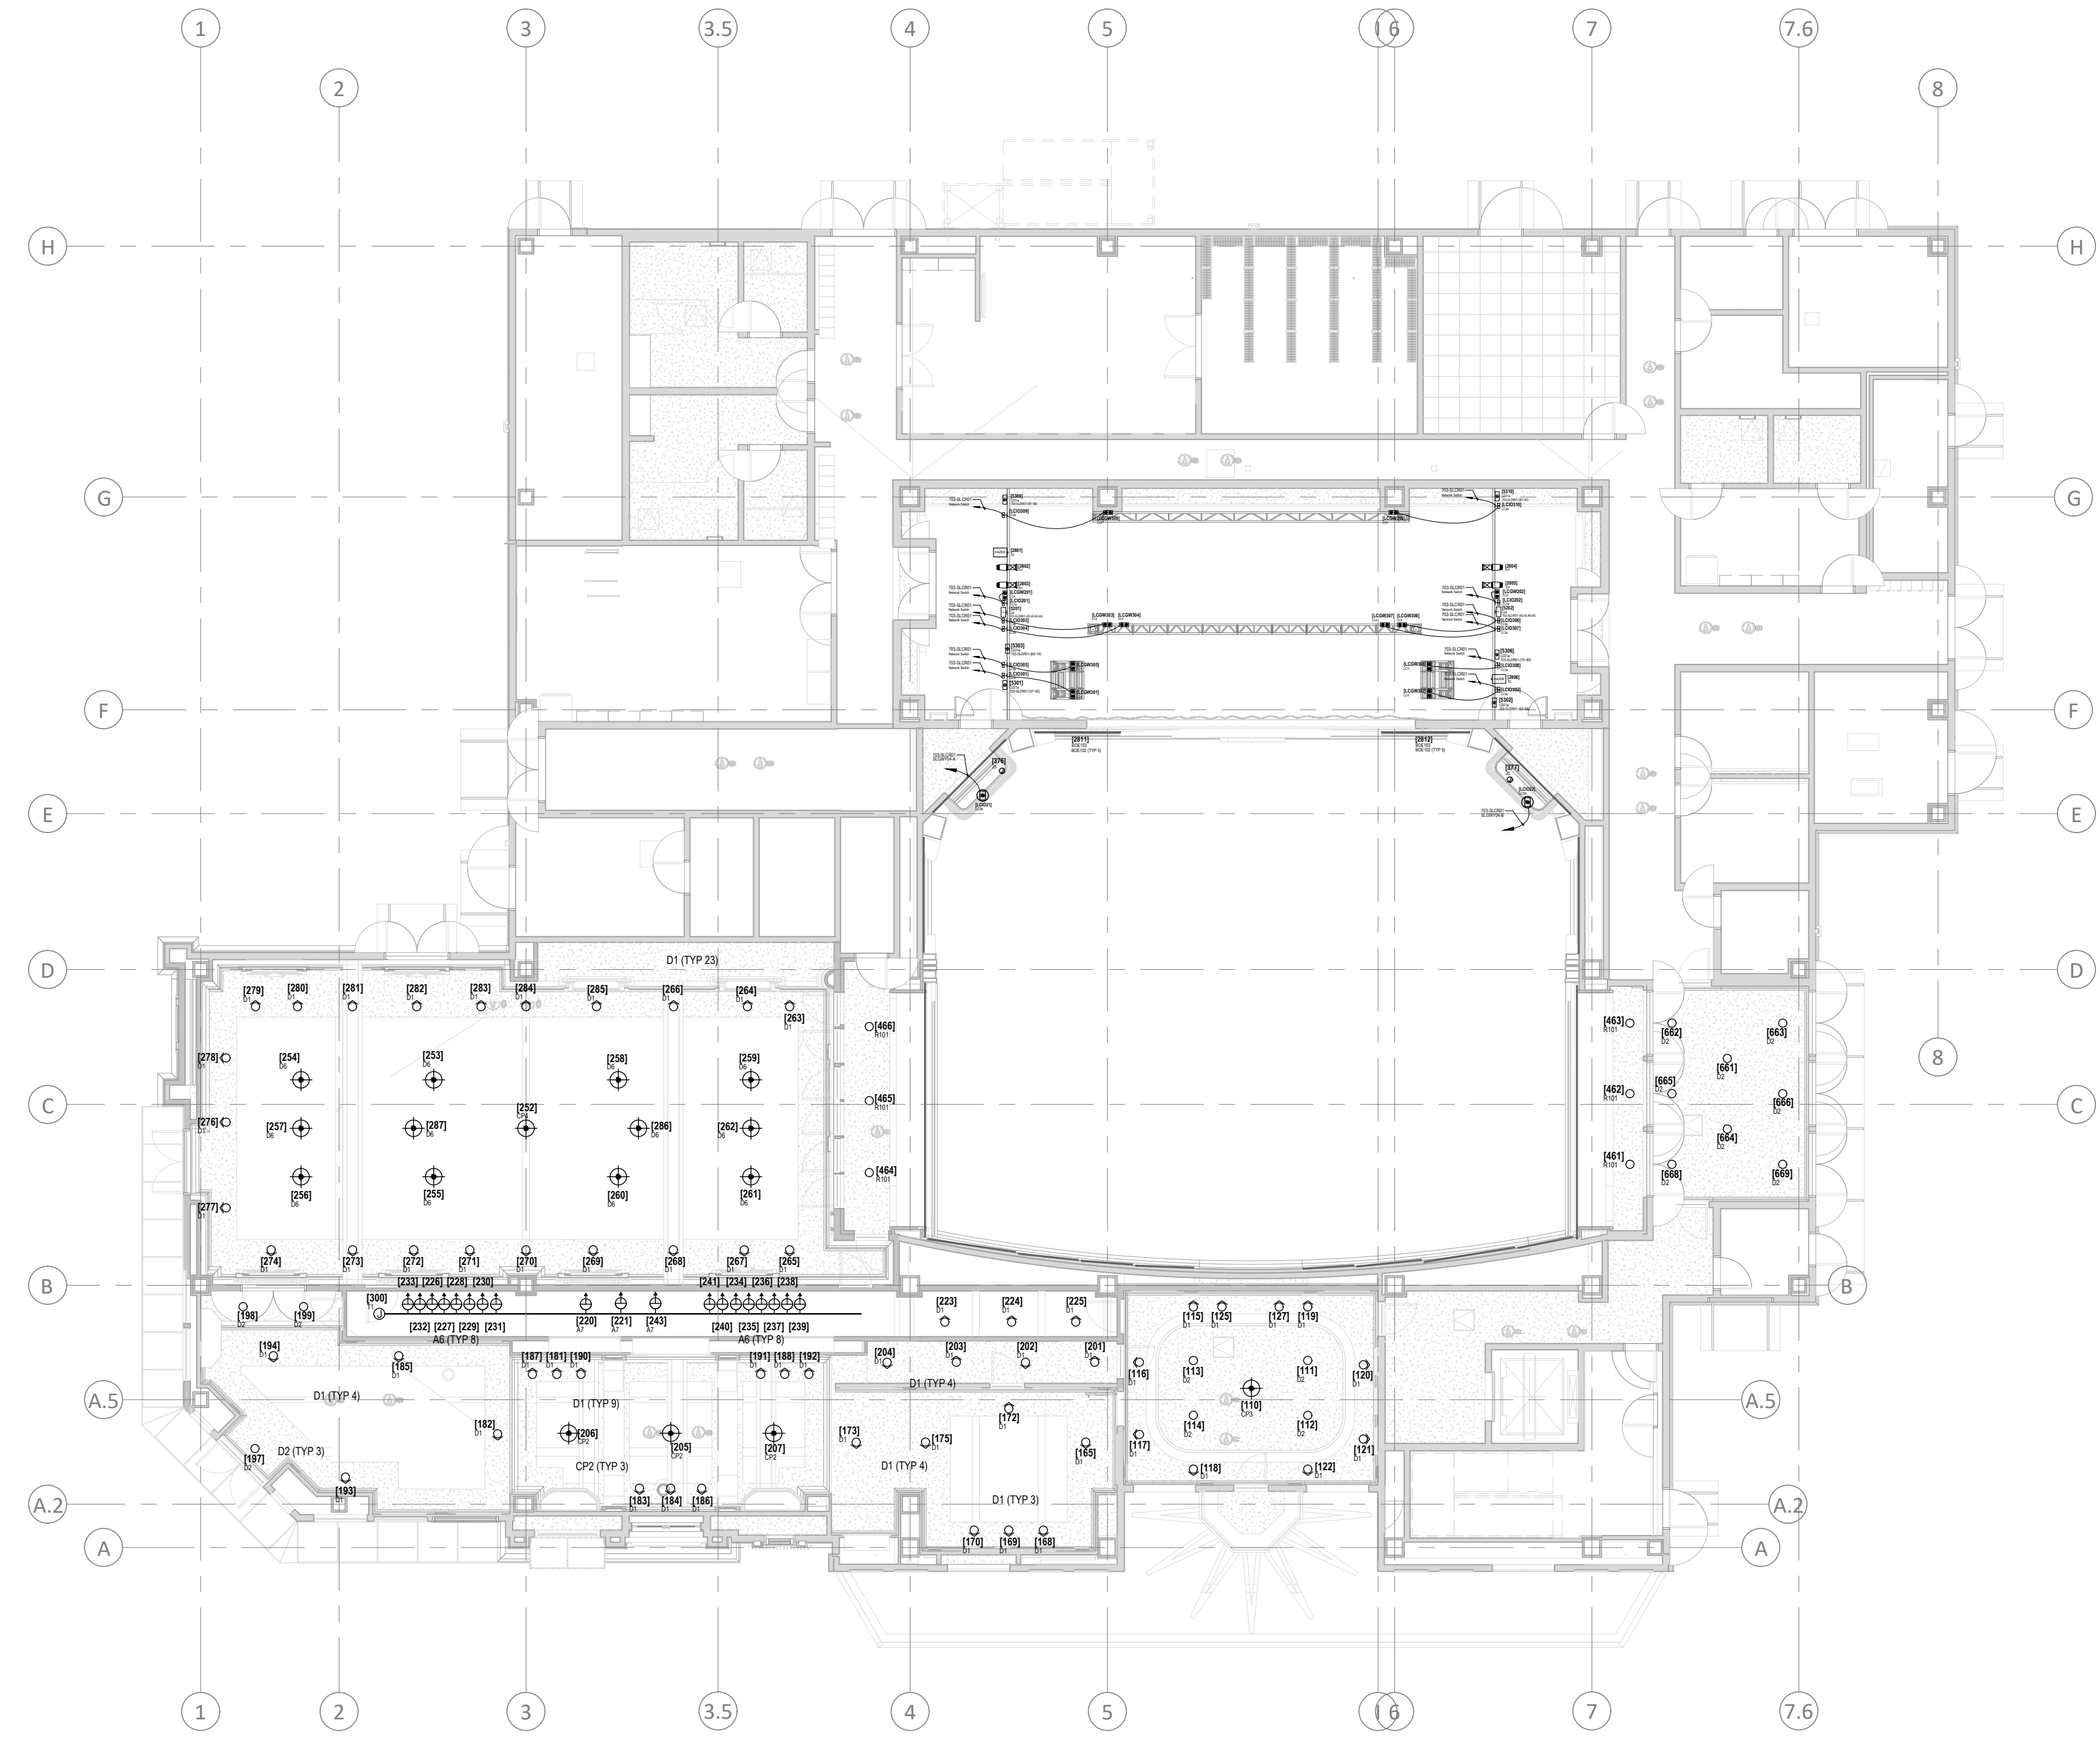


天花平面图-主题灯光
2 CEILING PLAN - THEMED LIGHTING
TL131b

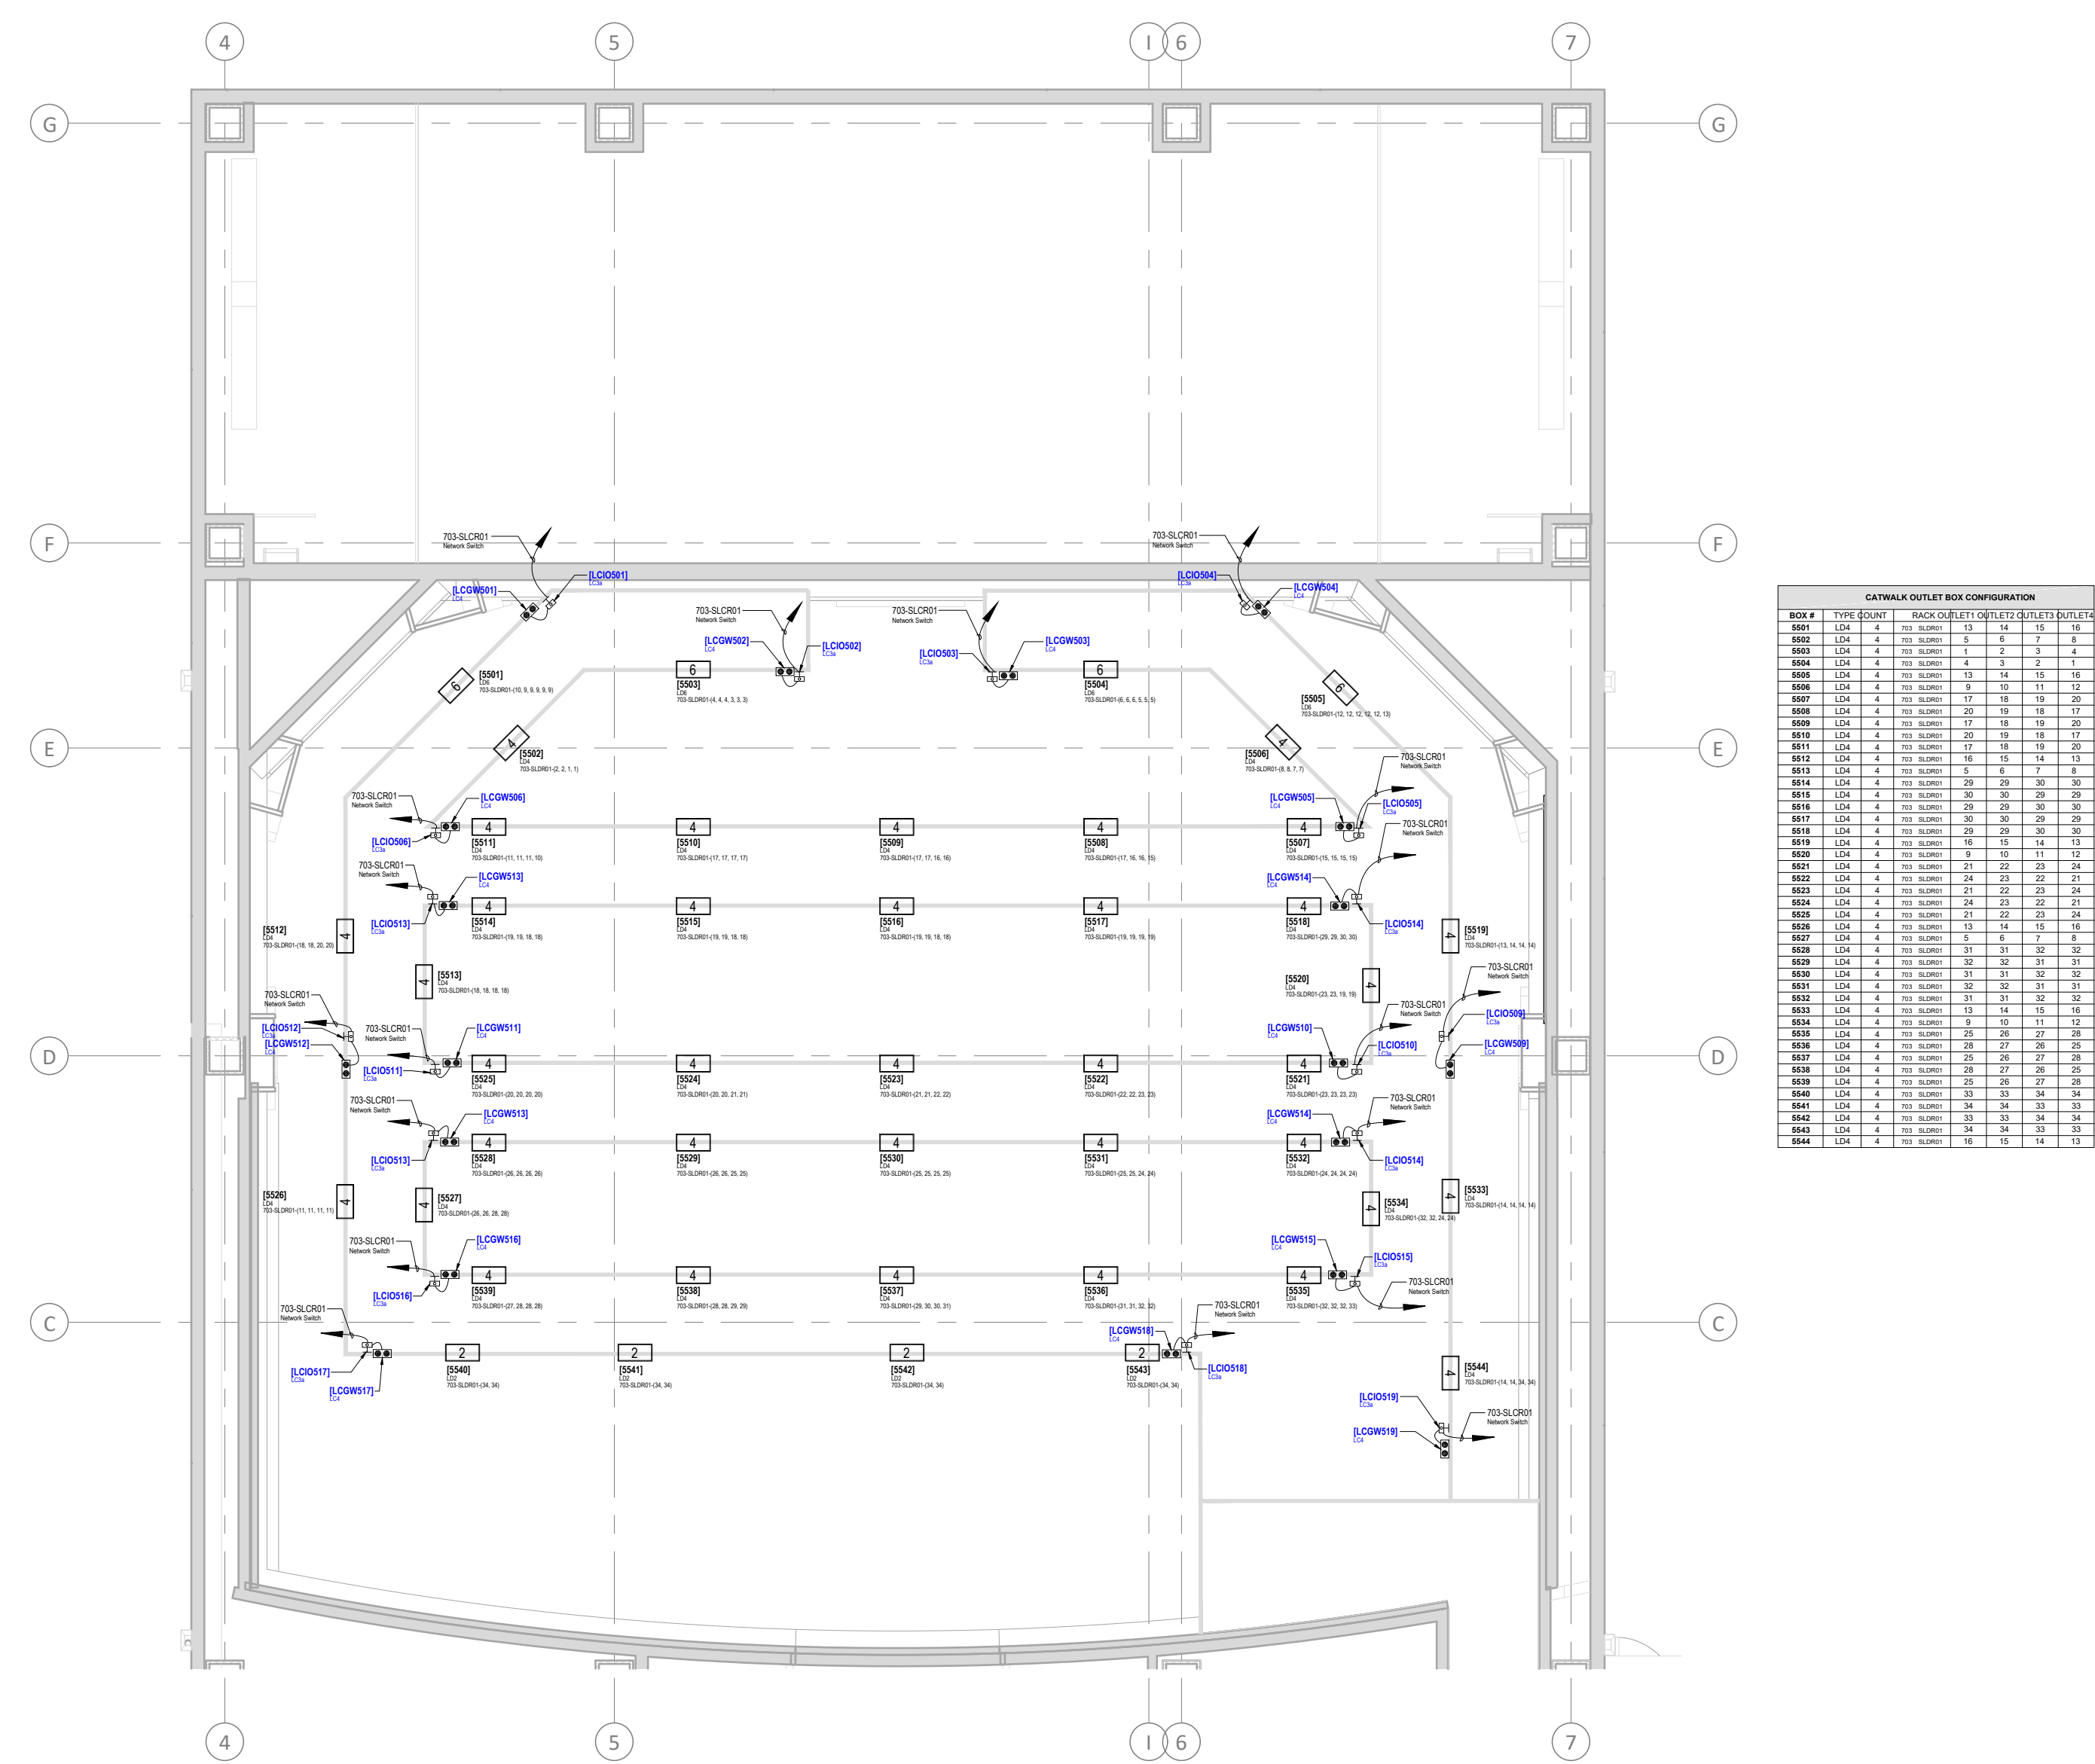

马道平面图 - 主题灯光
3 CATWALK PLAN - THEMED LIGHTING
TL131f

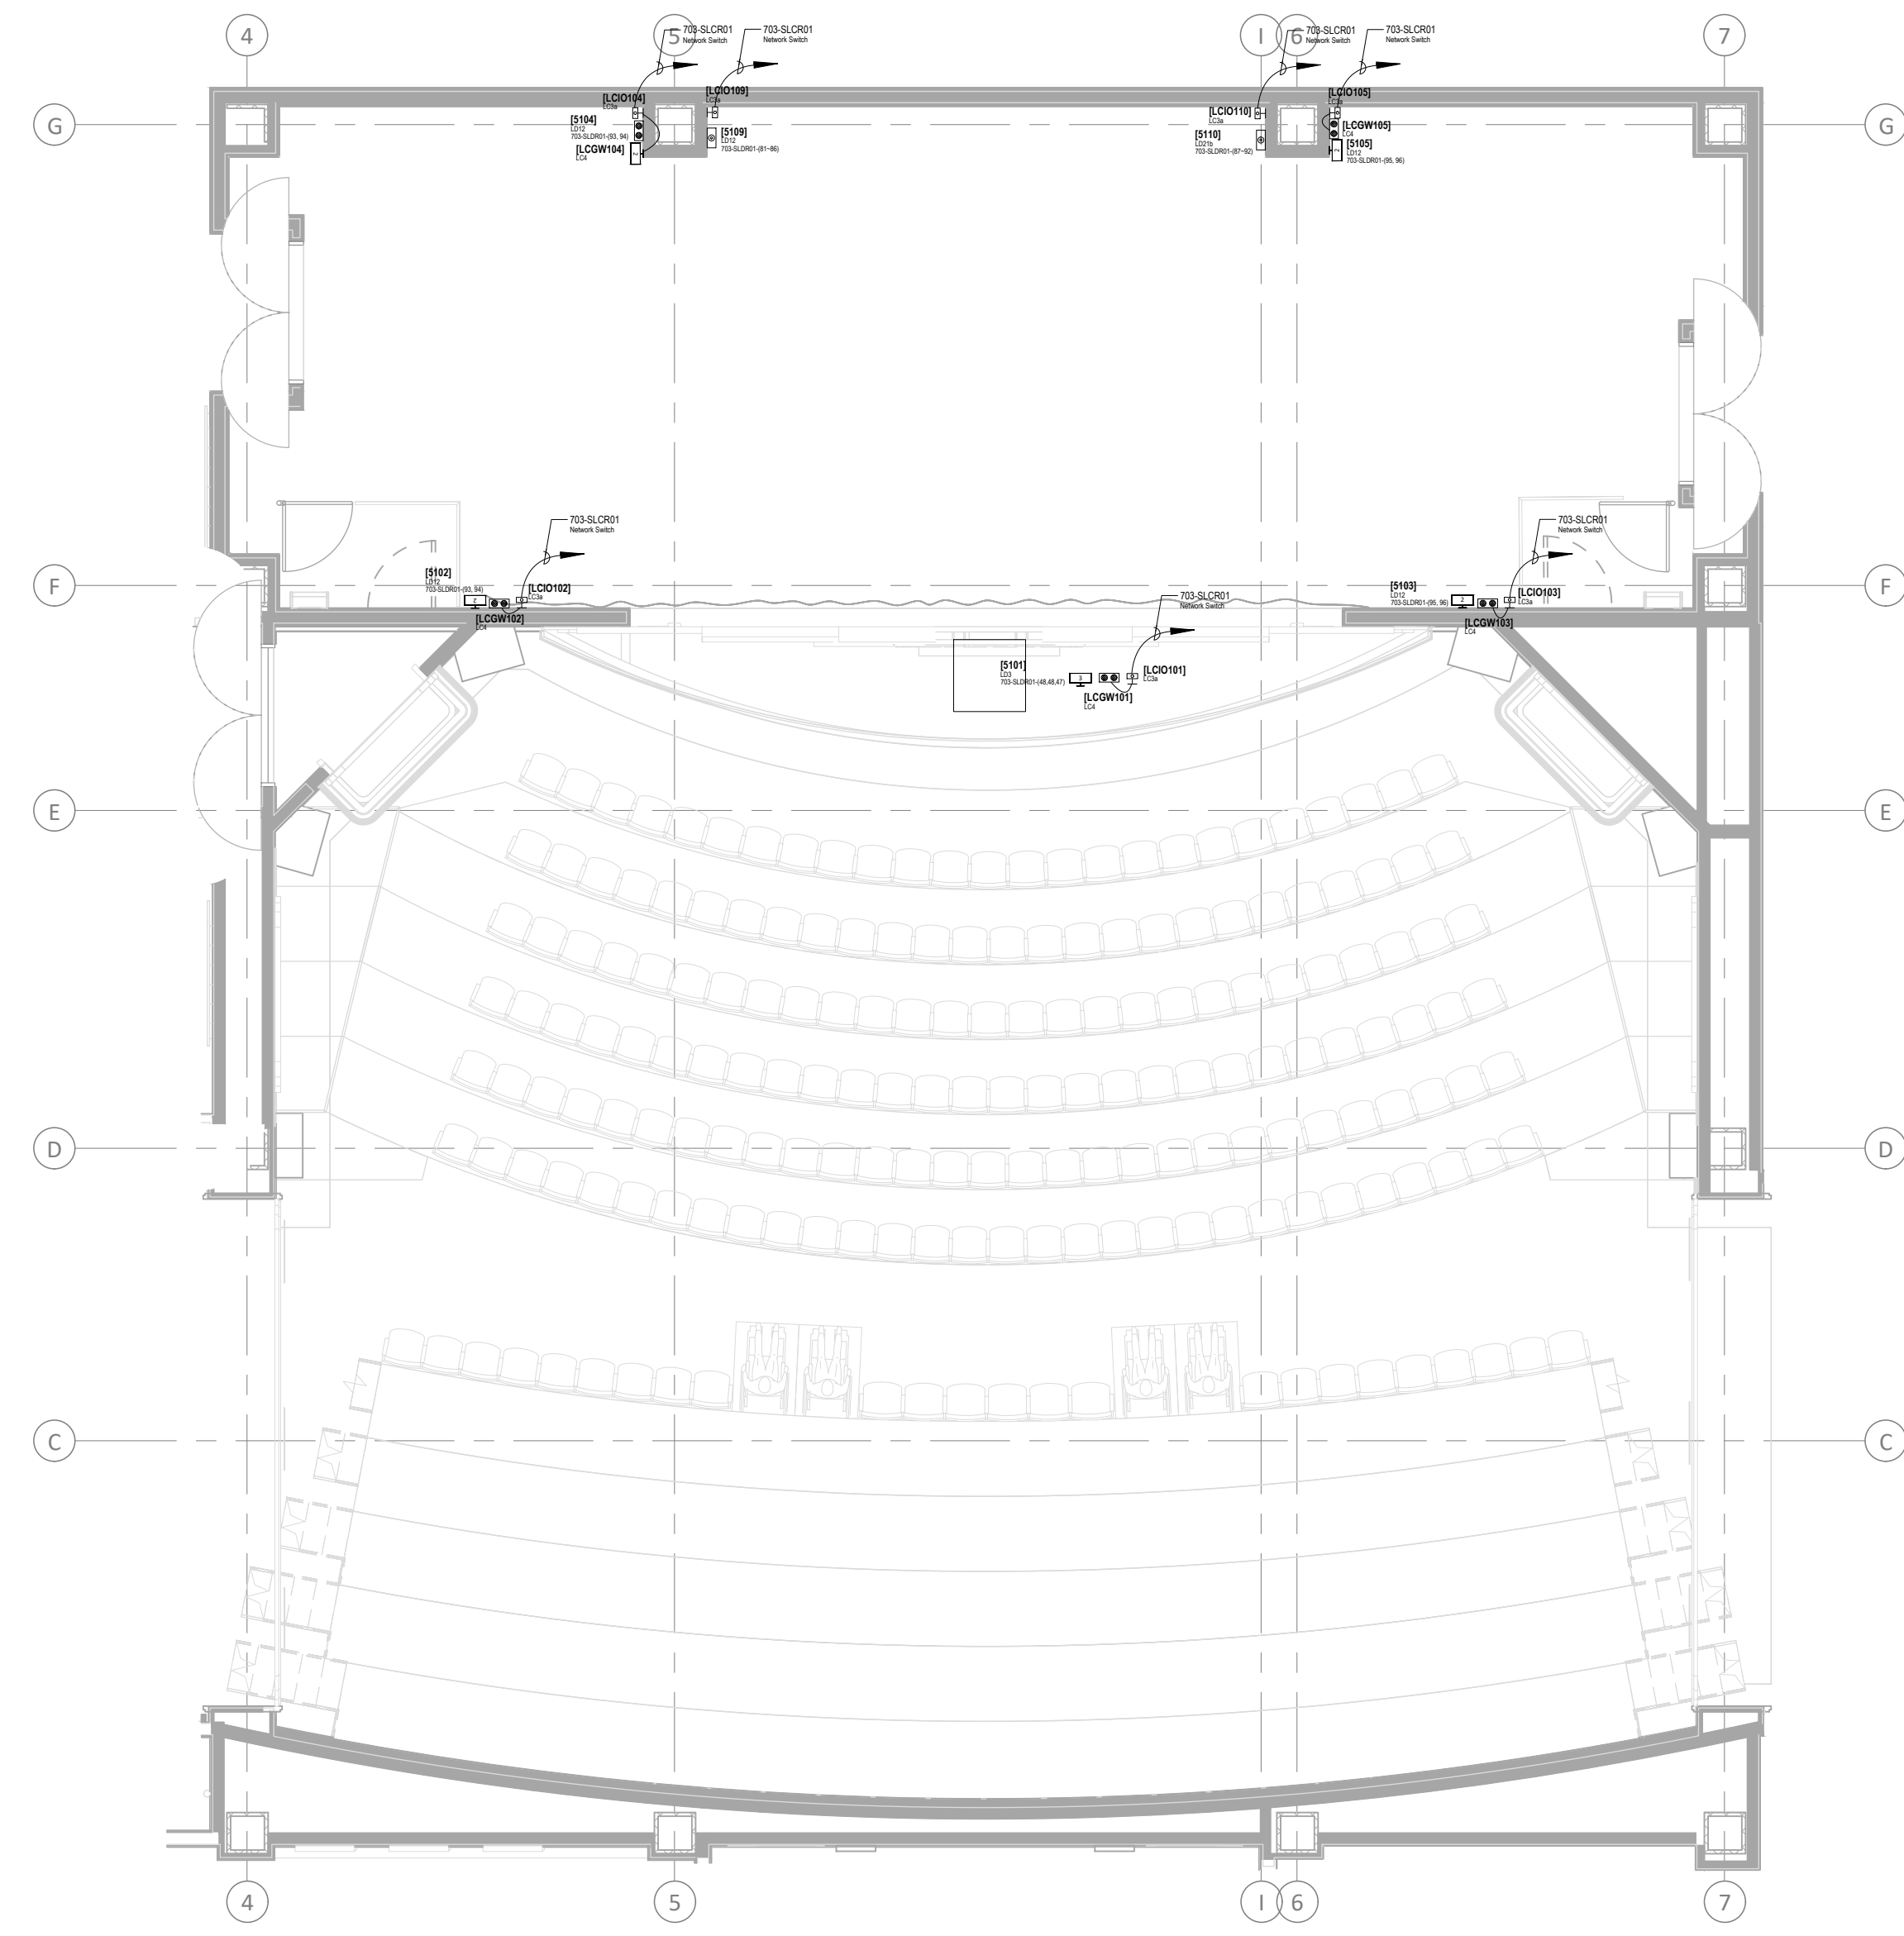

舞台内平面图 - 主题灯光
4 STAGE PLAN - THEMED LIGHTING
TL133

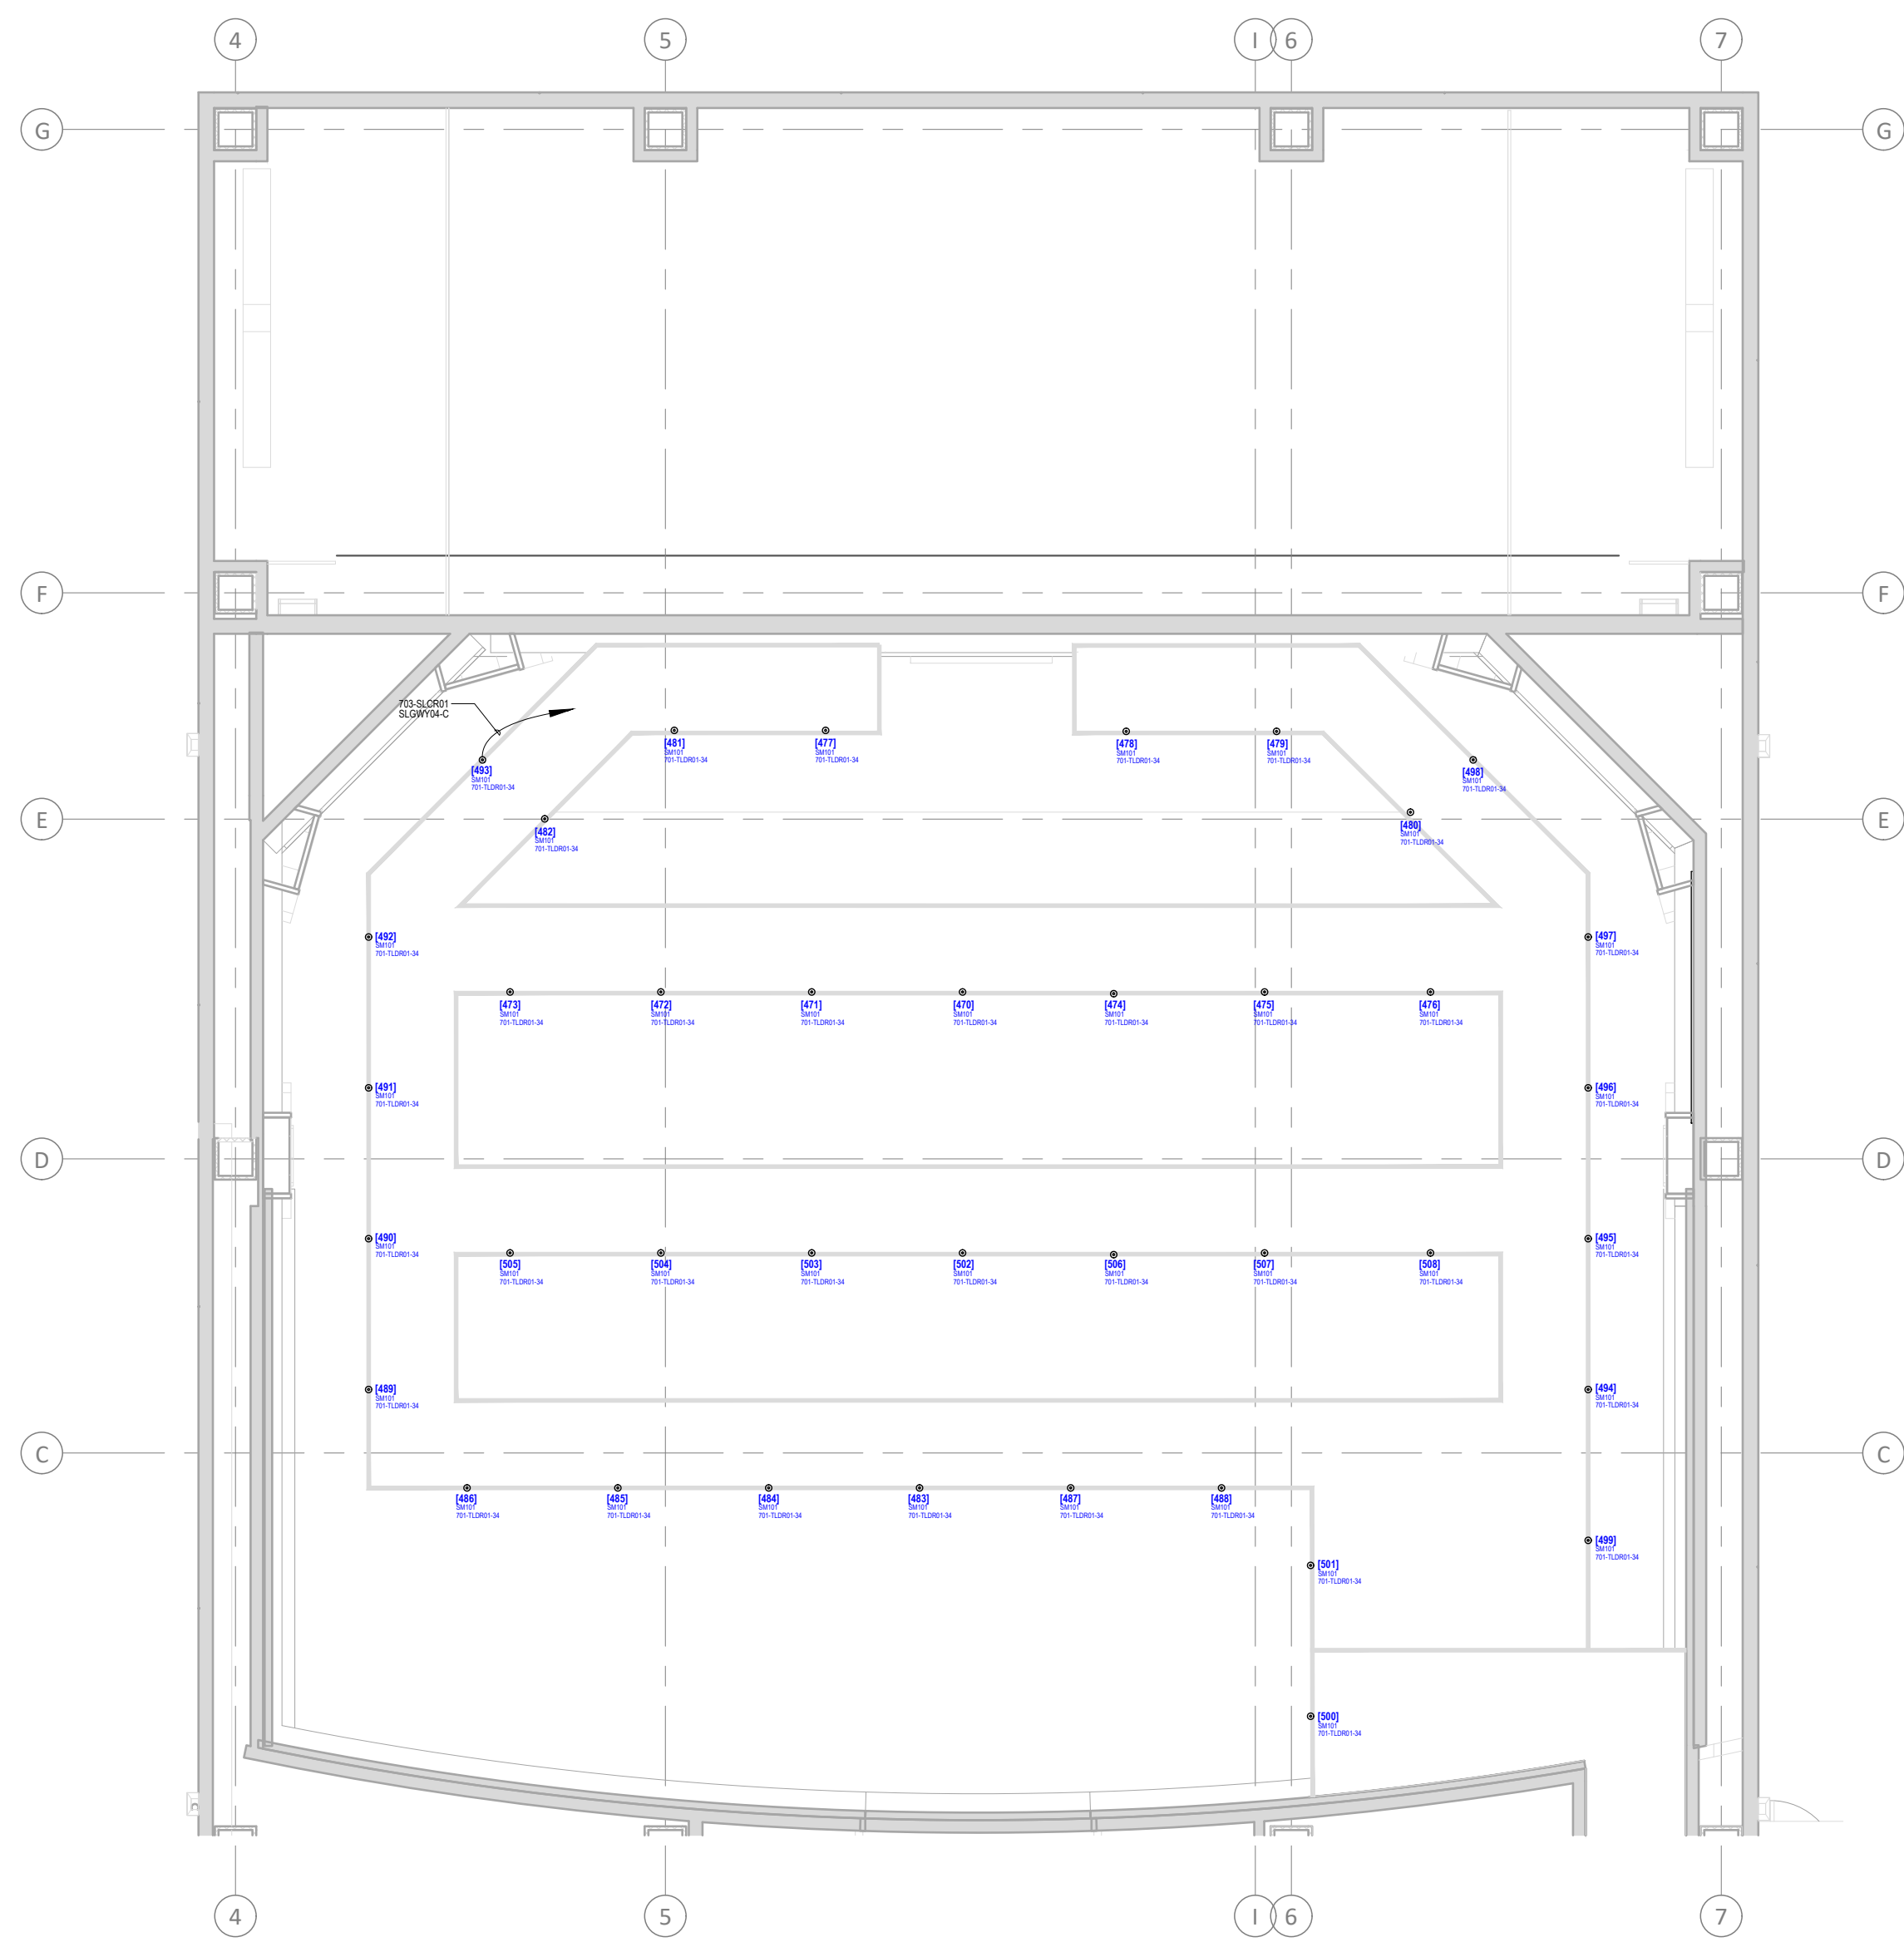

马道平面图 - 主题灯光
CATWALK PLAN - THEMED LIGHTING
1
TL131f