



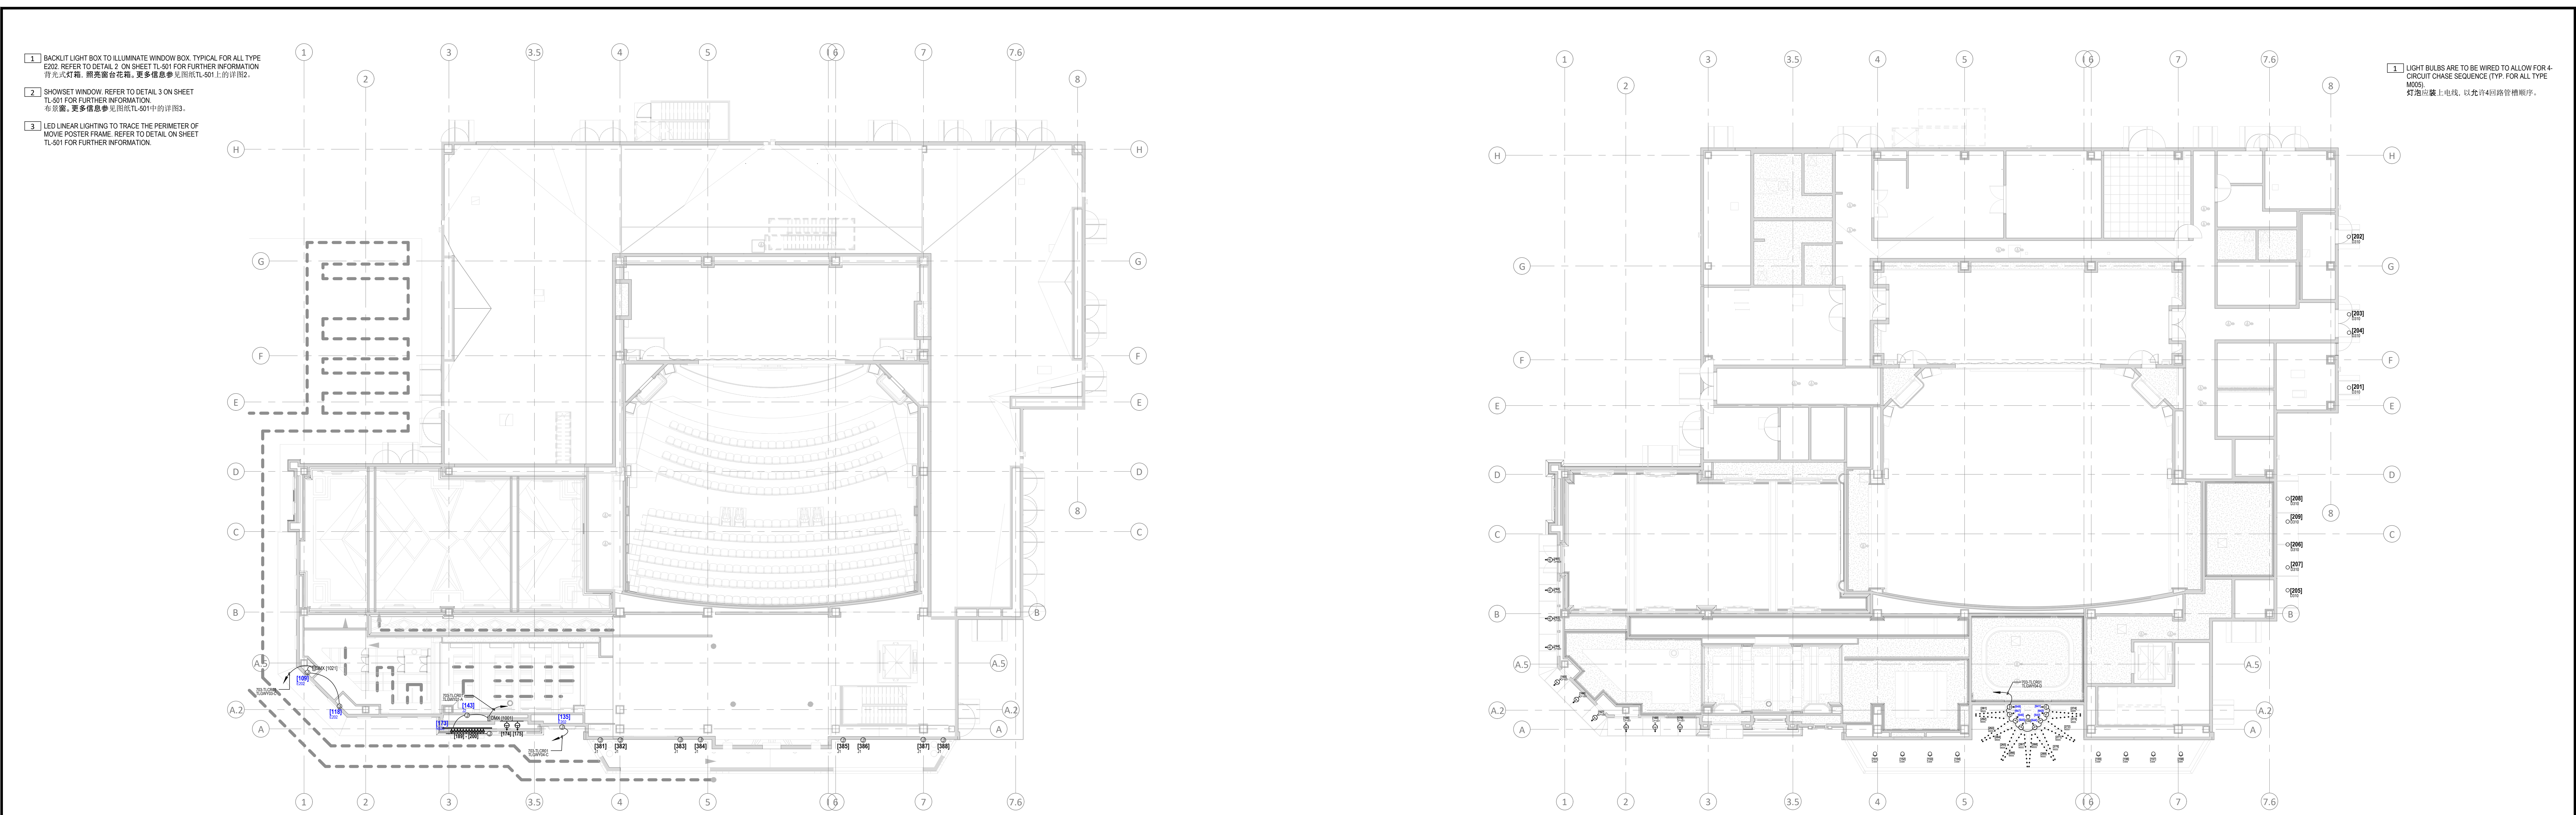


平面图 - 下层 - 主题灯光
FLOOR PLAN - LOWER LEVEL - THEMED LIGHTING

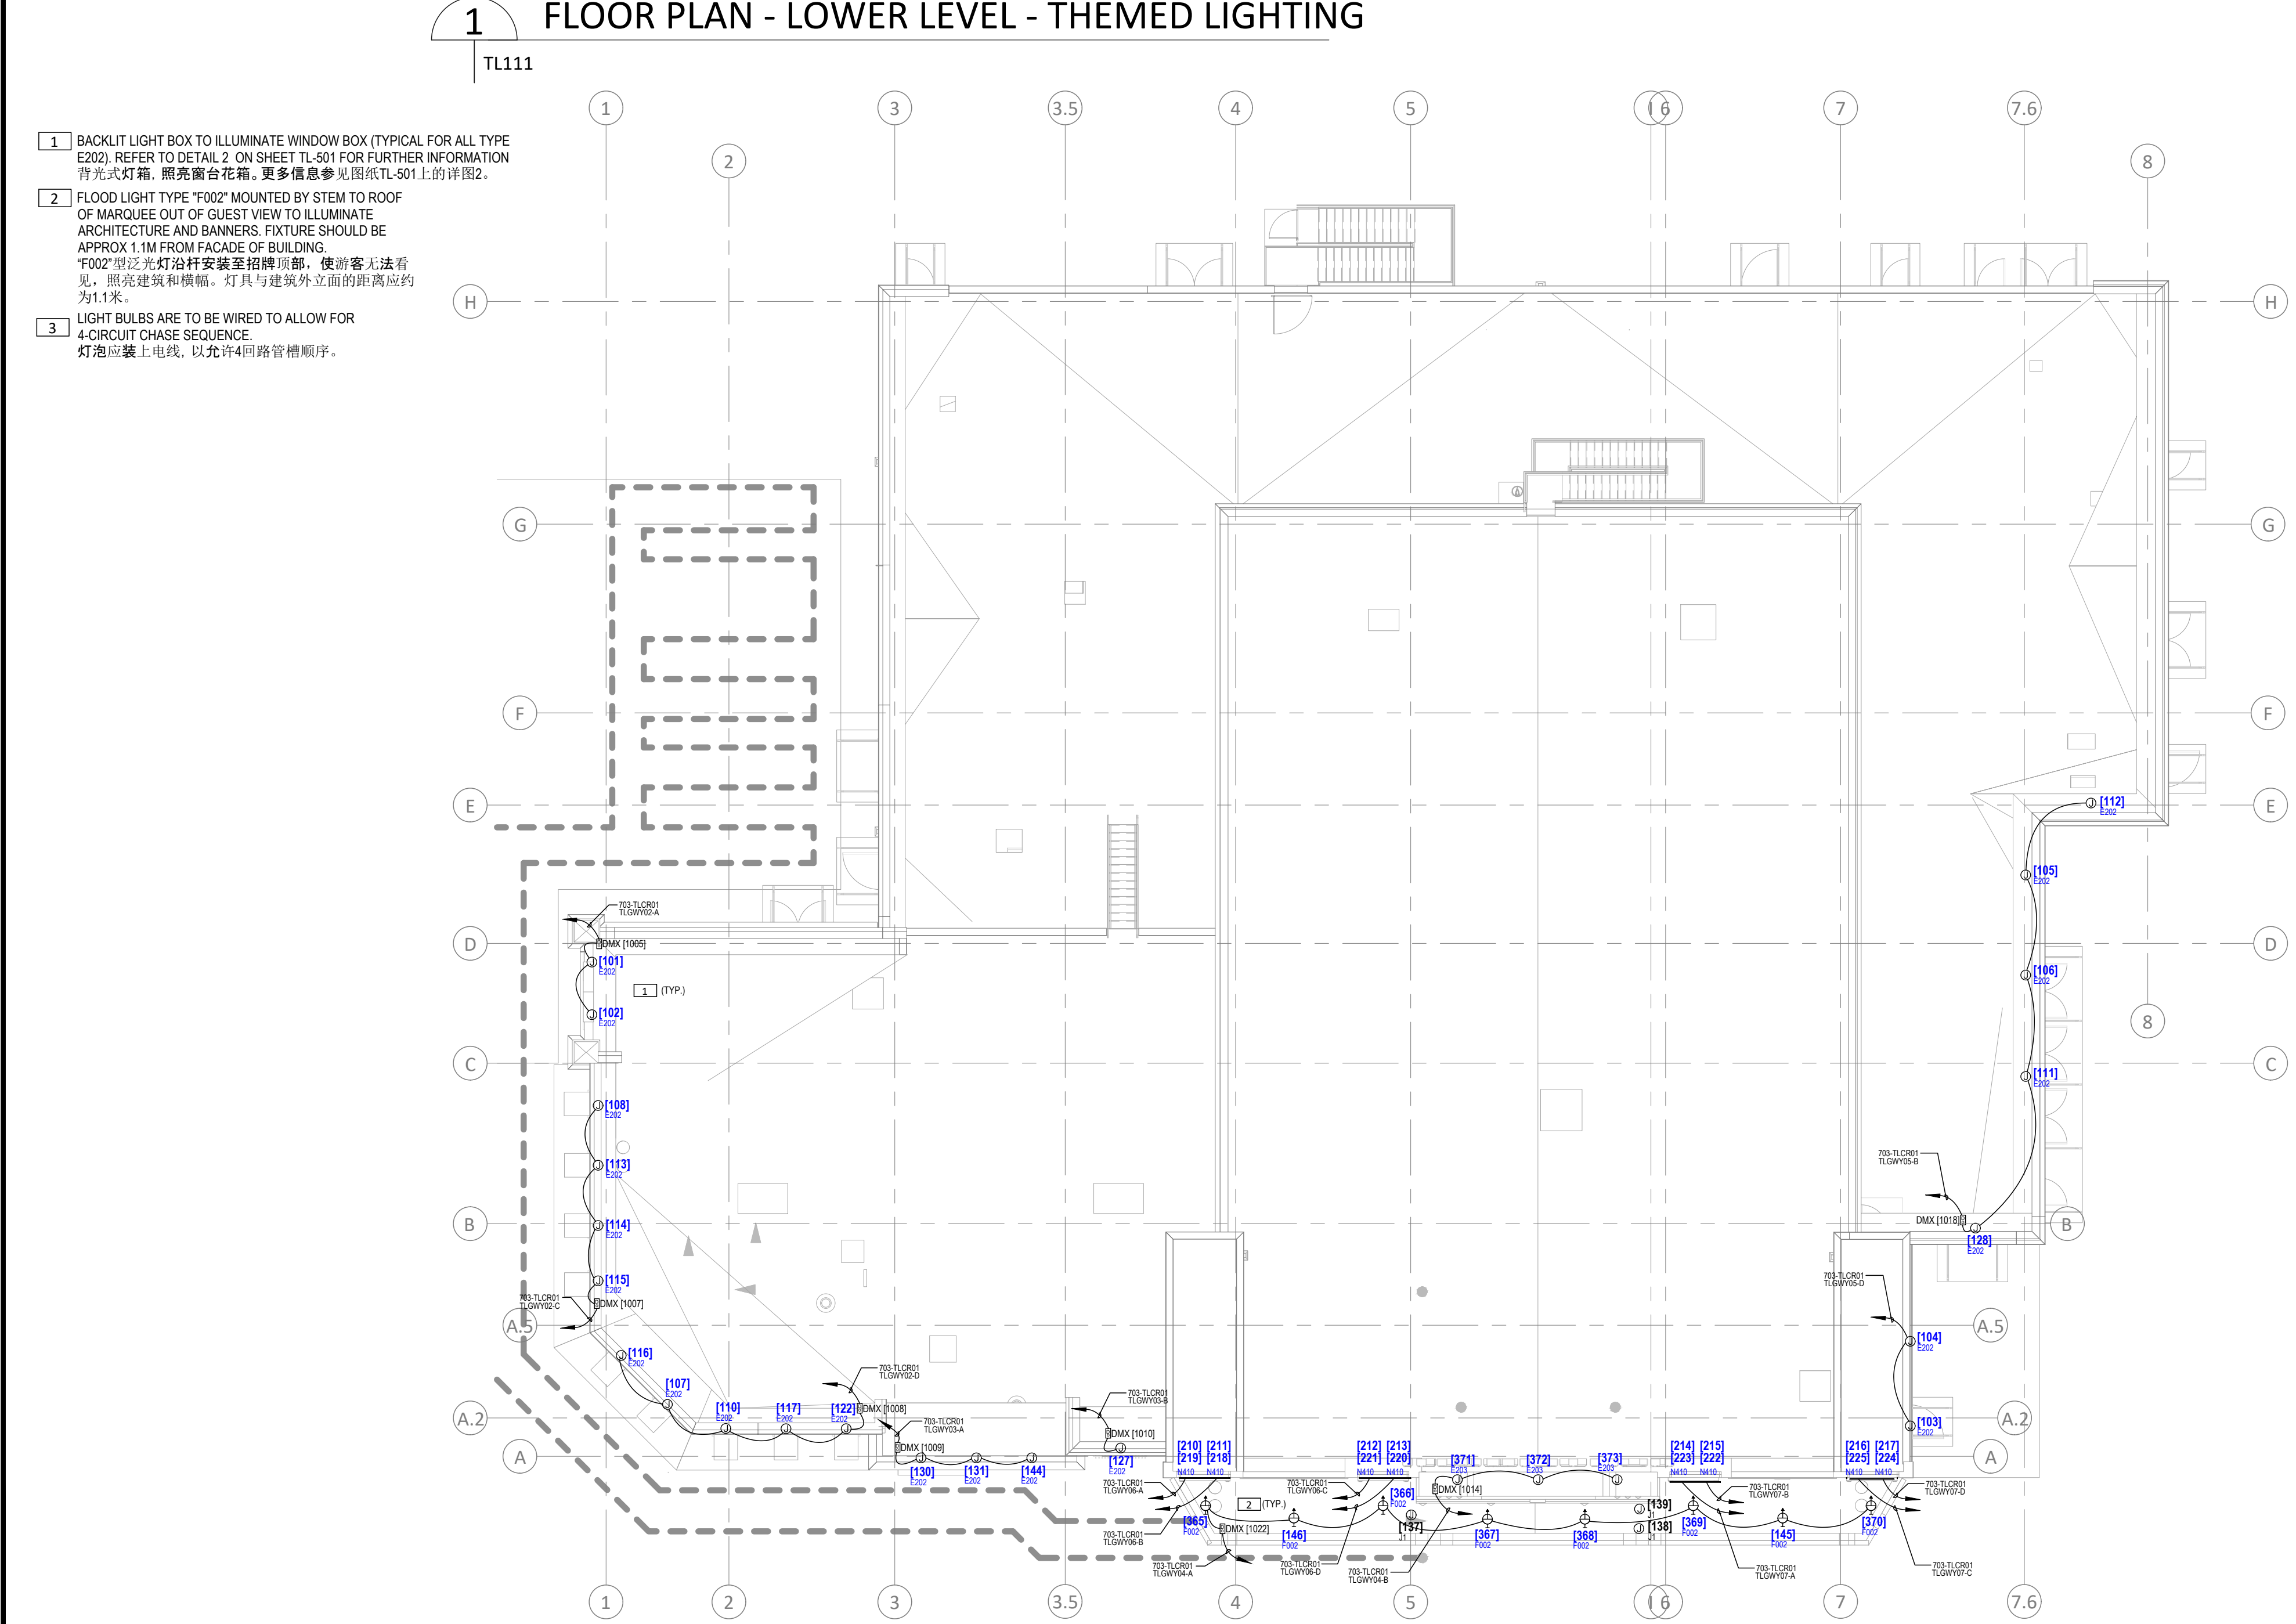

天花板平面图 - 下层 - 主题灯光
CEILING PLAN - LOWER LEVEL - THEMED LIGHTING




平面图 - 上层 - 主题灯光
FLOOR PLAN - UPPER LEVEL - THEMED LIGHTING

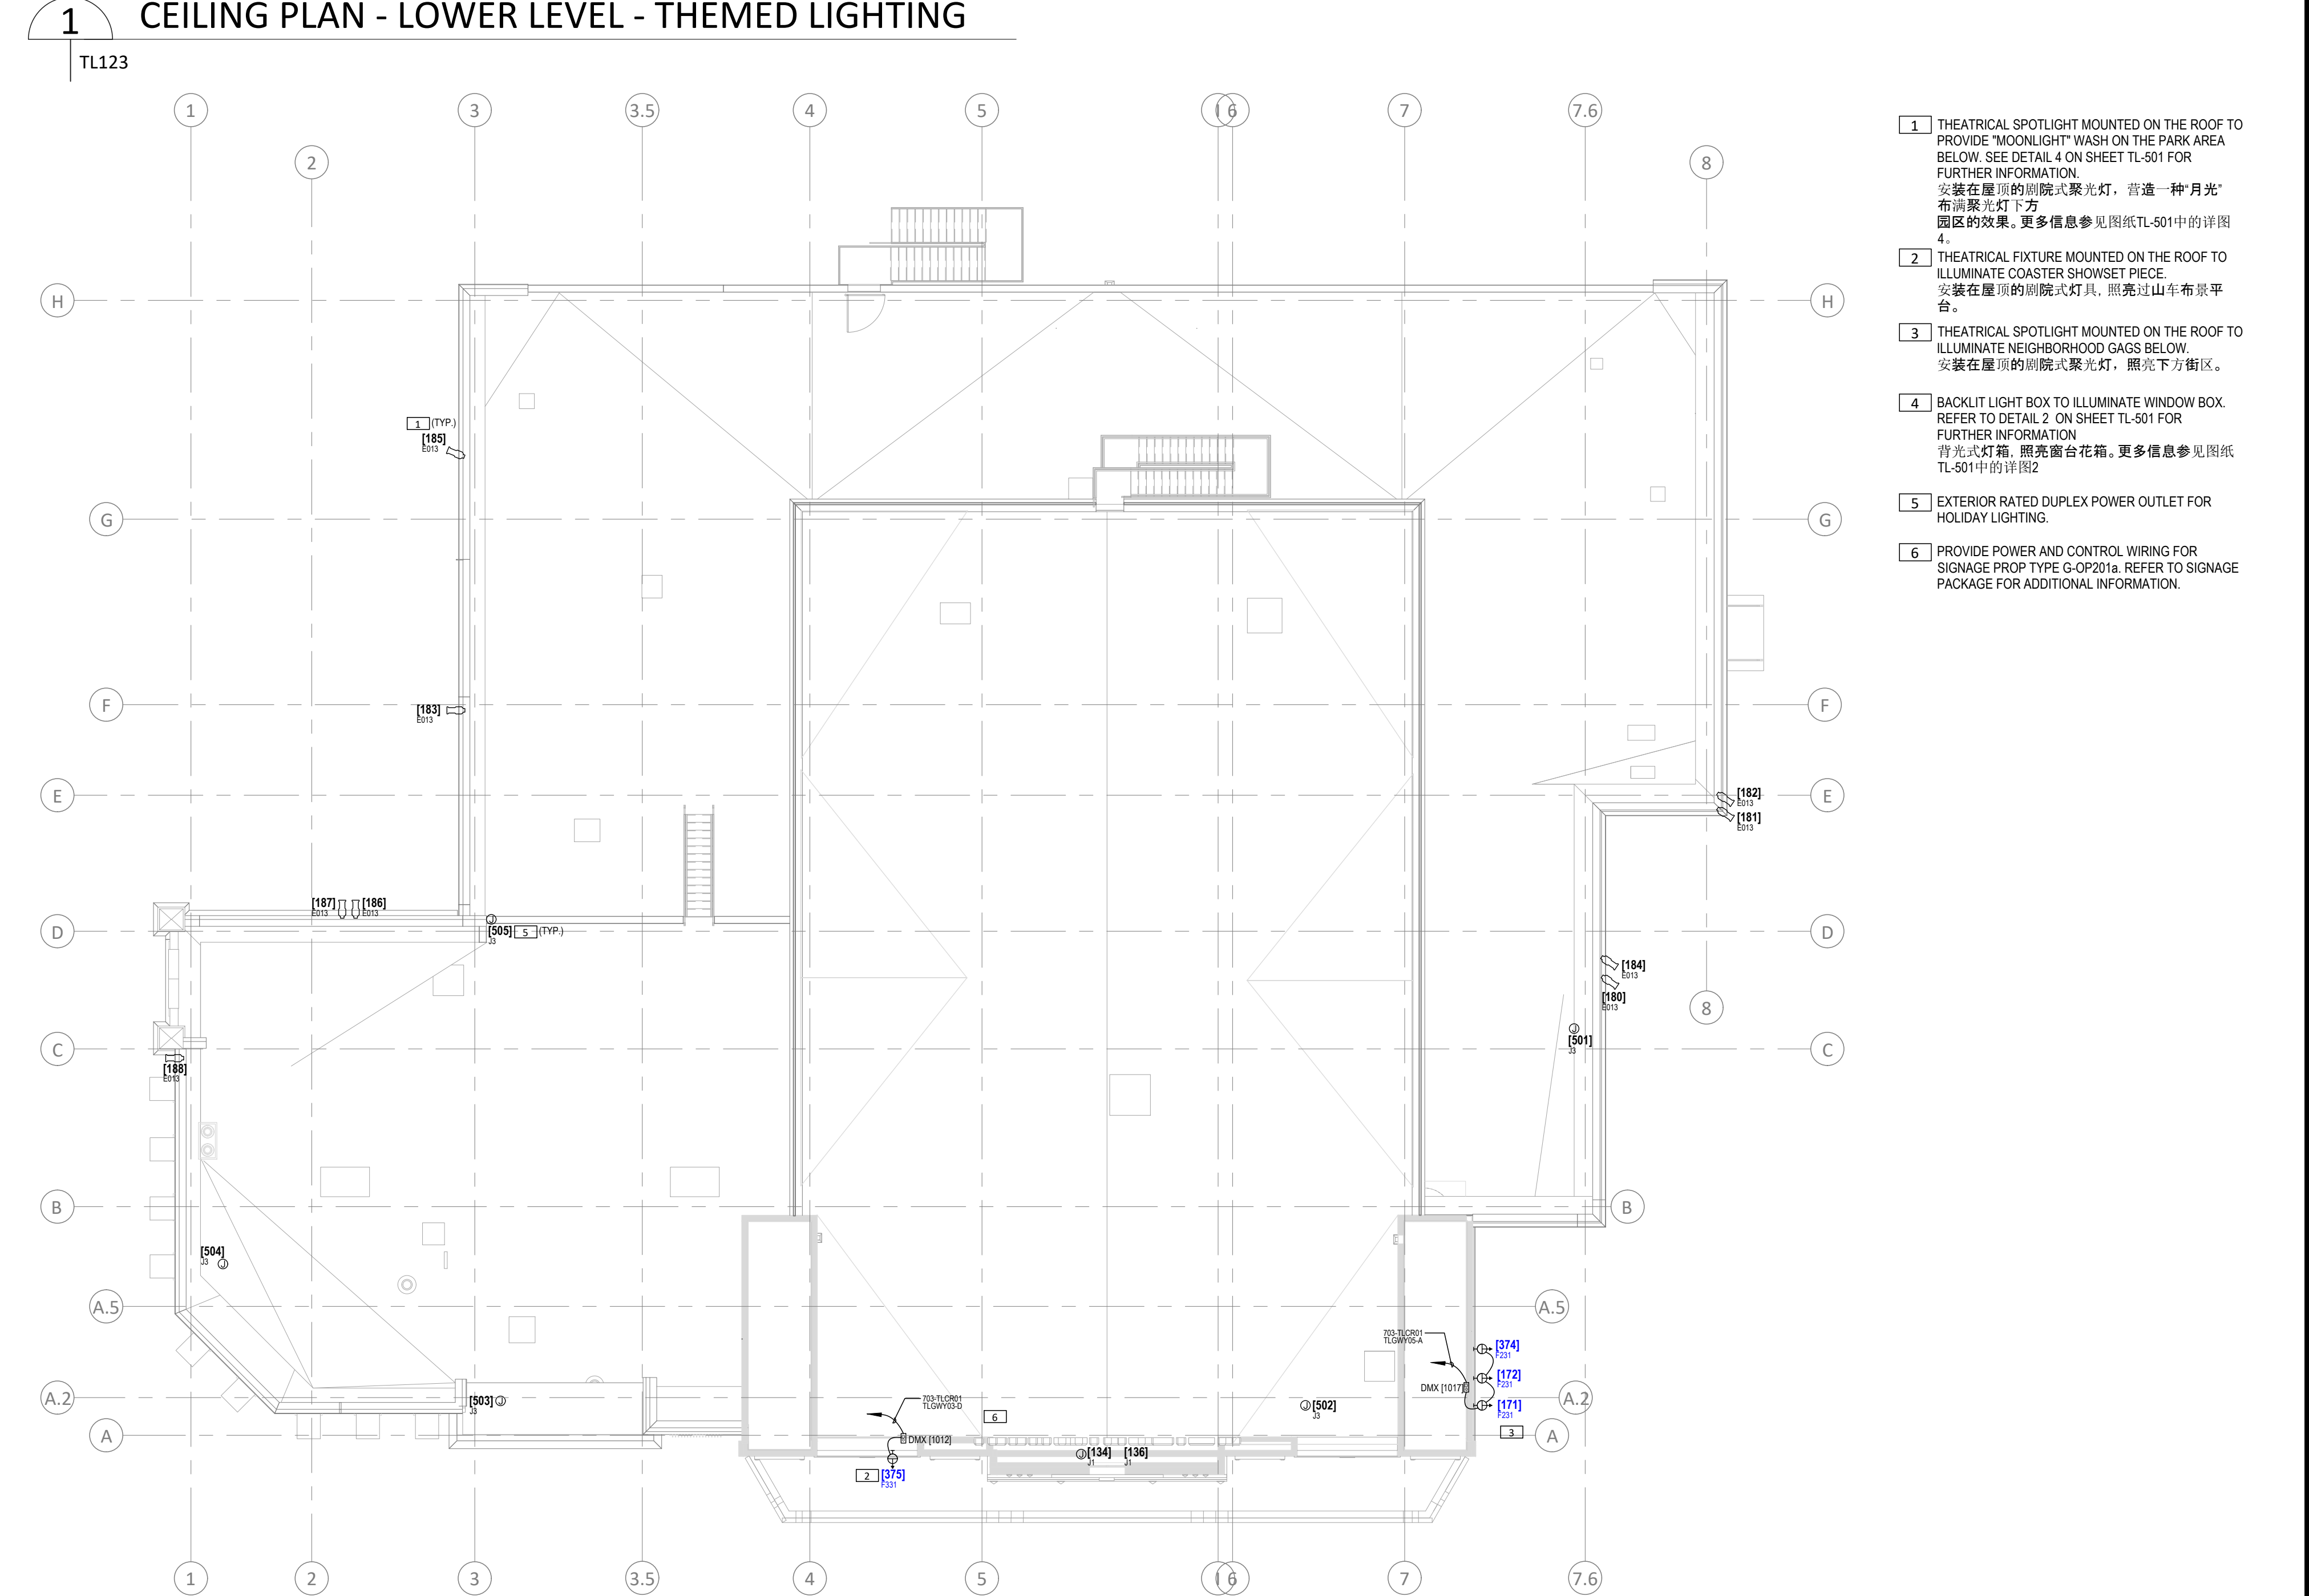


屋顶平面图 - 主题灯光
ROOF PLAN - THEMED LIGHTING

- 1 BACKLIT WINDOW (TYPICAL FOR ALL TYPE E202). REFER TO DETAIL 2 ON SHEET TL-501 FOR FURTHER INFORMATION.
背光式窗, 更多信息参见图纸TL-501中的详图2。
- 2 FLOOD LIGHT TYPE "F02" MOUNTED BY STEM TO ROOF OF MARQUEE OUT OF GUEST VIEW TO ILLUMINATE ARCHITECTURE AND BANNERS. FIXTURE SHOULD BE APPROX. 1.4M FROM FACADE OF BUILDING.
"F02"型泛光灯沿杆安装至招牌顶部, 使游客无遮挡光, 照亮建筑外墙和横幅。灯具与建筑外立面的距离约为1.4米。
- 3 LIGHT BULB SOCKETS RECESSED UNDER MARQUEE TO CREATE CHASING PATTERN. REFER TO FIXTURE SCHEDULE FOR FURTHER INFORMATION. FOUR CONTROL ZONES WERE PROVIDED FOR A CHASE EFFECT.
将入式灯泡插座安装在招牌下方, 形成追逐图案效果。更多信息参见灯具一览表。为追逐效果提供四个控制区。
- 4 FLOOD LIGHT TYPE "F02" MOUNTED BY STEM TO ROOF OF MARQUEE OUT OF GUEST VIEW TO ILLUMINATE ARCHITECTURE AND BANNERS. FIXTURE SHOULD BE APPROX. 1.1M FROM FACADE OF BUILDING.
"F02"型泛光灯沿杆安装至招牌顶部, 使游客无遮挡光, 照亮建筑外墙和横幅。灯具与建筑外立面的距离约为1.1米。
- 5 COLOR-CHANGING LED TO BACKLIT GLASS BLOCK WINDOWS (TYP. FOR ALL TYPE E203). REFER TO DETAIL 1 ON TL-501 FOR FURTHER INFORMATION. 变色LED灯照亮背光式玻璃块窗。更多信息参见图纸 TL-501中的详图1。
- 6 SHOWSET WINDOW. REFER TO DETAIL 3 ON SHEET TL-501 FOR FURTHER INFORMATION. 布景窗, 更多信息参见图纸TL-501中的详图3。
- 7 THEATRICAL SPOTLIGHT MOUNTED ON THE ROOF TO PROVIDE "MOONLIGHT" WASH ON THE PARK AREA BELOW (TYP. FOR ALL TYPE E030). SEE DETAIL 4 ON SHEET TL-501 FOR FURTHER INFORMATION.
安装在屋顶的剧院式聚光灯, 营造一种"月光"布景聚光灯下方扫过效果。更多信息参见图纸TL-501中的详图4。
- 8 PROVIDE POWER AND CONTROL WIRING FOR SHOWSET SIGNAGE PRIOR ON ROOF TYPE G-0P0201a. REFER TO SIGNAGE PACKAGE FOR ADDITIONAL INFORMATION.
- 9 E202 FOR BACKLIT MARQUEE SIGN.
- 10 M005 MARQUEE BULBS OUTLINING MARQUEE SIGN.
- 11 LED LINEAR LIGHTING TO TRACE THE PERIMETER OF MOVIE POSTER FRAME. REFER TO DETAIL ON SHEET TL-501 FOR FURTHER INFORMATION.

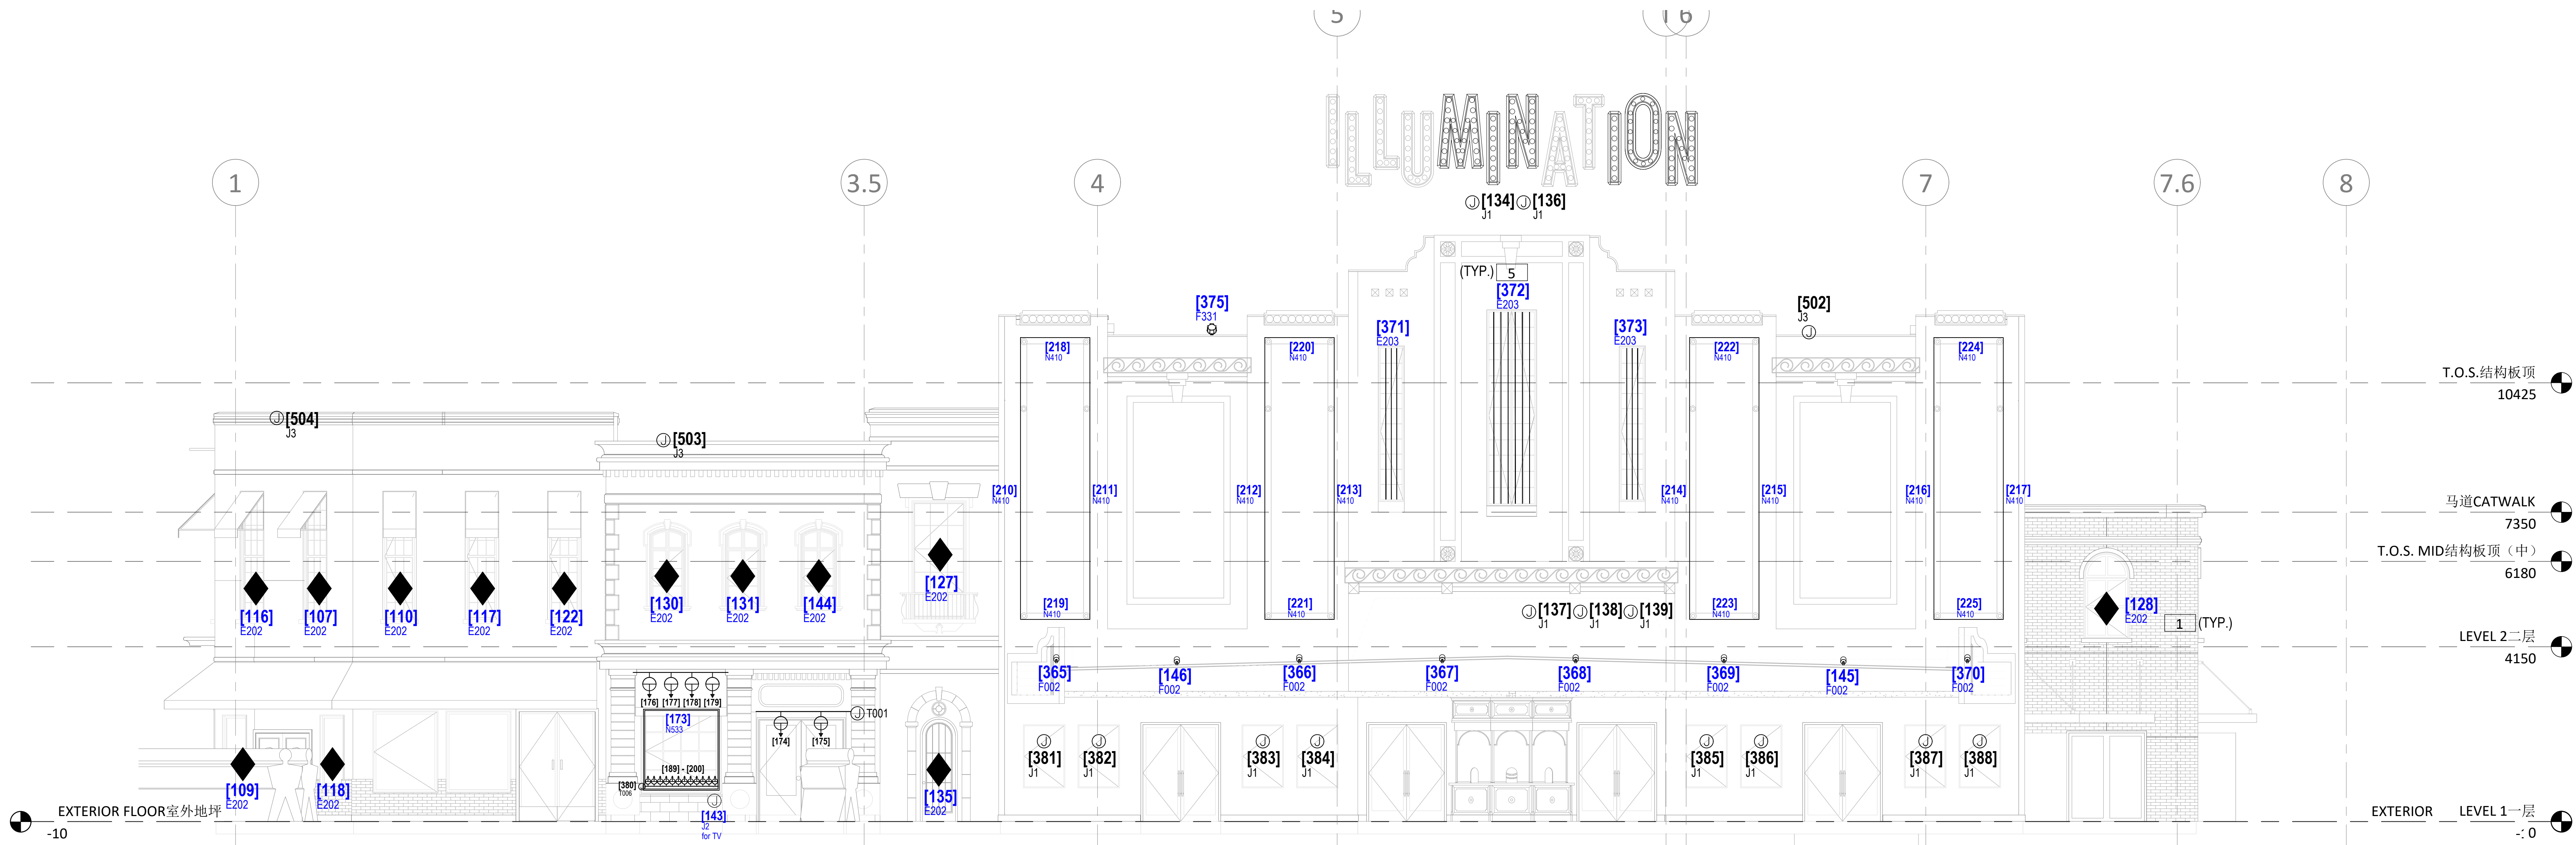

立面图 - 西 - 主题灯光
1 ELEVATION - WEST - THEMED LIGHTING
TL201

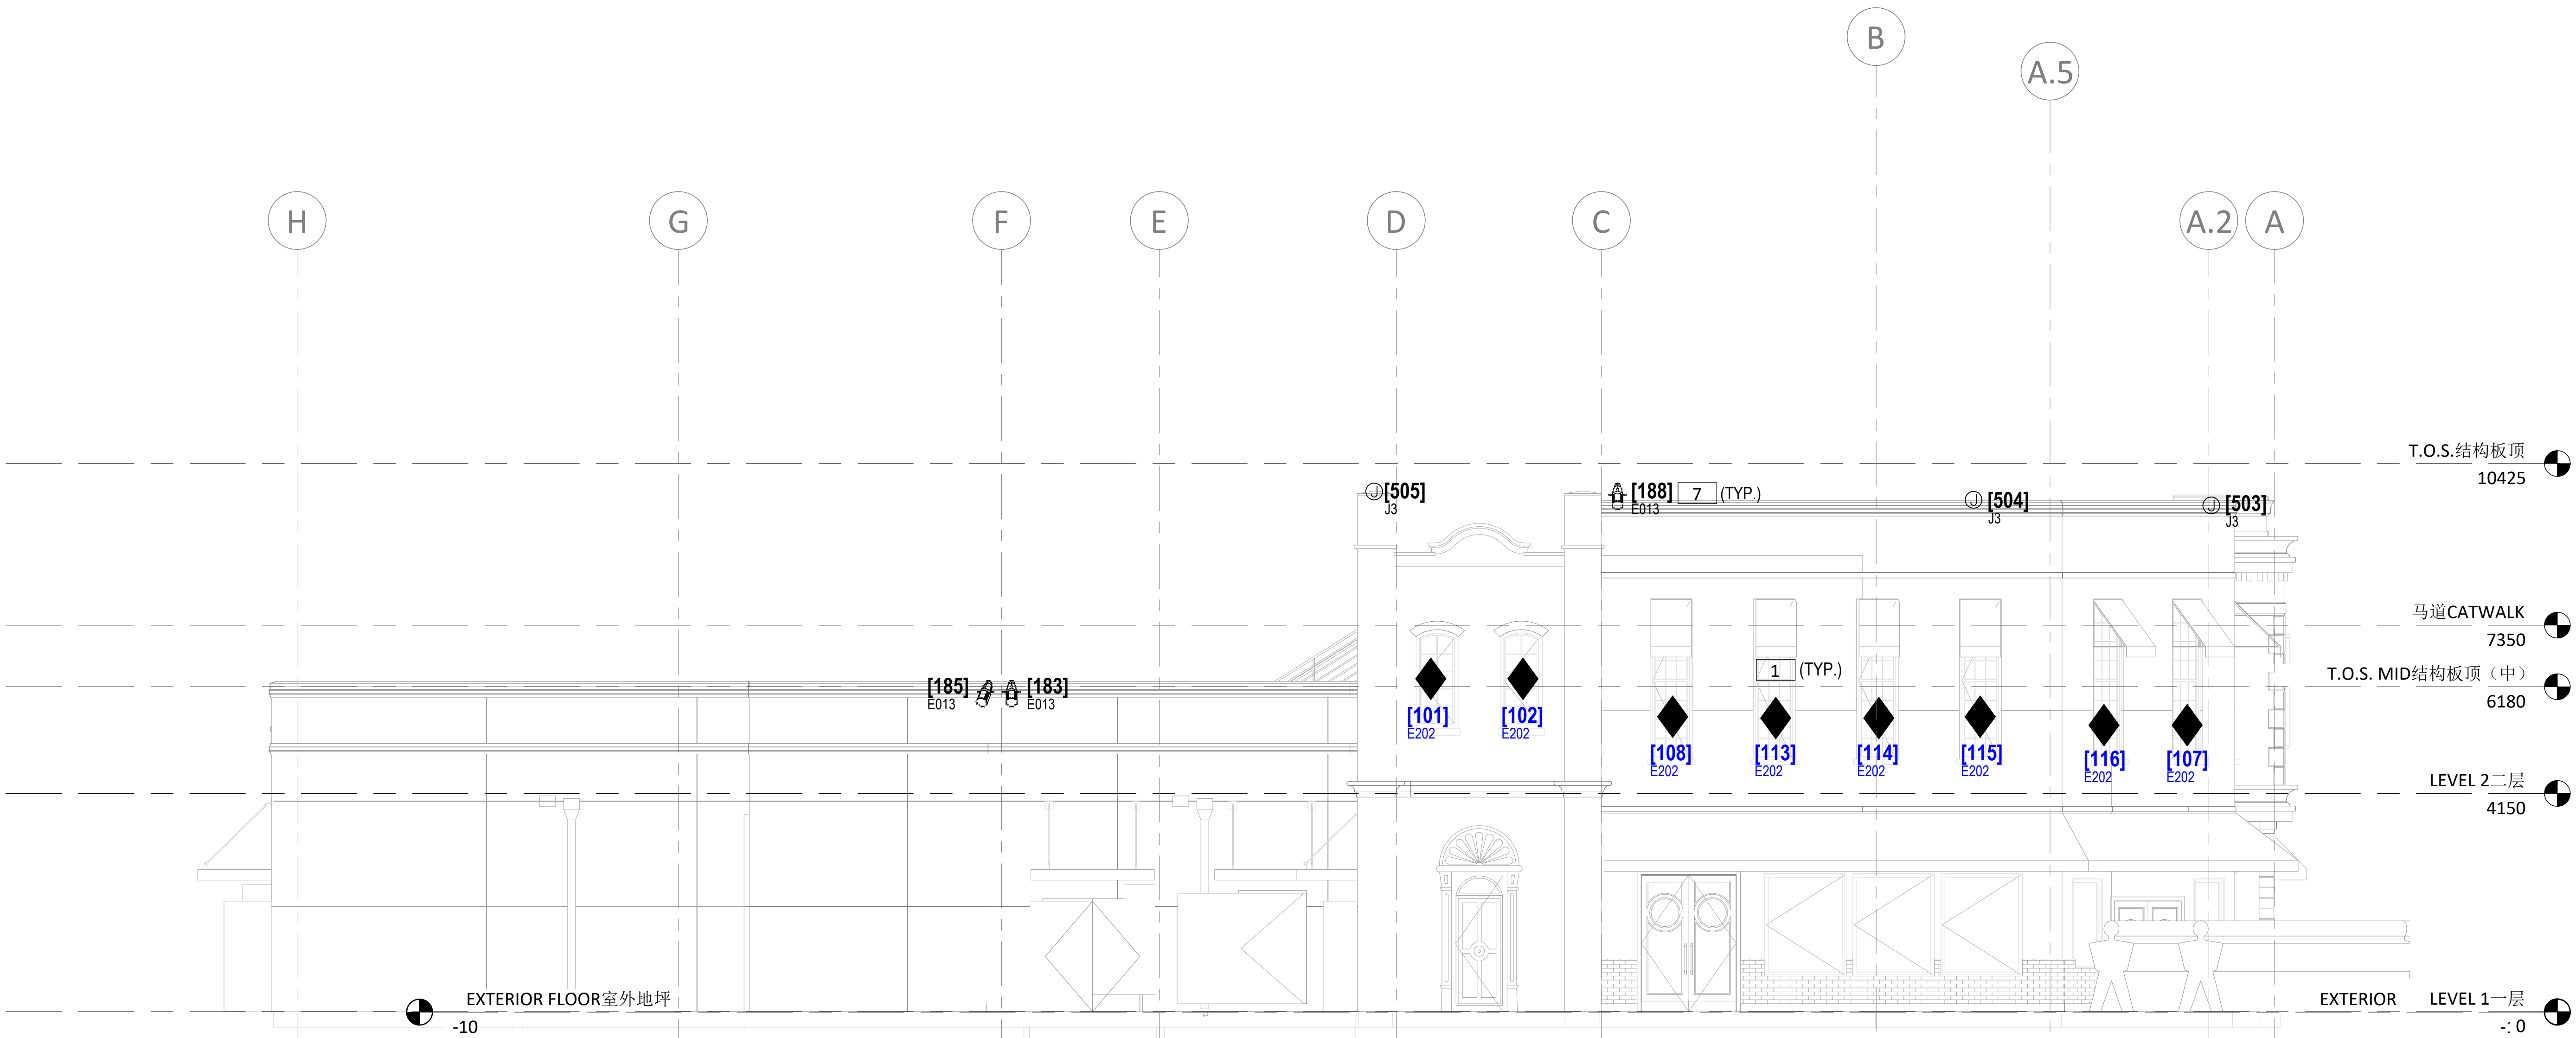

立面图 - 北 - 主题灯光
2 ELEVATION - NORTH - THEMED LIGHTING
TL201