



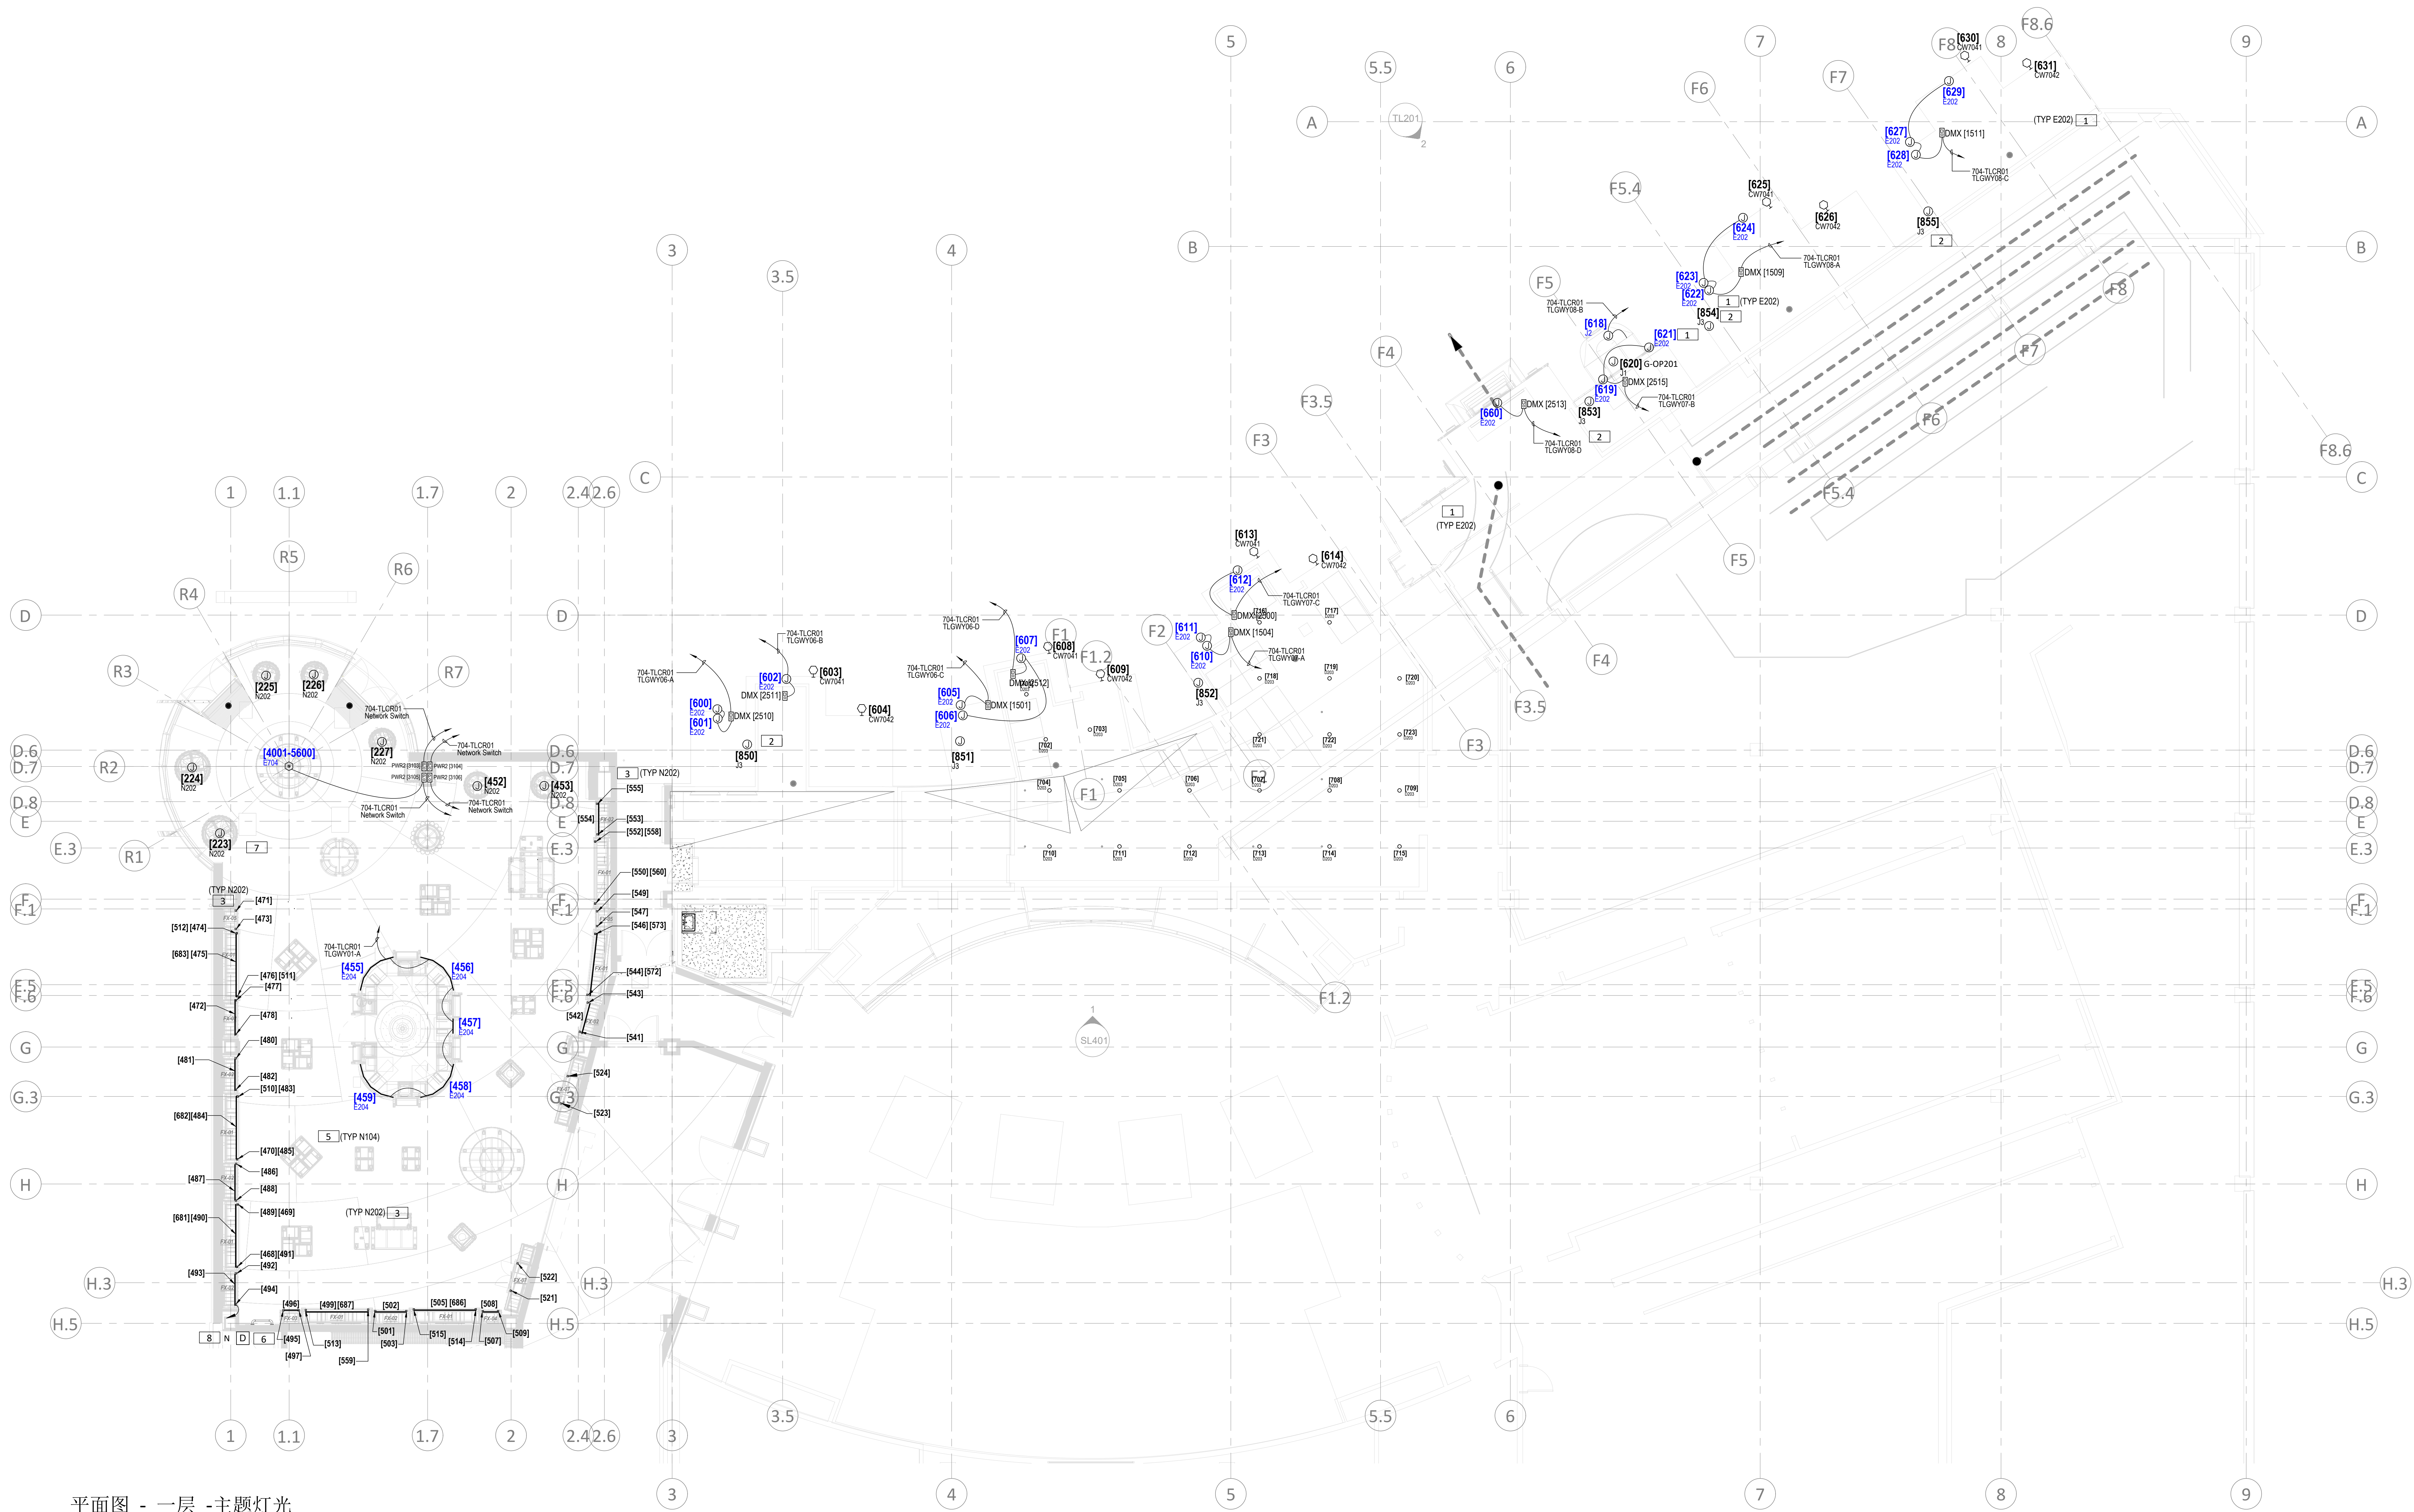


平面图 - 一层 - 主题灯光
Plan View - Level1 - THEMED LIGHTING


2
TL201

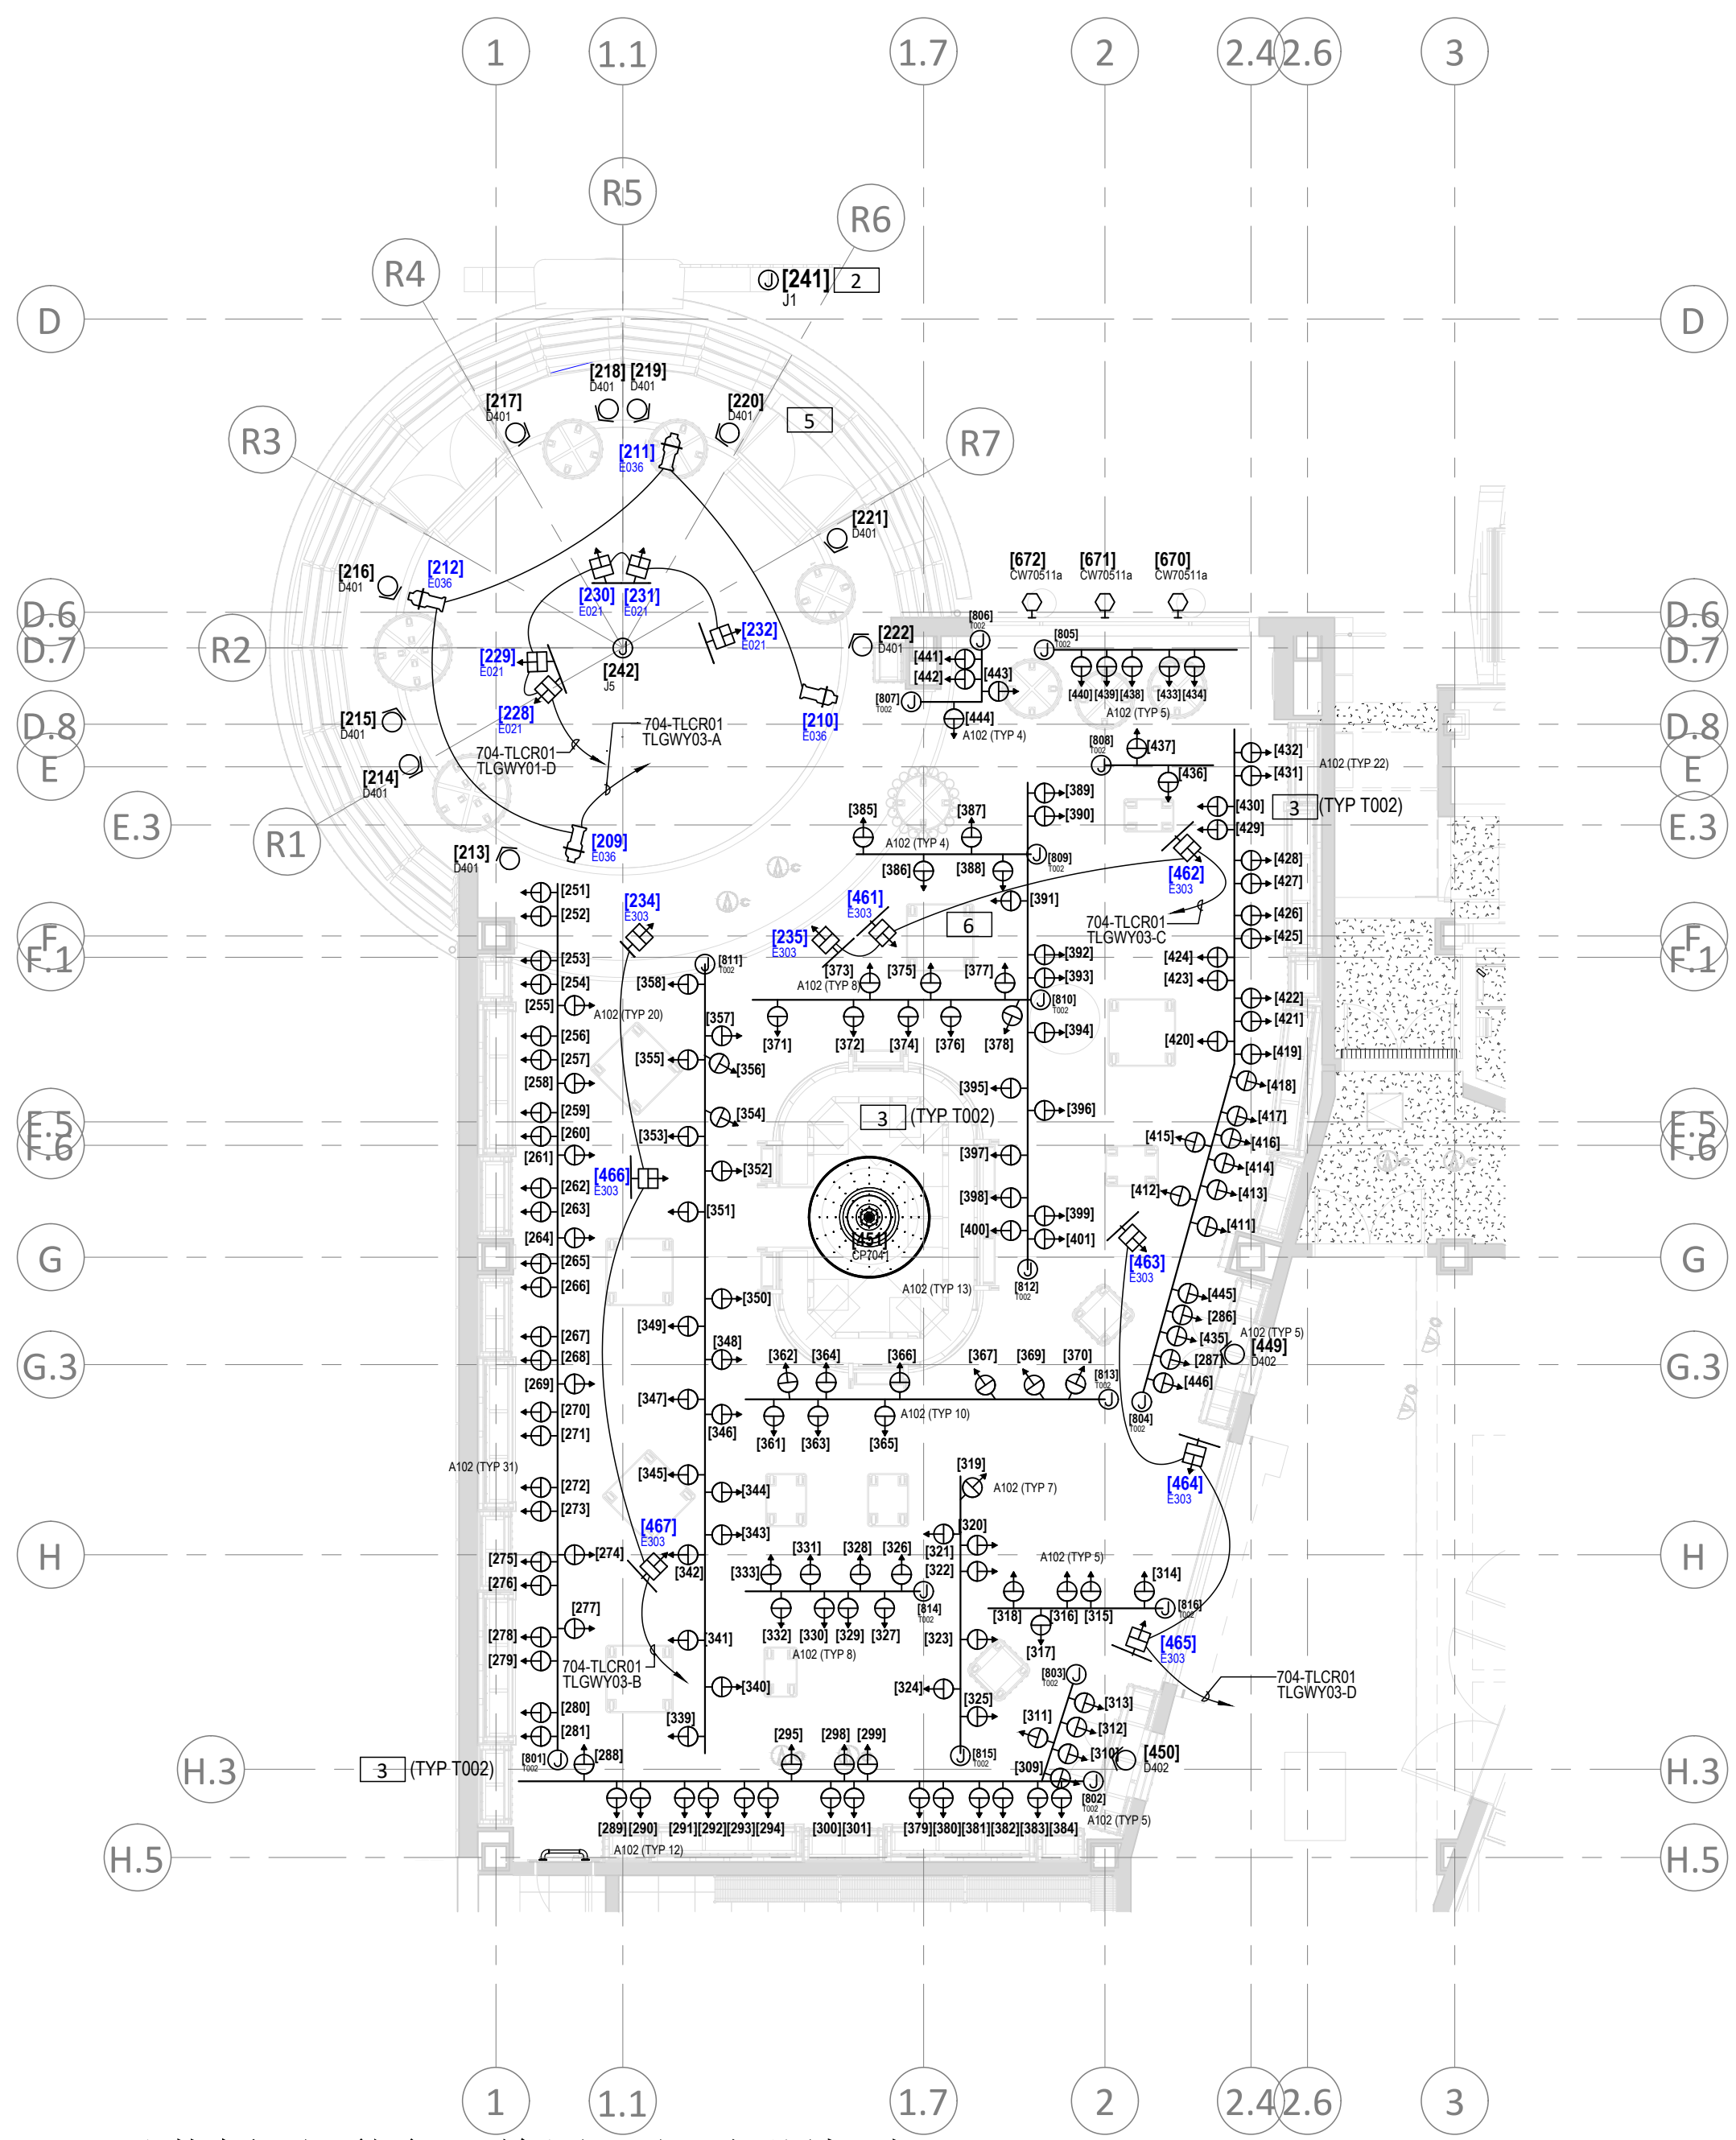


天花板平面图 - 首层f区 - 主题灯光
CEILING PLAN - LEVEL1 AREA f - THEMED LIGHTING

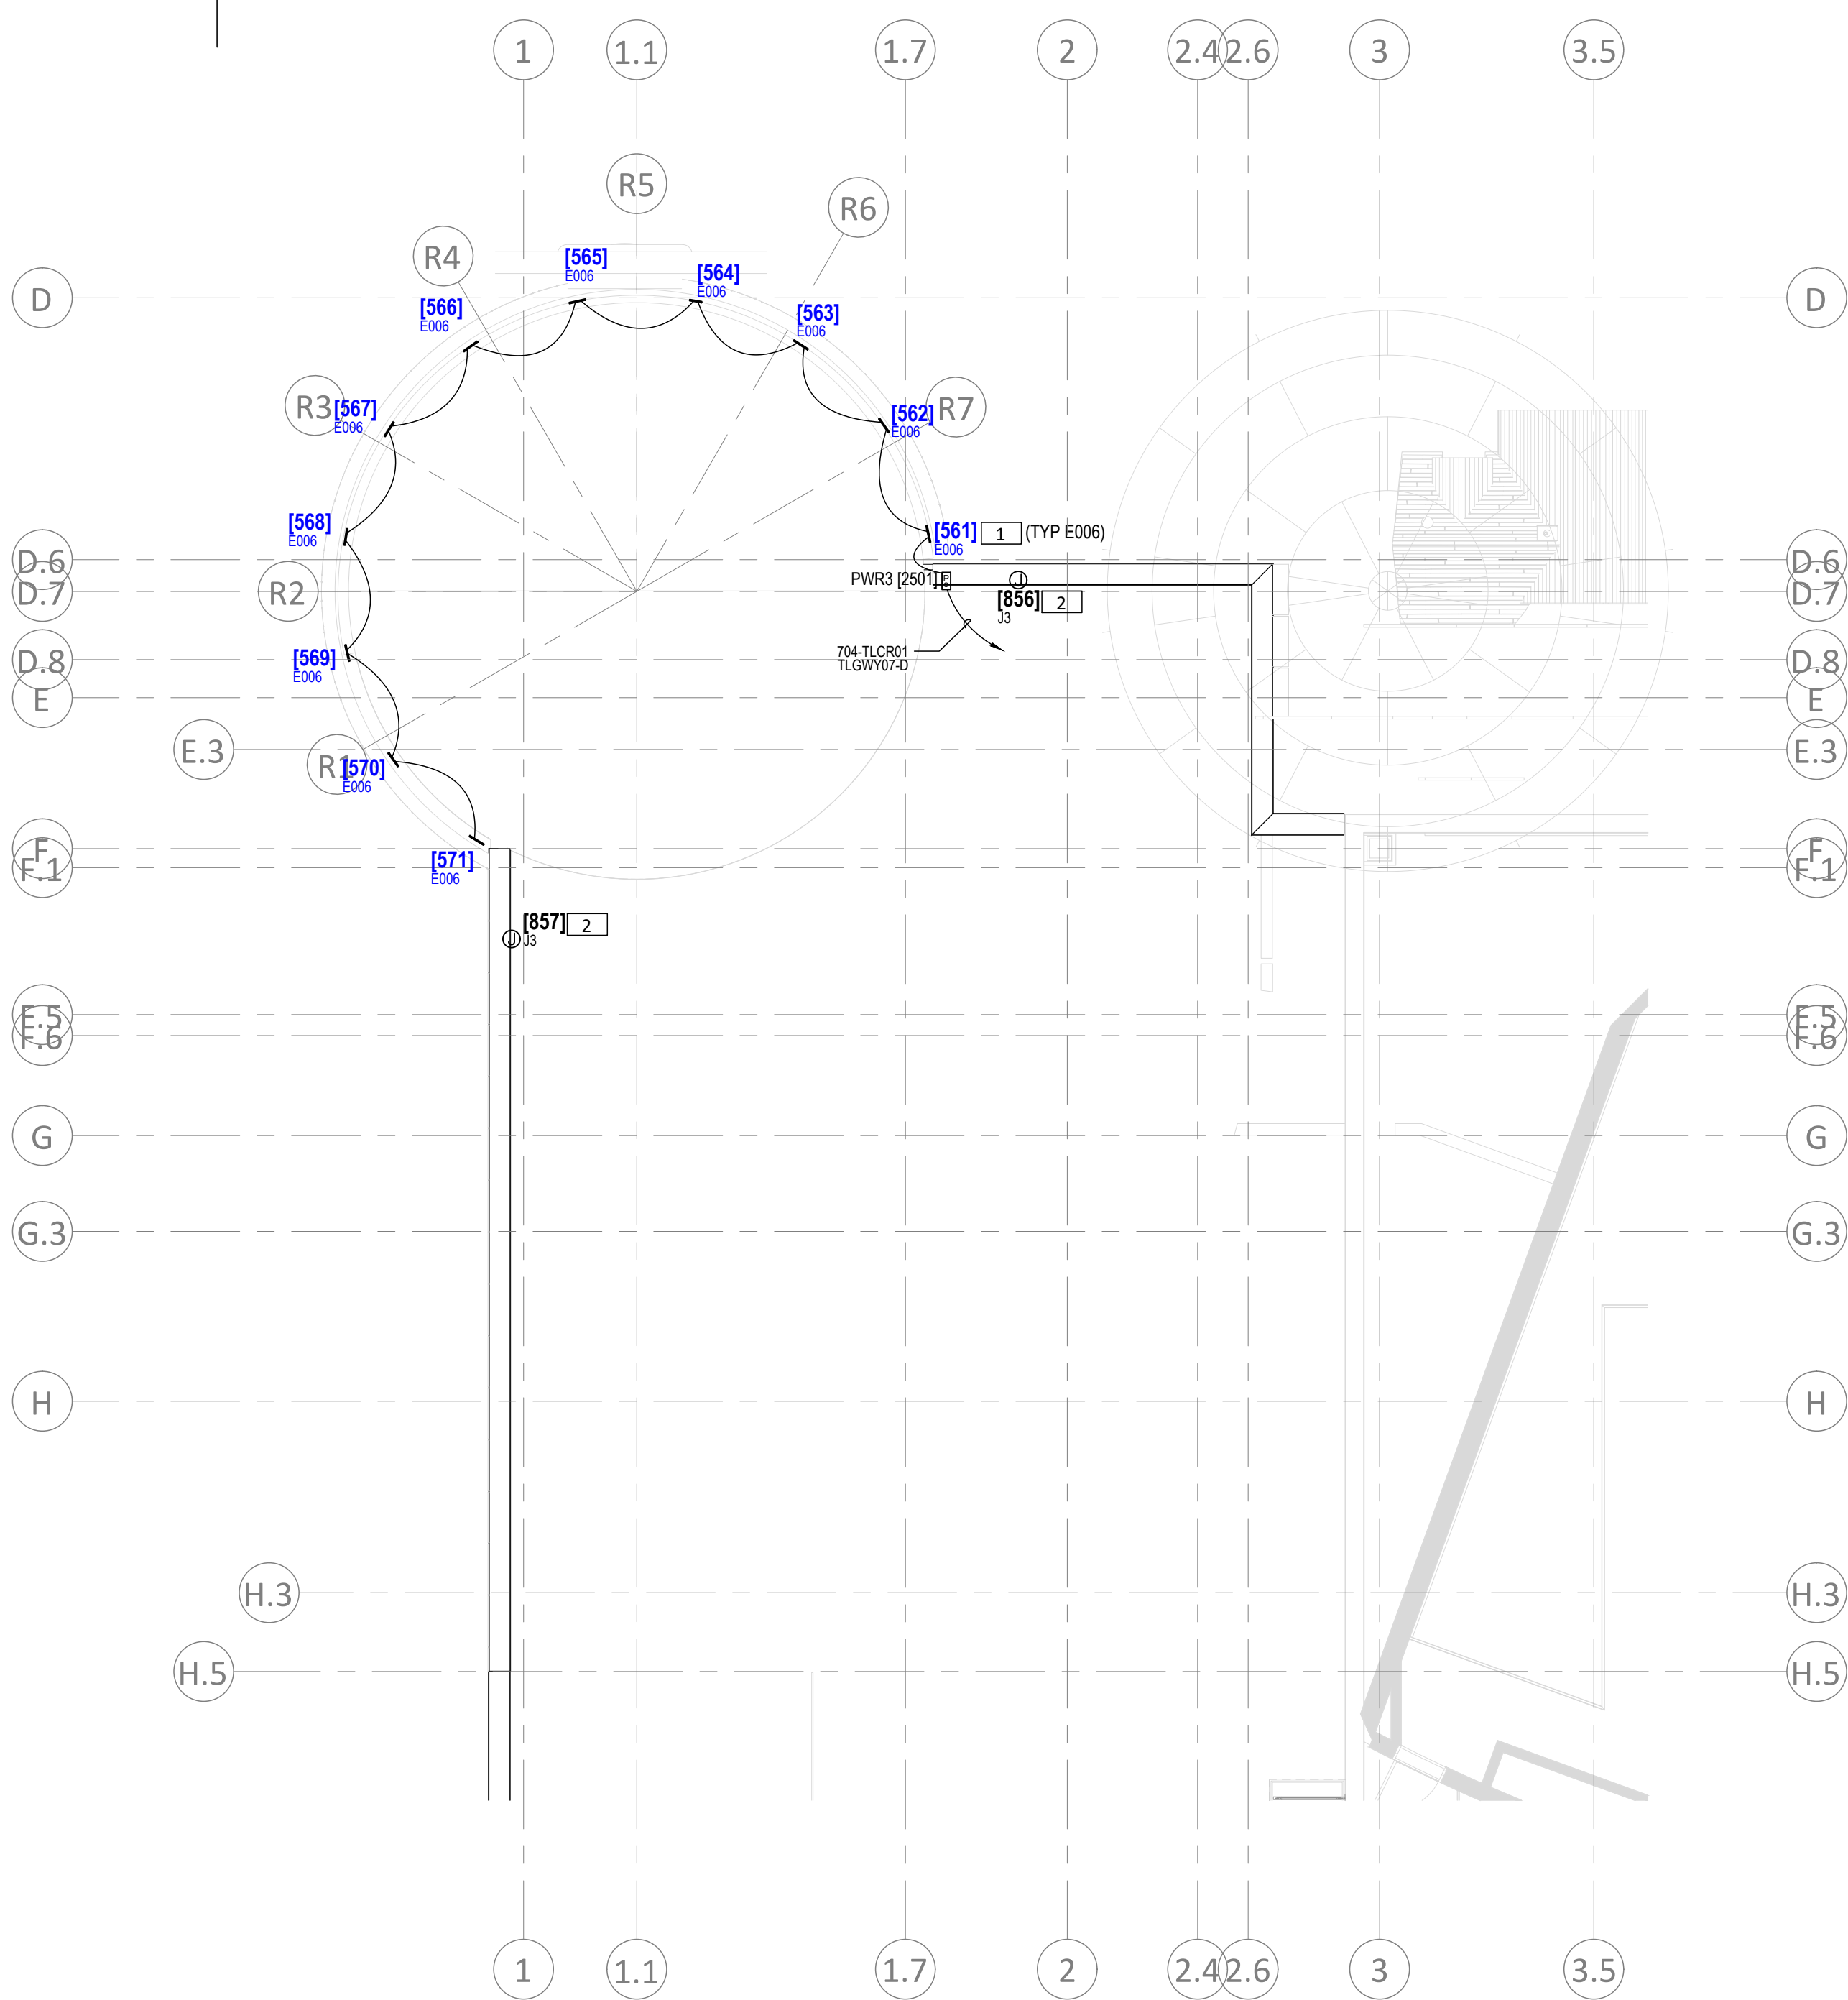


屋顶平面图 - 出口零售区 - 主题灯光
ROOF PLAN - EXIT RETAIL - THEMED LIGHTING

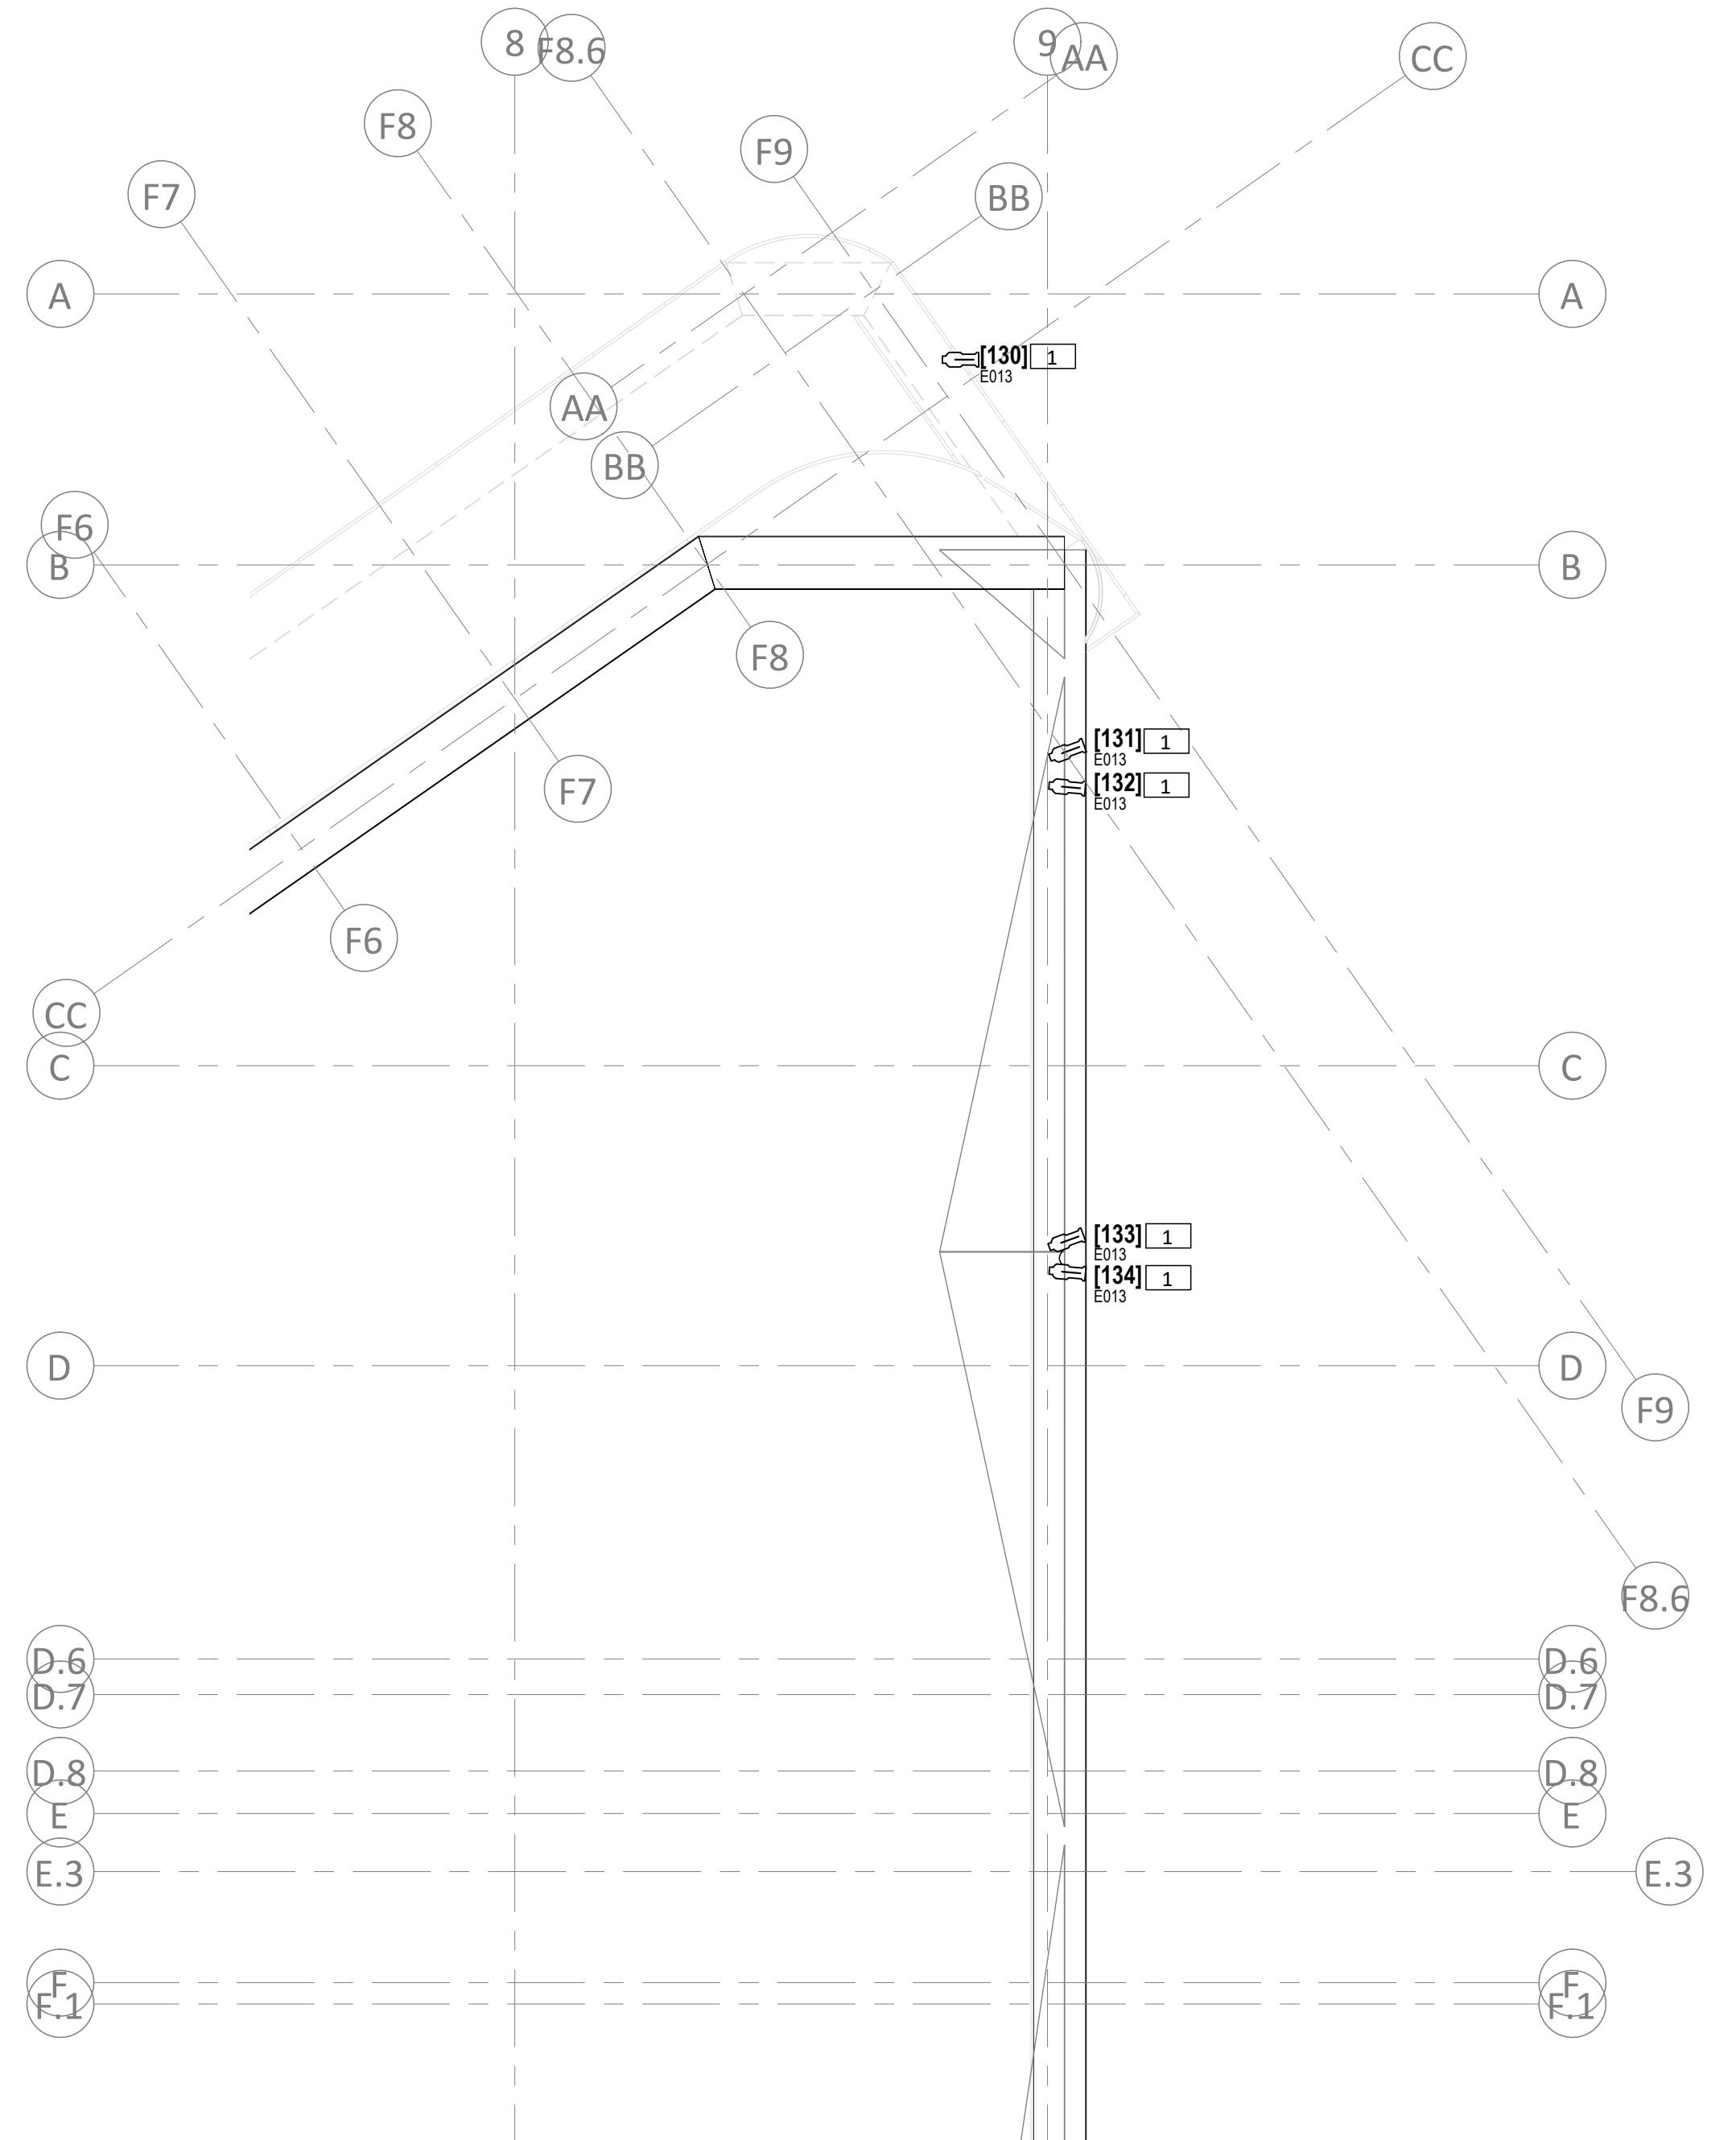


局部屋顶平面图-主题灯光
PARTIAL ROOF PLAN - THEMED LIGHTING - OVERALL

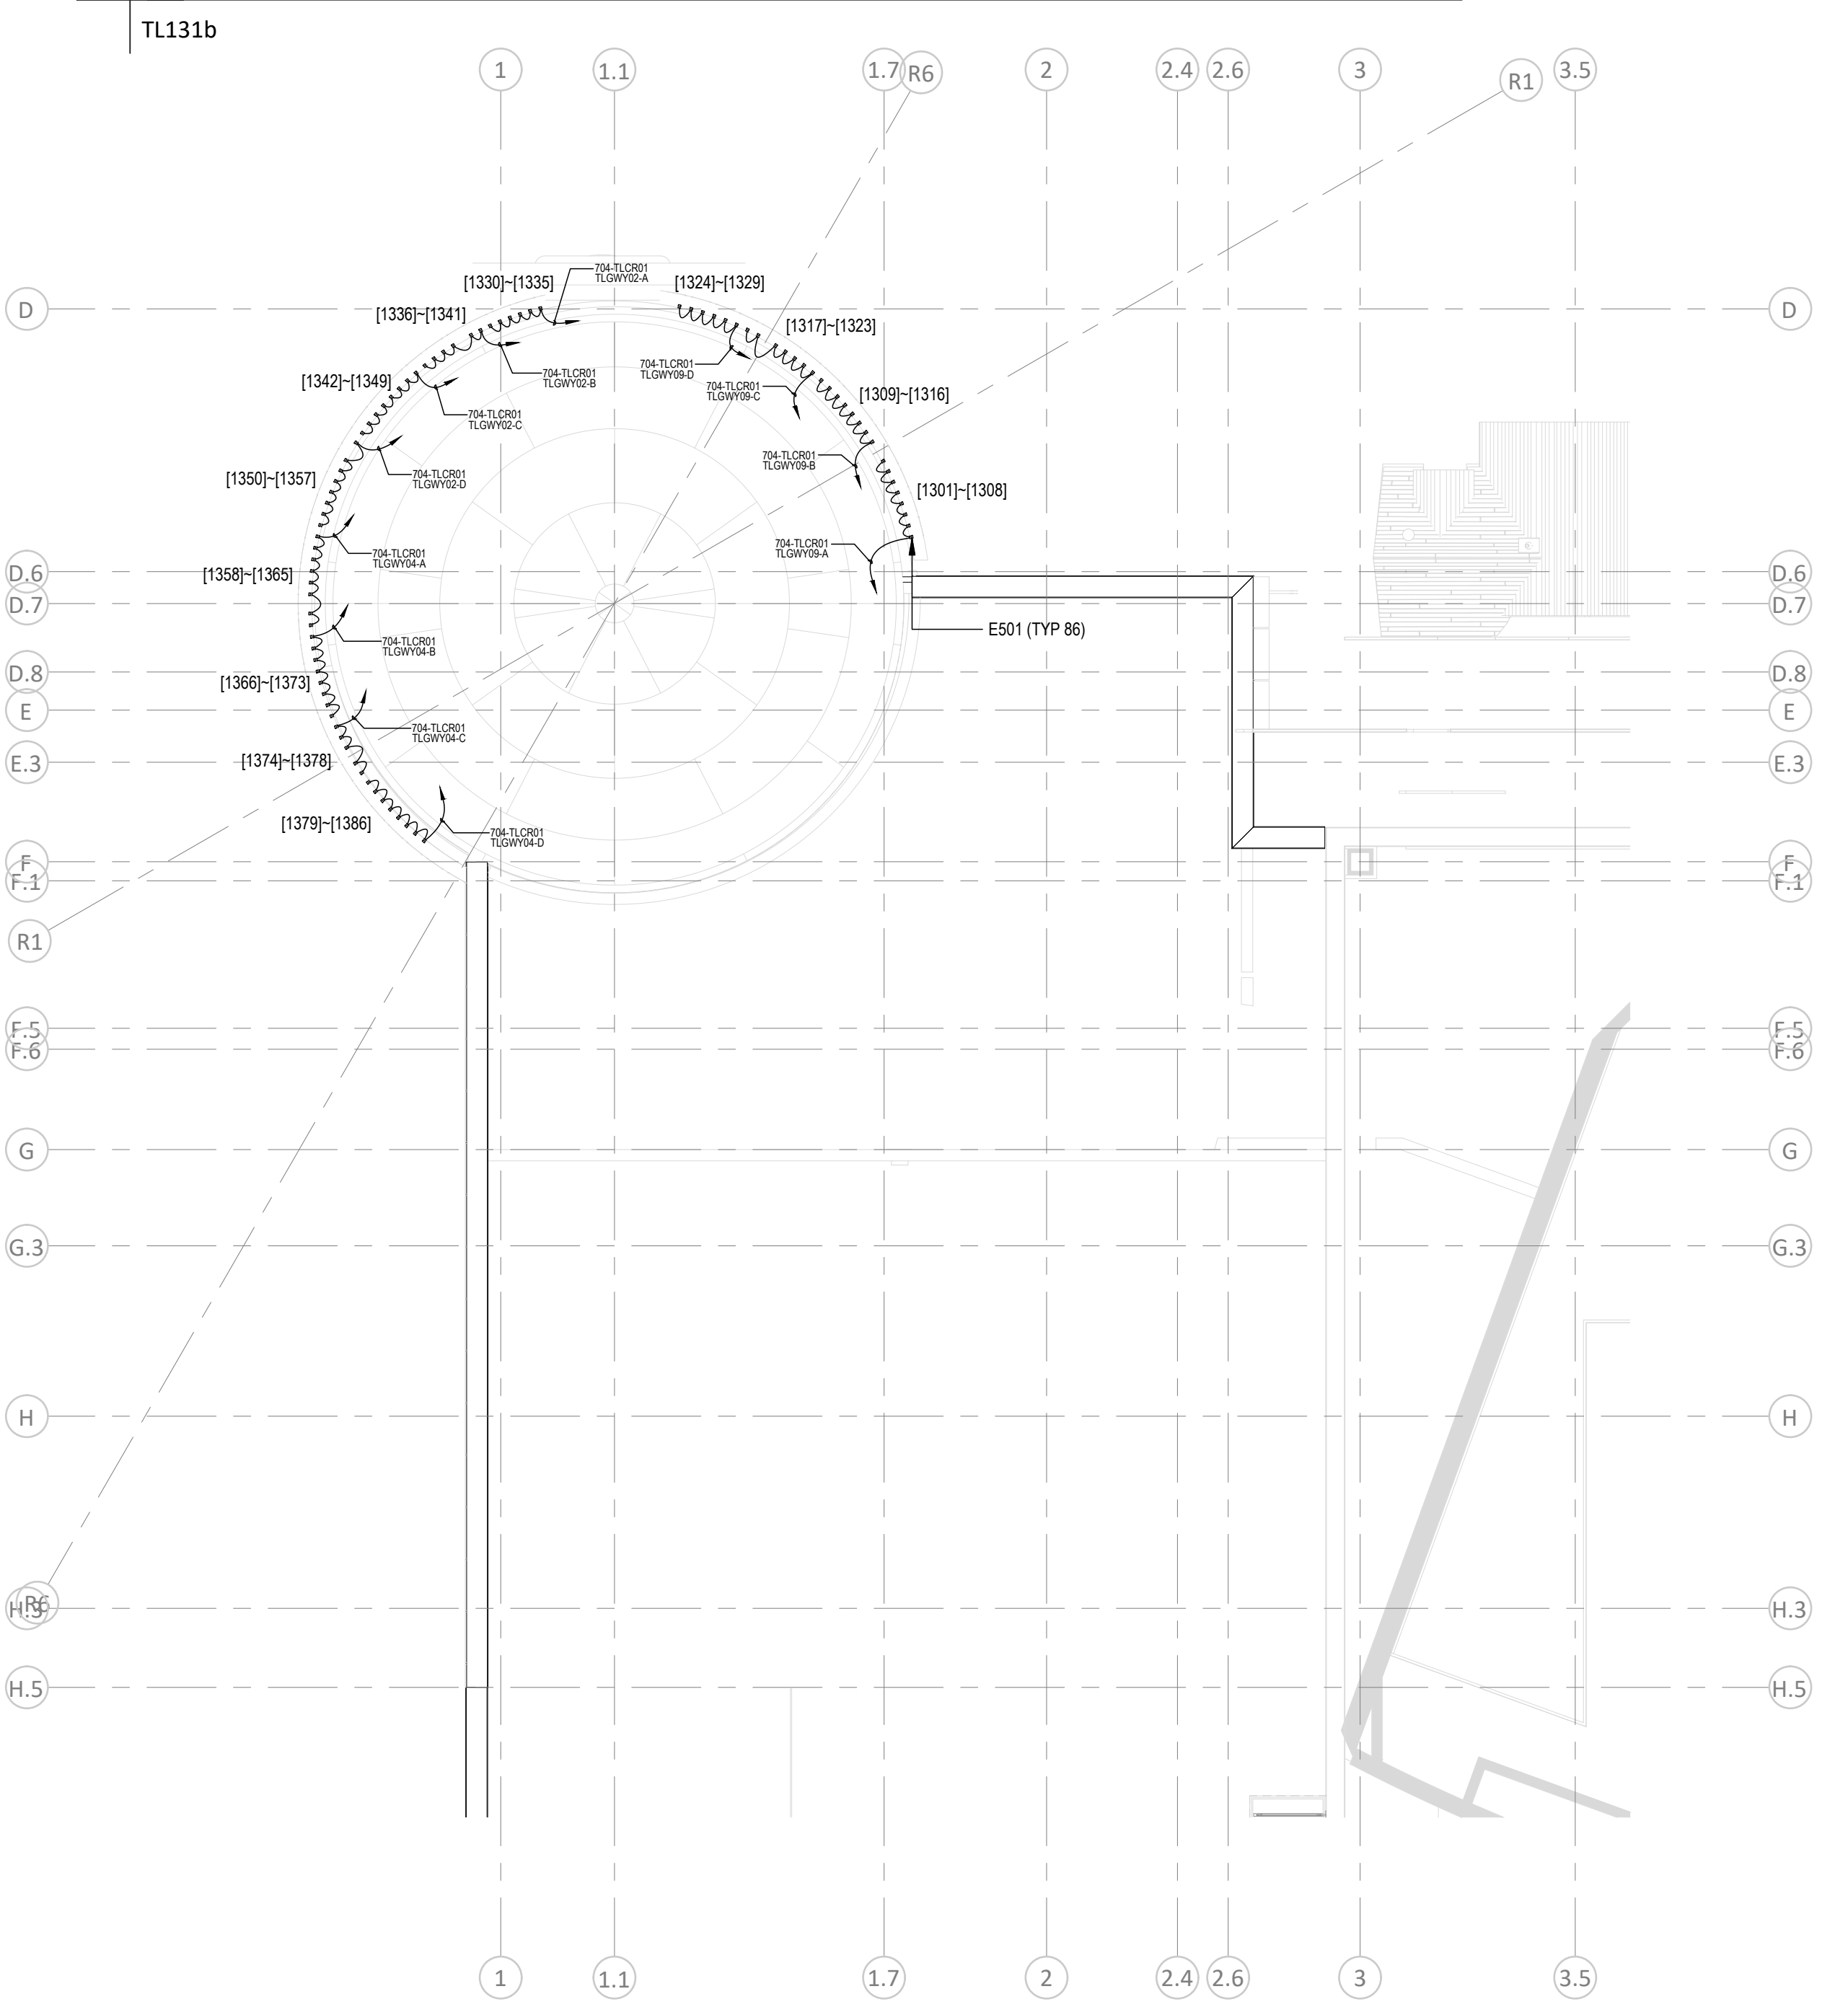

屋顶平面图 - 出口零售区 - 主题灯光
ROOF PLAN - EXIT RETAIL - THEMED LIGHTING

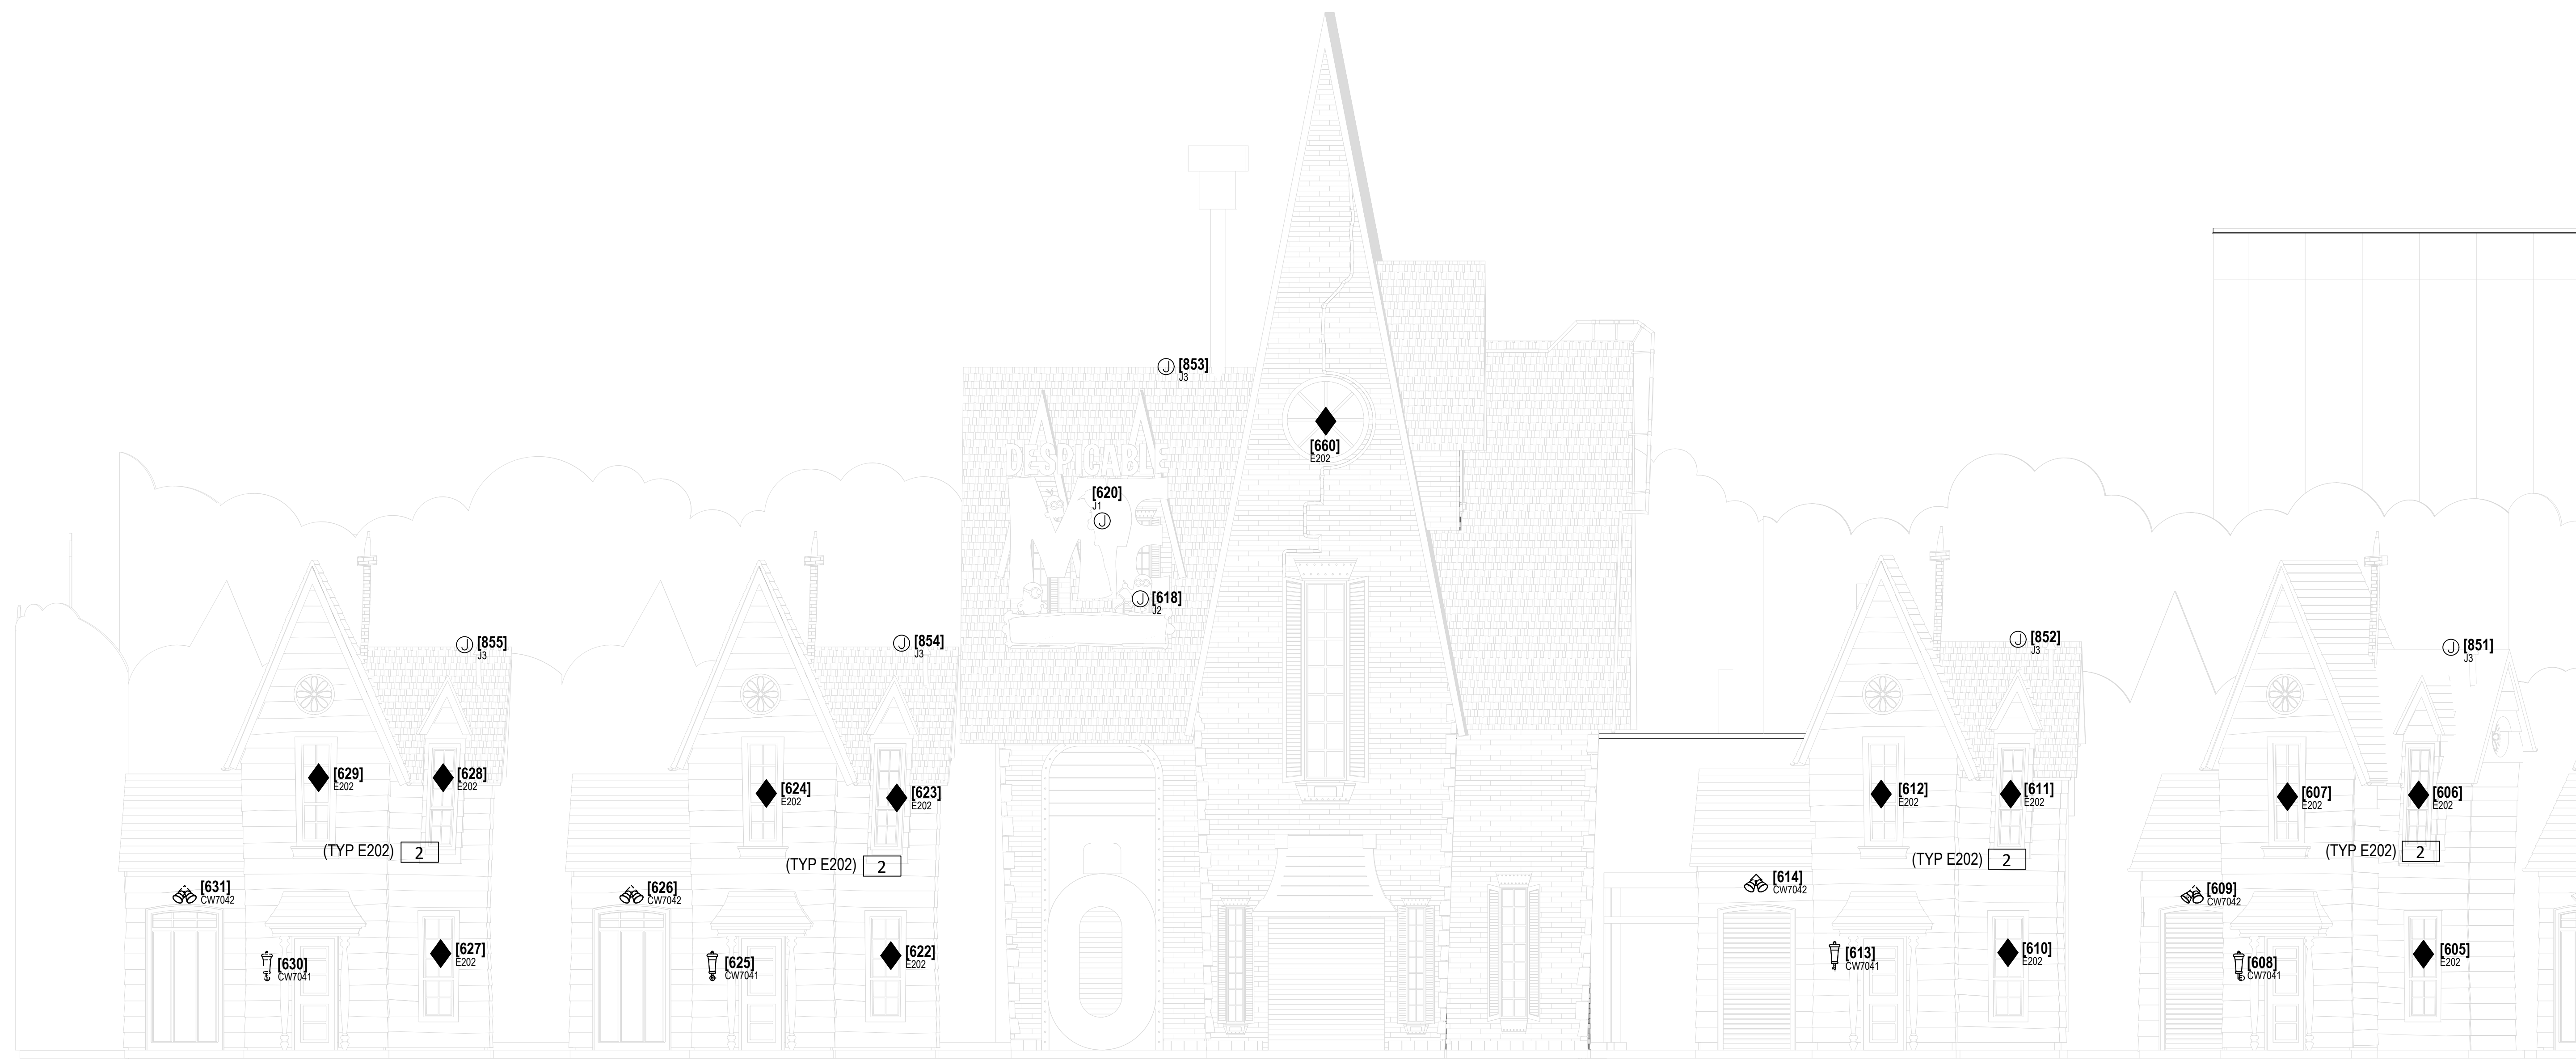

1 ELEVATION - NORTH WEST - THEMED LIGHTING
TL201

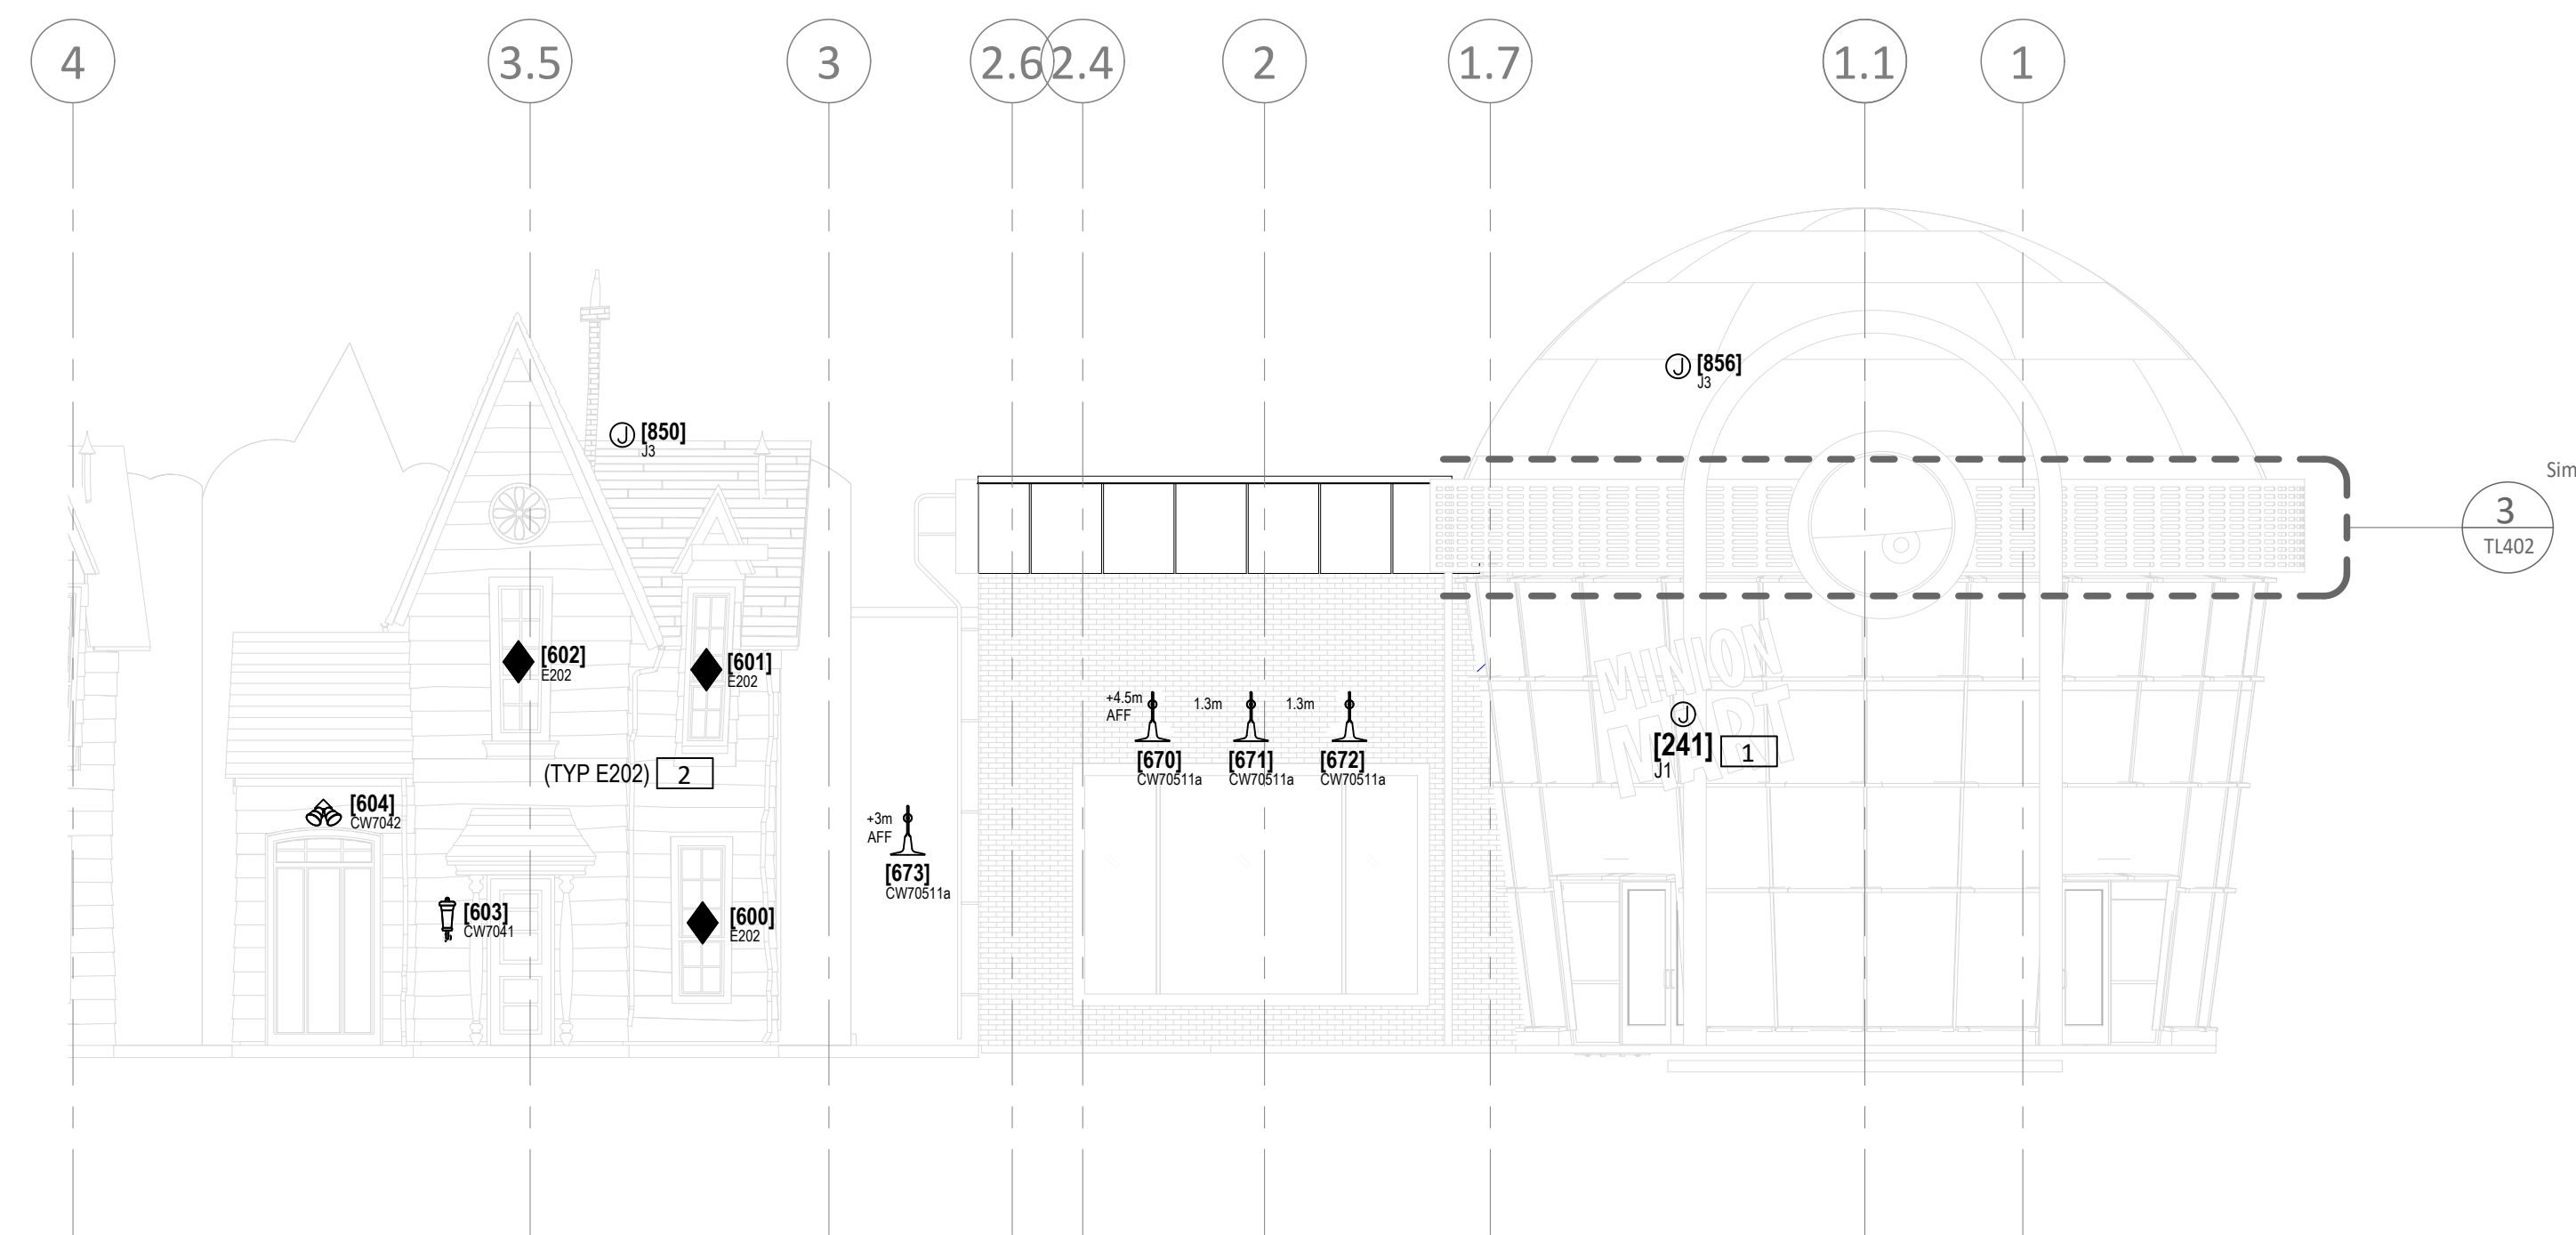

2 ELEVATION - NORTH - THEMED LIGHTING
TL201