




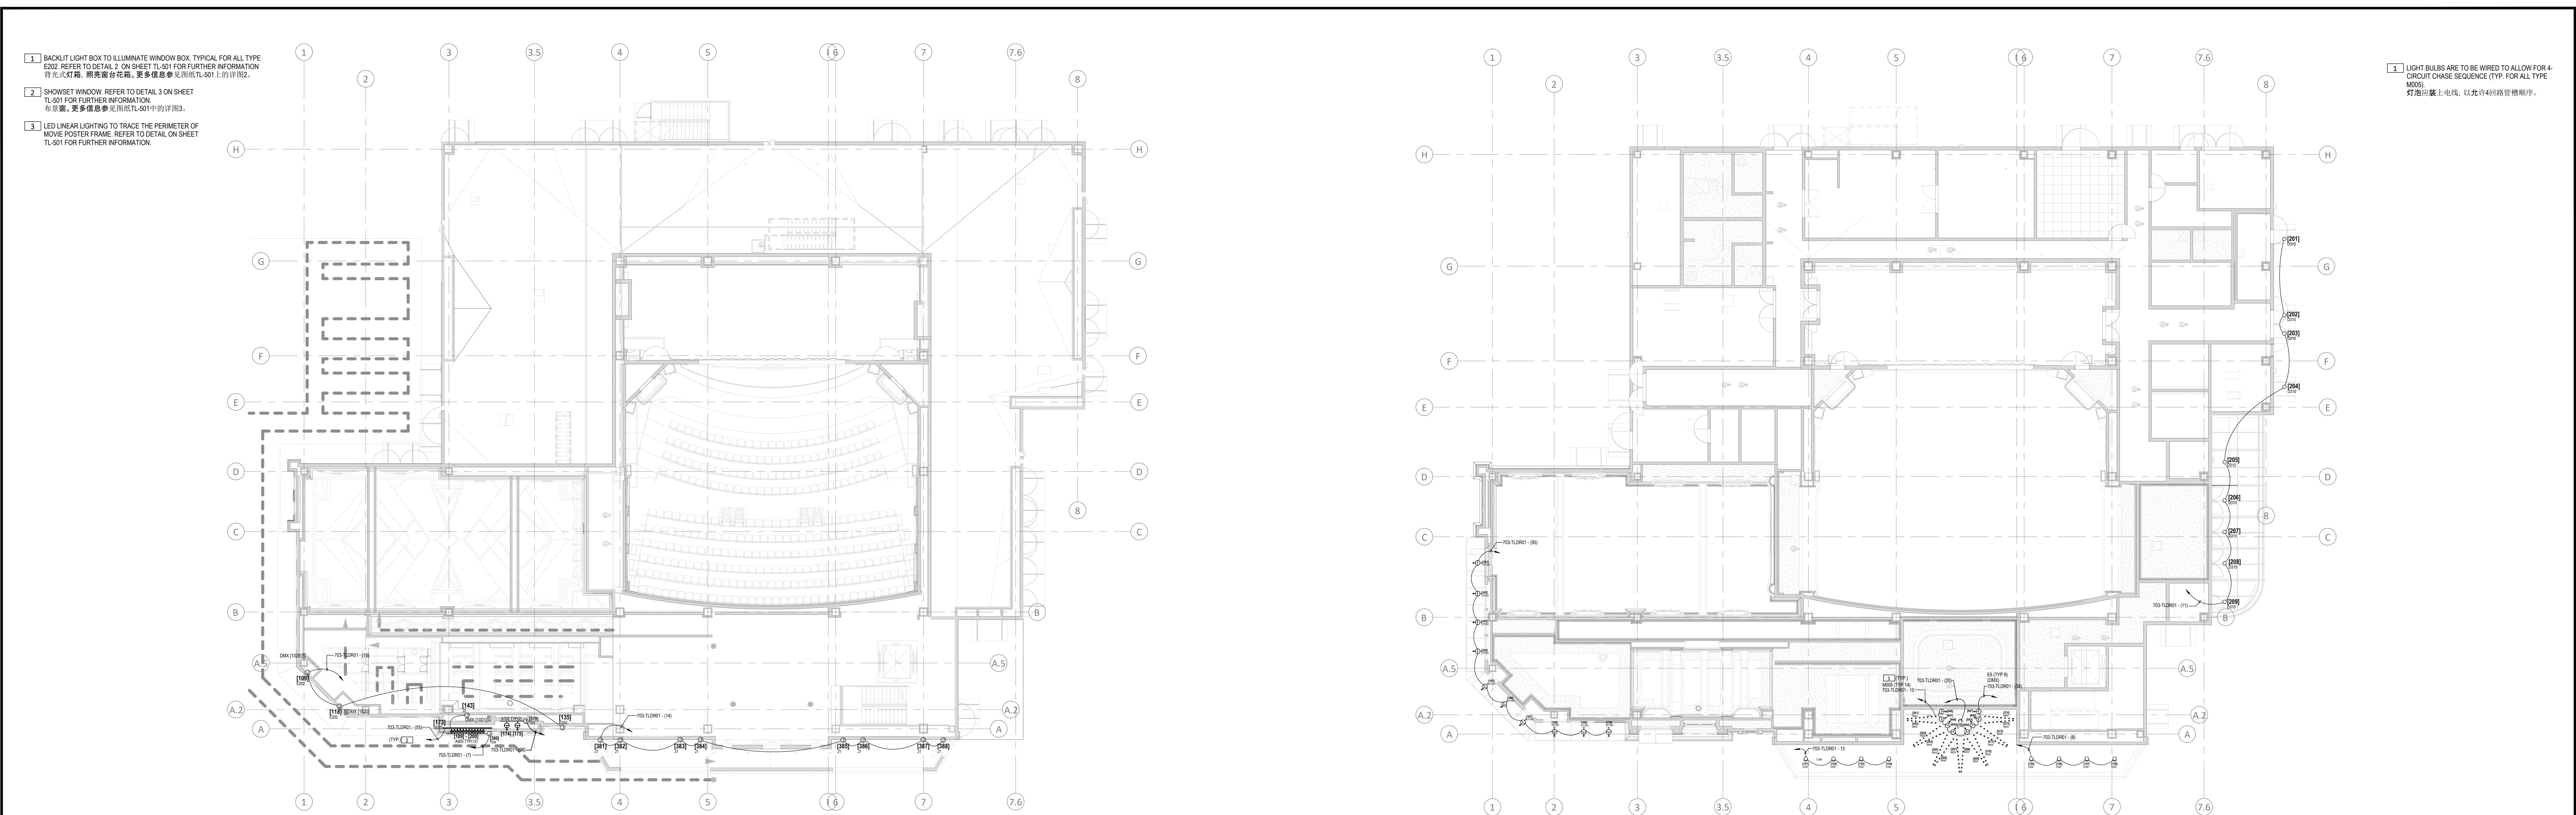


平面图 - 下层 - 主题灯光
FLOOR PLAN - LOWER LEVEL - THEMED LIGHTING

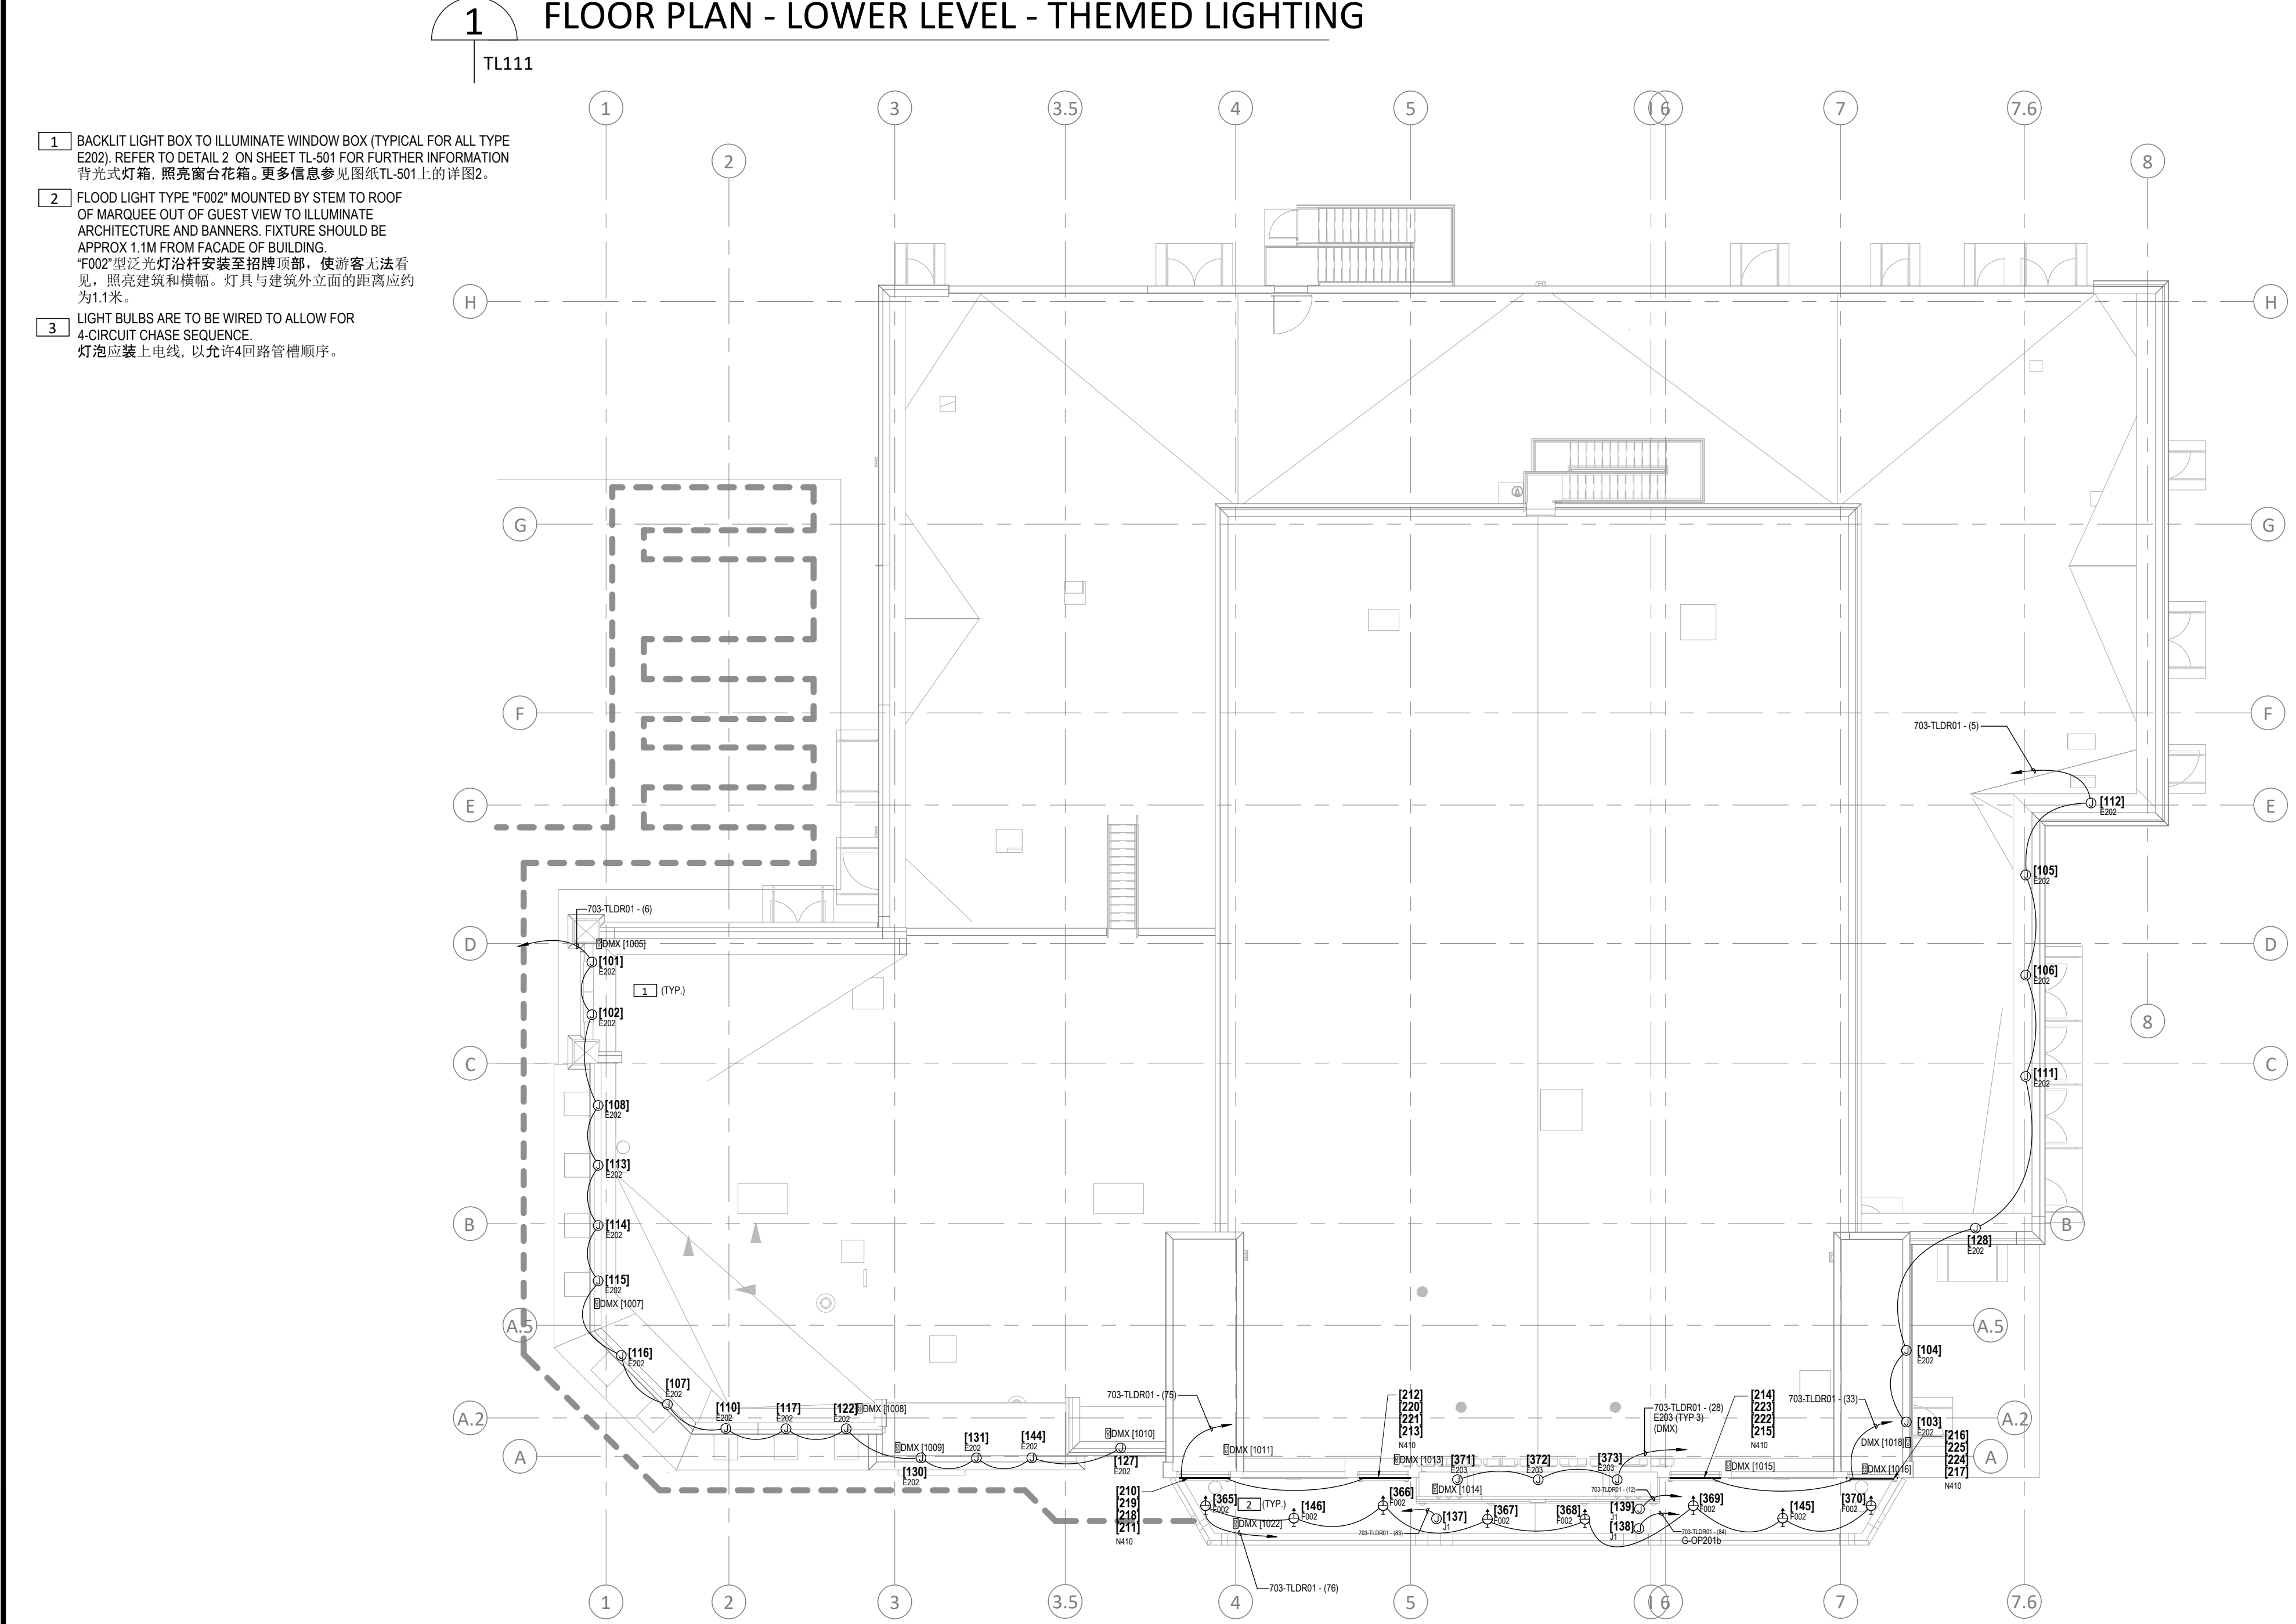

平面图 - 上层 - 主题灯光
FLOOR PLAN - UPPER LEVEL - THEMED LIGHTING

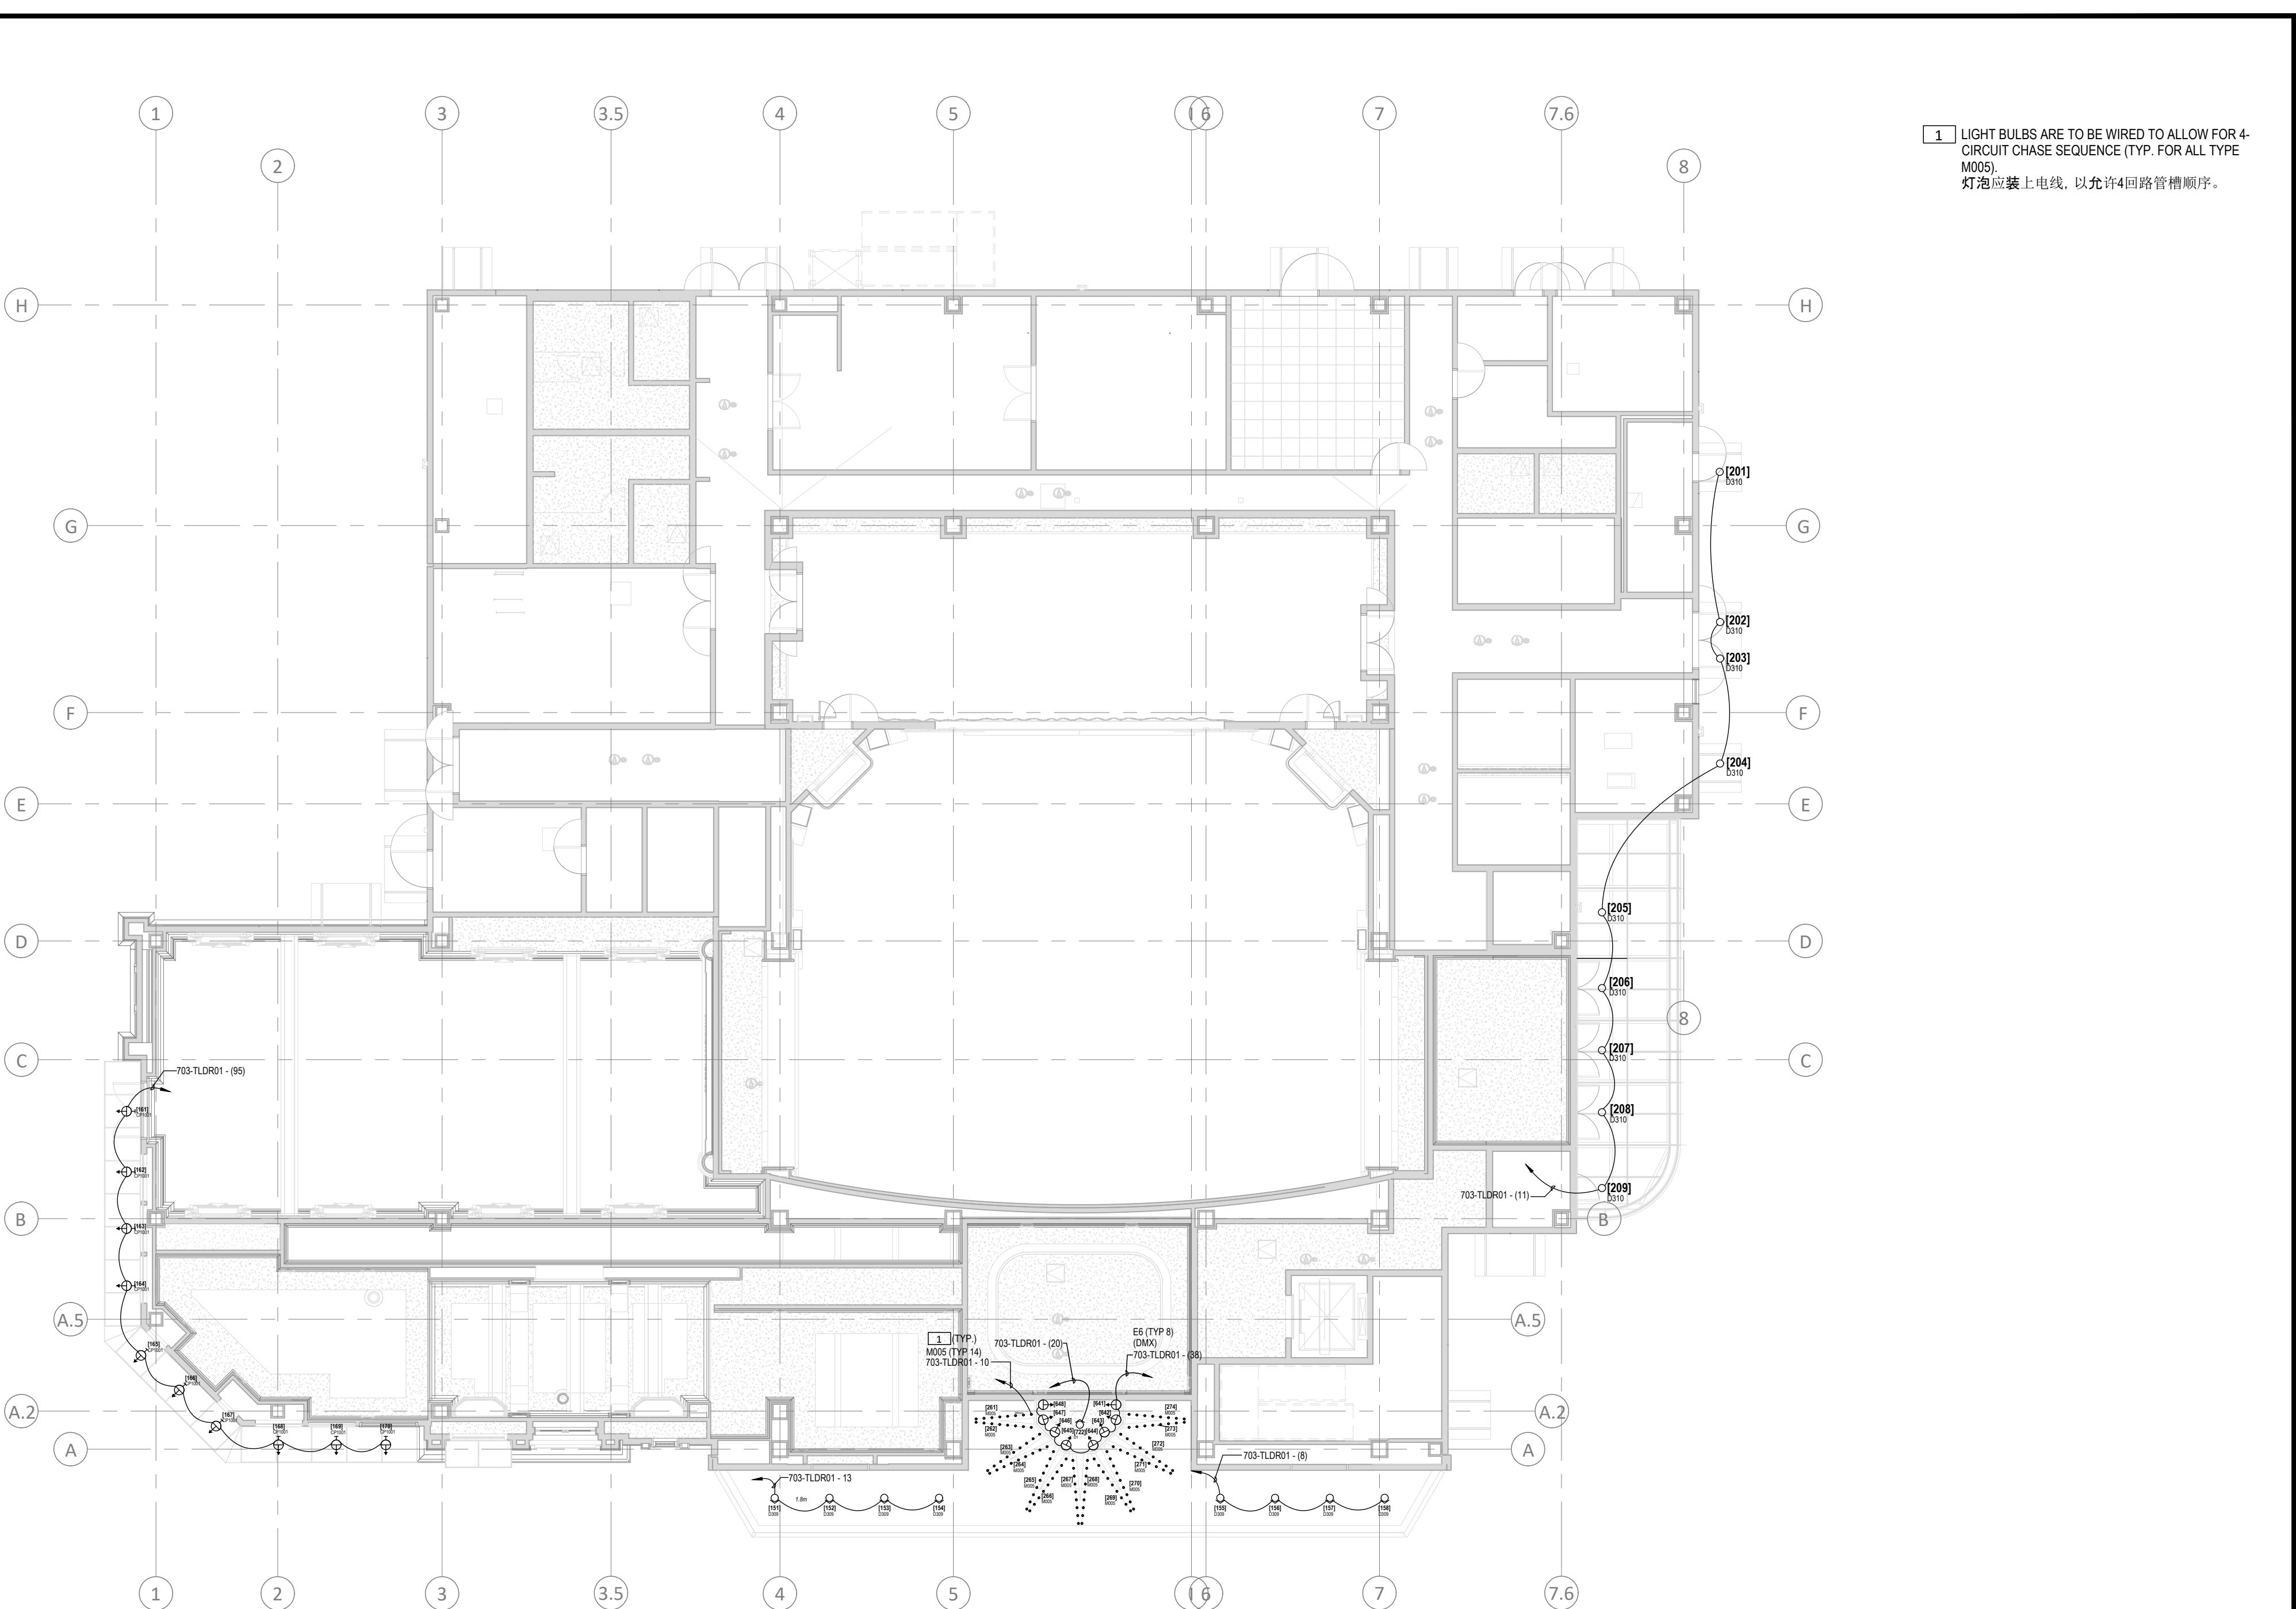

天花板平面图 - 下层 - 主题灯光
CEILING PLAN - LOWER LEVEL - THEMED LIGHTING

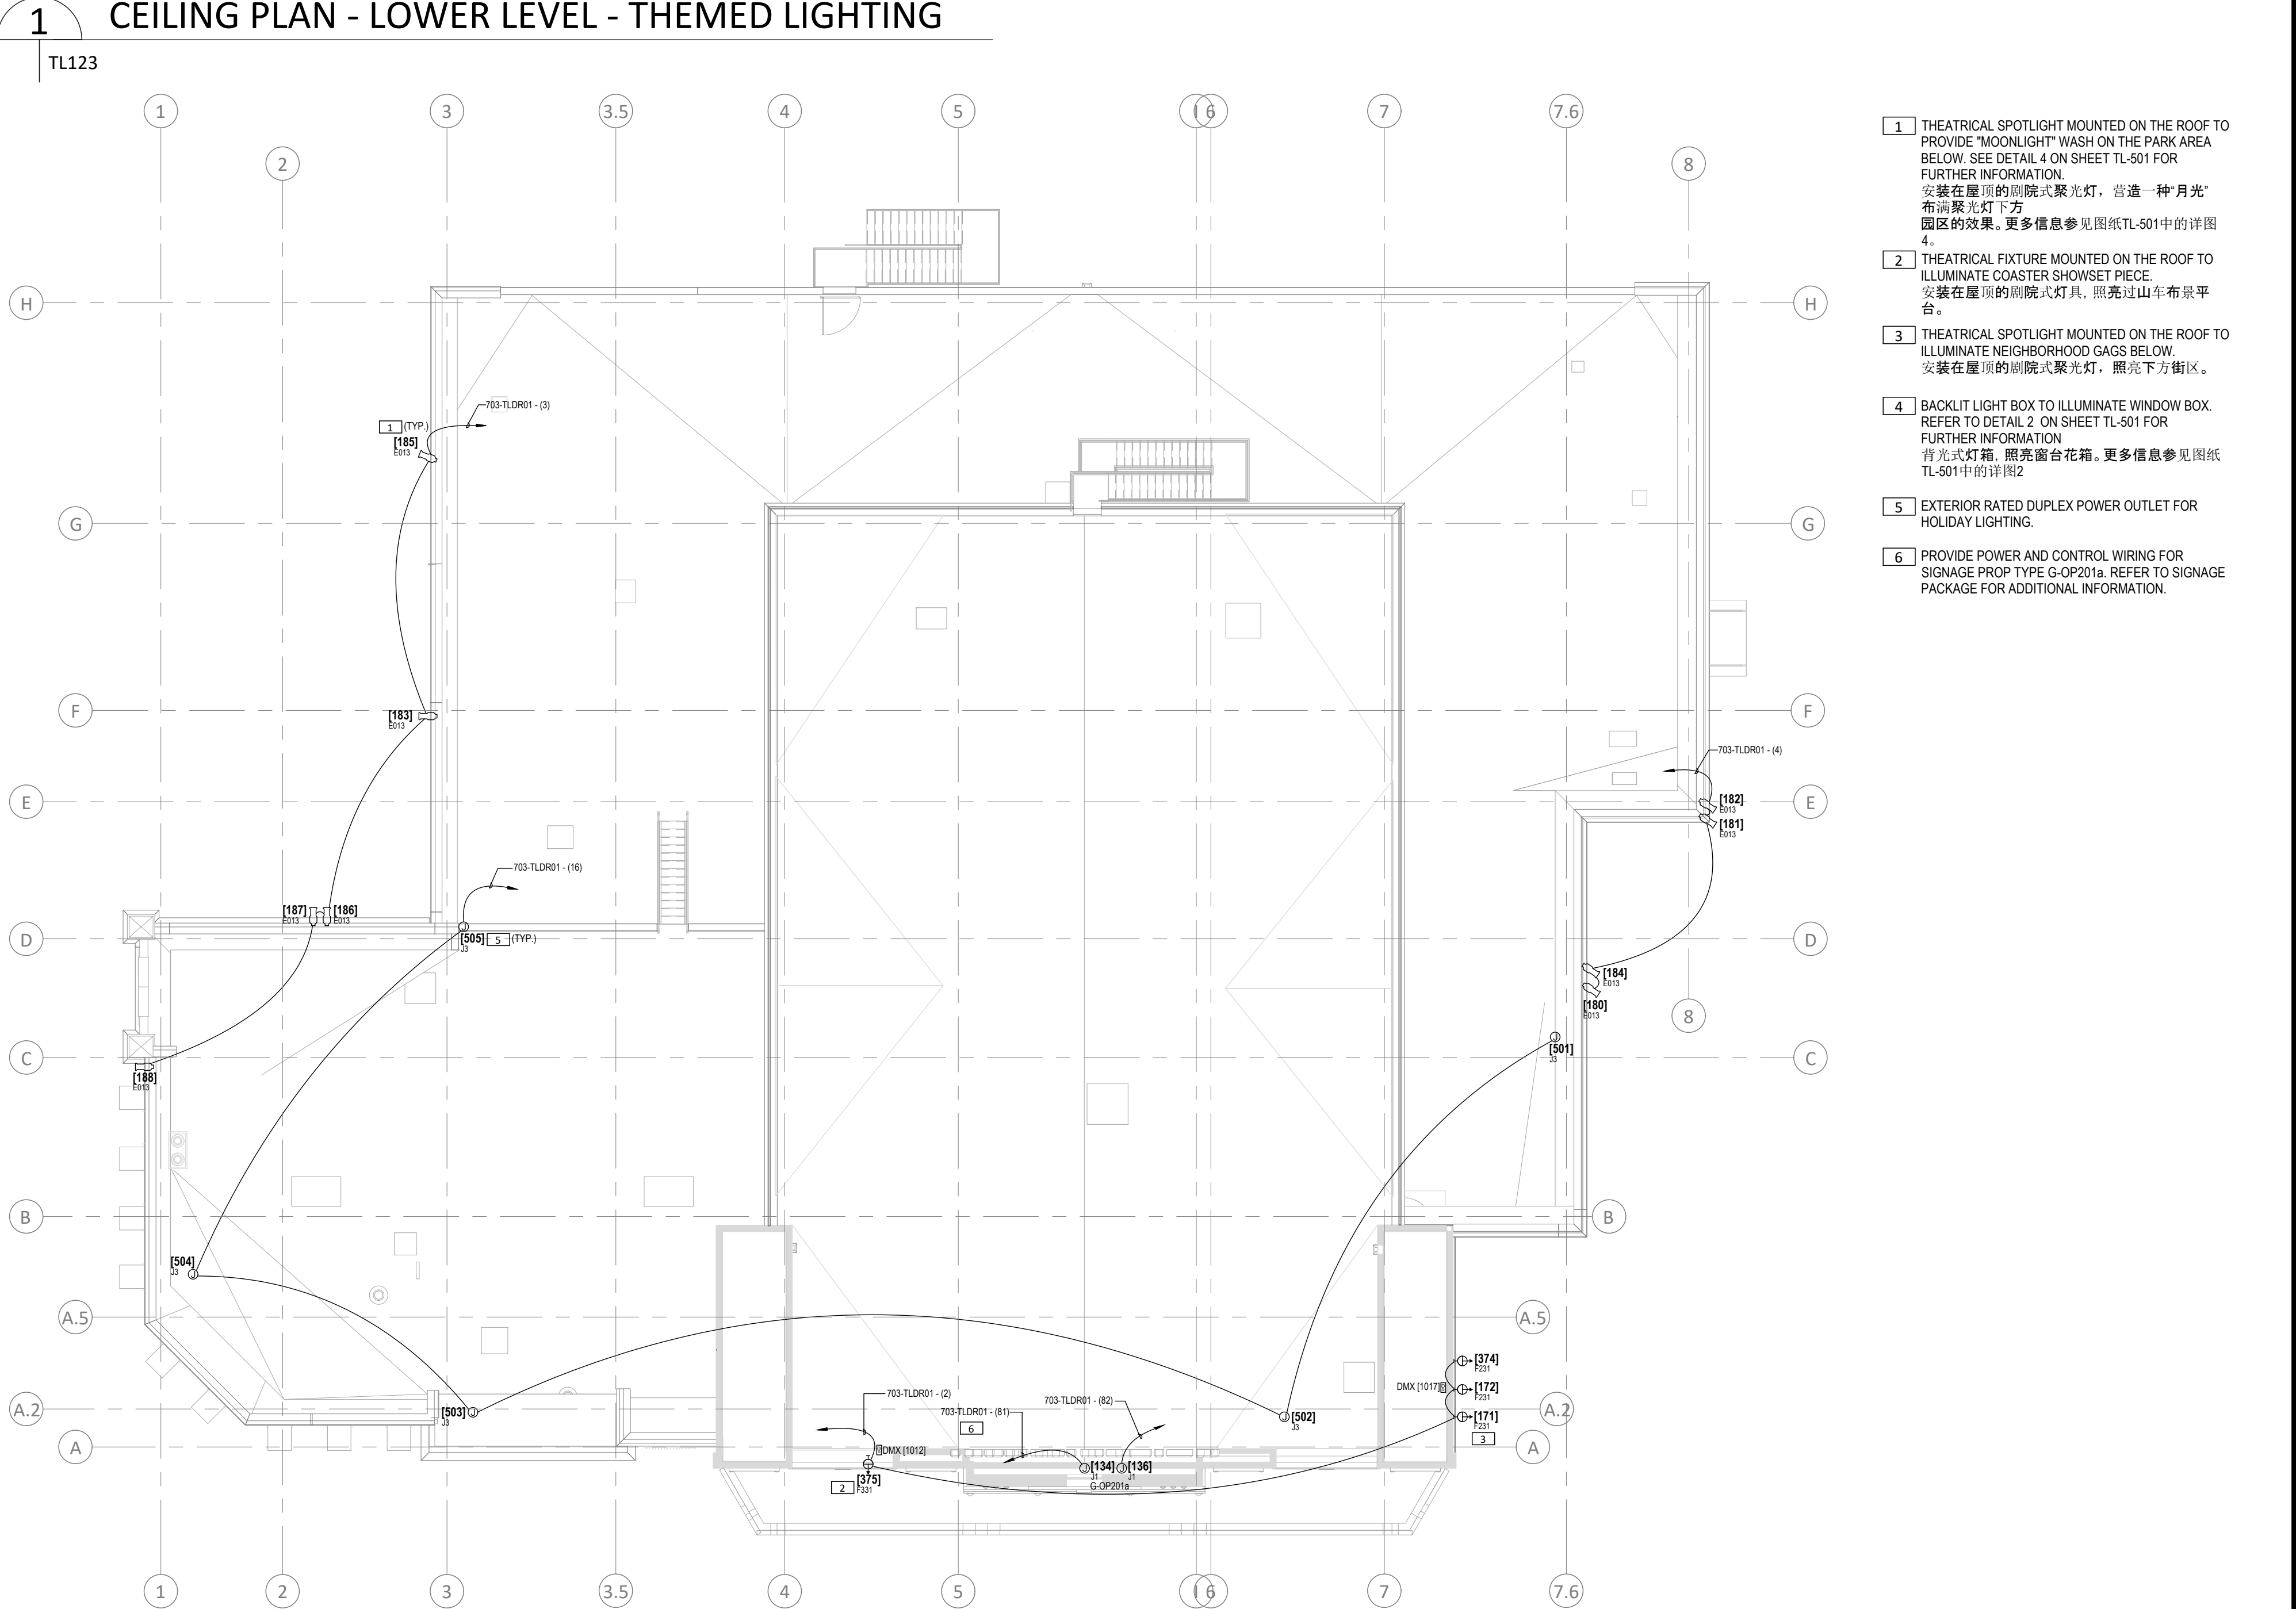

屋顶平面图 - 主题灯光
ROOF PLAN - THEMED LIGHTING

-
- 立面图 - 北 - 主题灯光
ELEVATION - NORTH - THEMED LIGHTING